

특기사항
NOTE

공간 활용도를 높이기 위해 기존 복도 상한 위치를 제외한 영역까지 상가 공간을 확장하였다. 열람공간 내부의 안치 형태가 다소 이질적으로 보이는 부분은 보다 원형에 가까운 형태로 다듬어 공간의 자연스러운 인상을 강화하였다. 기존에는 서가존을 복도 유리면 쪽에 집중 배치하여 다소 폐쇄적인 느낌이 있었으나, 이를 휴게실 하부 벽면 쪽으로 이동 집중 배치해 시야가 트이도록 조정하였다. 또한 기존 전열수납대의 수량을 줄이고, 단순 수납 기능보다 전시 효과를 강조한 디스플레이 서가로 변경하였다. 그 외 커튼월의 1인 좌석 공간과 복도 창가에는 2인용 테이블과 의자를 배치하여 좌석 선택의 다양성을 높이고, 간체적으로 보다 자유롭고 개방적인 분위기를 유도하였다.

수정사항
REVISION


번호 NO	일 자 DATE	수 정 DESCRIPTION	날 인 SIGN
△			
△			
△			
△			
△			
△			
△			
△			
△			
△			

공사명
PROJECT TITLE축척
SCALE작성일
DATE설계
DESIGNED BY제 도
DRAWN BY검 사
CHECKED BY승 인
APPROVED BY도면명
NAME OF DRAWING도면번호
DRAWING NO

--	--	--	--	--

시공번호
PROJECT NO

TD				
----	--	--	--	--

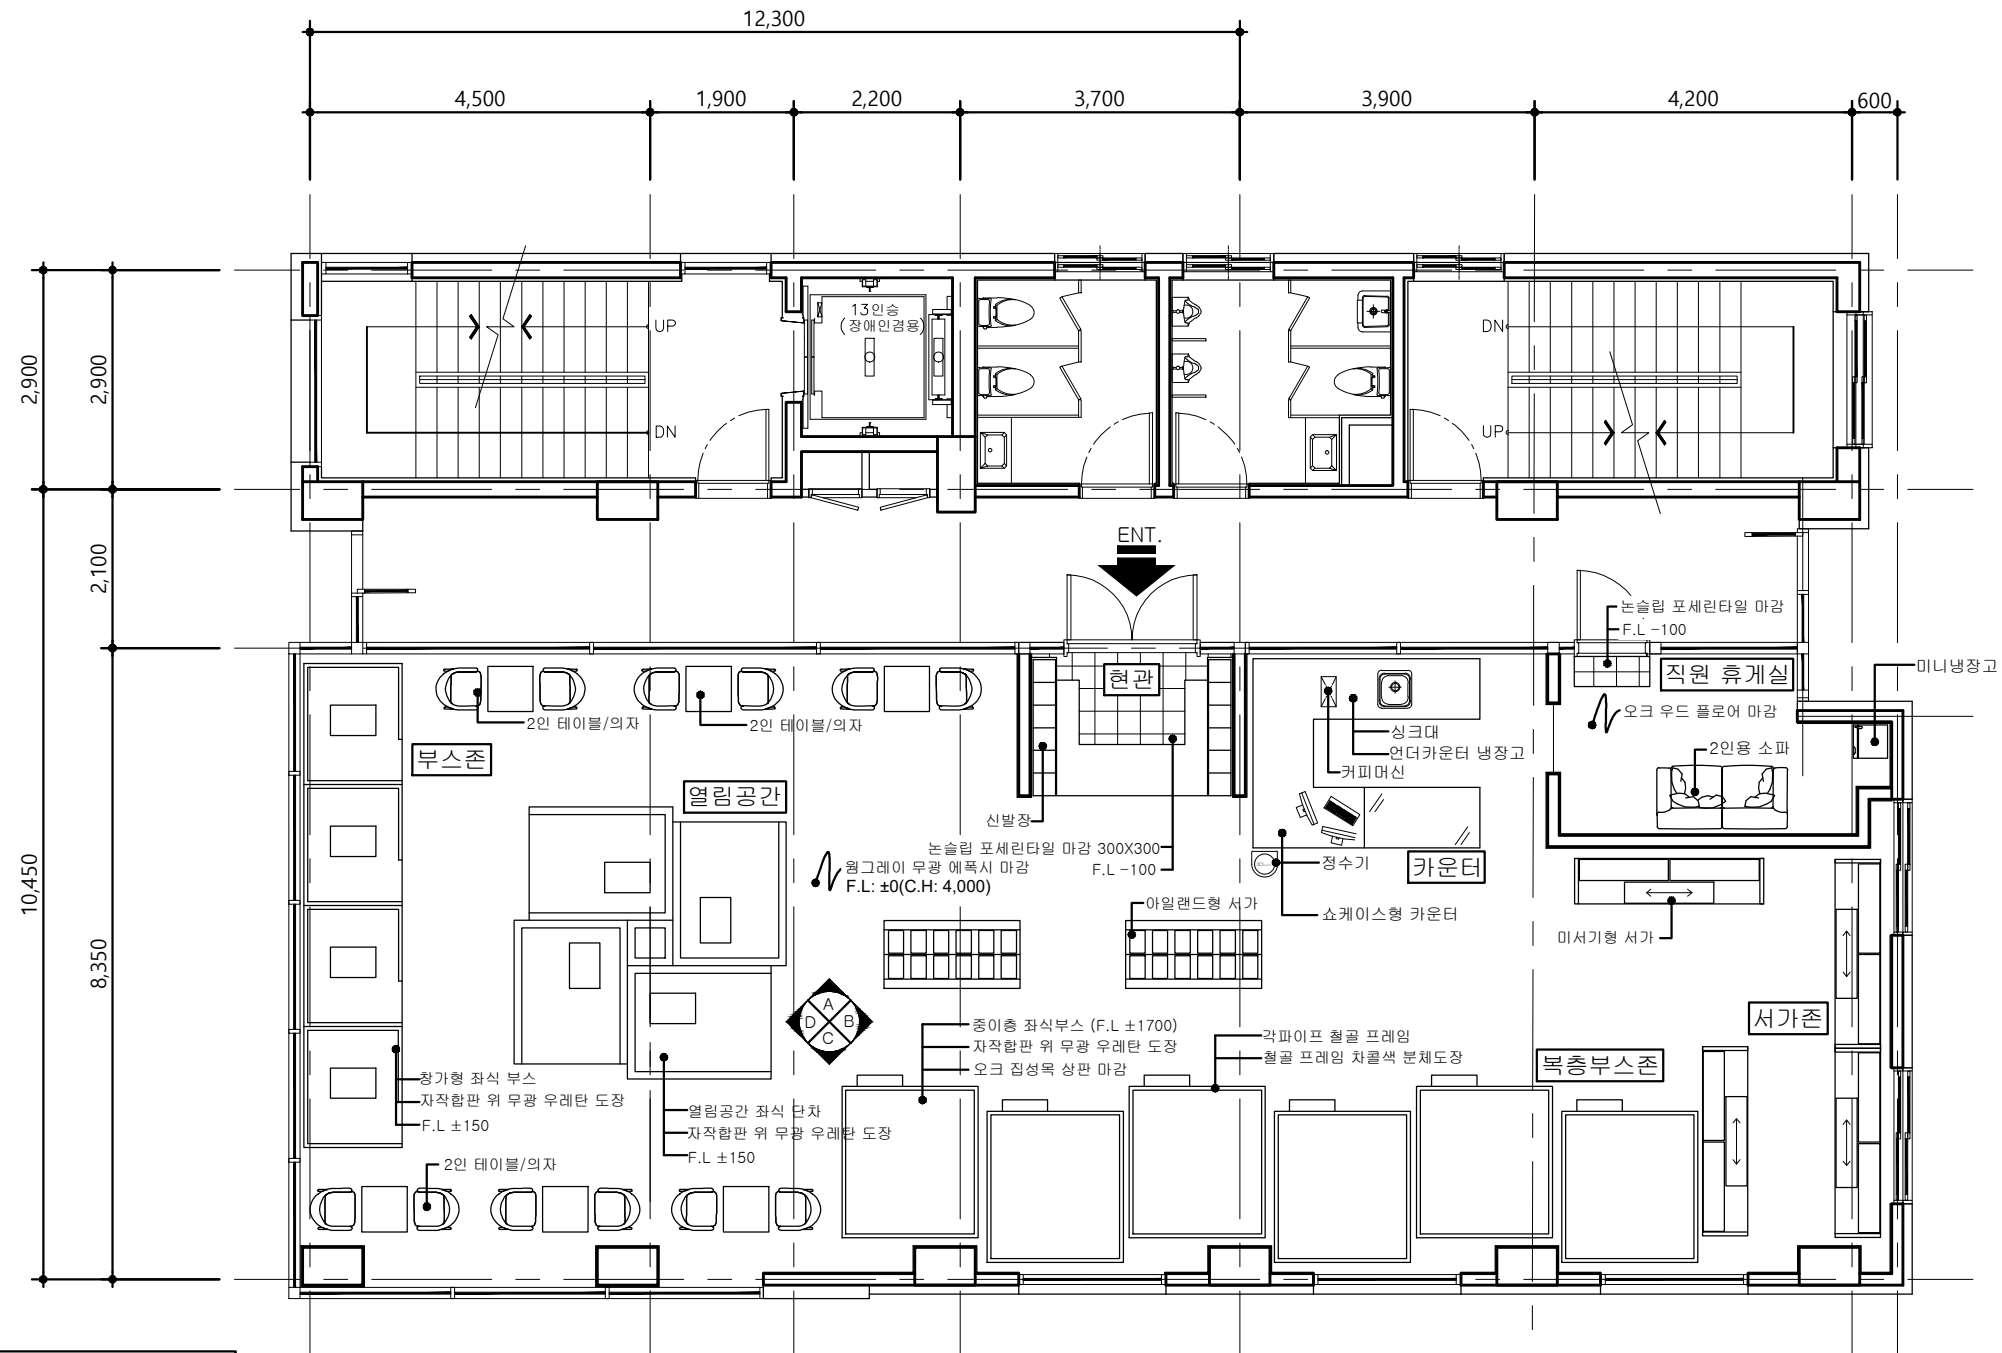

*디자인 의도

상가 내 위치한 만화가페로, 이용객이 편안하게 머물며 독서와 휴식을 함께 할 수 있도록 공간을 구성하였다. 외부 채광을 적극 활용하여 창가에는 1인 테이블과 좌석을 배치하고, 중앙에는 낮은 가구와 좌식 공간을 계획하여 개방감을 확보하였다. 반면 채광이 적은 공간에는 중이층 형태의 좌식 공간을 두어 보다 아늑하고 독립적인 분위기를 조성하였다. 이용객의 주요 동선에는 서가와 수납가구를 배치하여 자연스럽게 다양한 만화책과 공간을 접할 수 있도록 하였으며, 카운터와 직원 휴게공간을 가까이 배치하여 직원의 이동 동선을 줄였다. 또한 신발장과 좌식공간을 구분하여 신발 정리와 이용이 편리하도록 계획하였다.

평면도

축척 1/100

특기사항
NOTE

수정사항
REVISION

번호 NO	일 자 DATE	수 정 DESCRIPTION	날 인 SIGN
△			
△			
△			
△			
△			
△			
△			
△			
△			

공사명
PROJECT TITLE

축 척
SCALE

작성일
DATE

설 계
DESIGNED BY

제 도
DRAWN BY

검 사
CHECKED BY

승 인
APPROVED BY

도면명
NAME OF DRAWING

도면번호
DRAWING NO


--	--	--	--	--	--

시공번호
PROJECT NO

TD					
----	--	--	--	--	--

※범례

기 호	명 칭	수량
⊕	매입등	6
⊕	화재 감지기	4
●	스피커	3
■	환풍기	8
□	1WAY 에어컨	1
□	점검구	1
⊕	분전트	39
□	사각 LED 평판등 3000~5000 축척 1/10	3
□	4WAY 에어컨	3

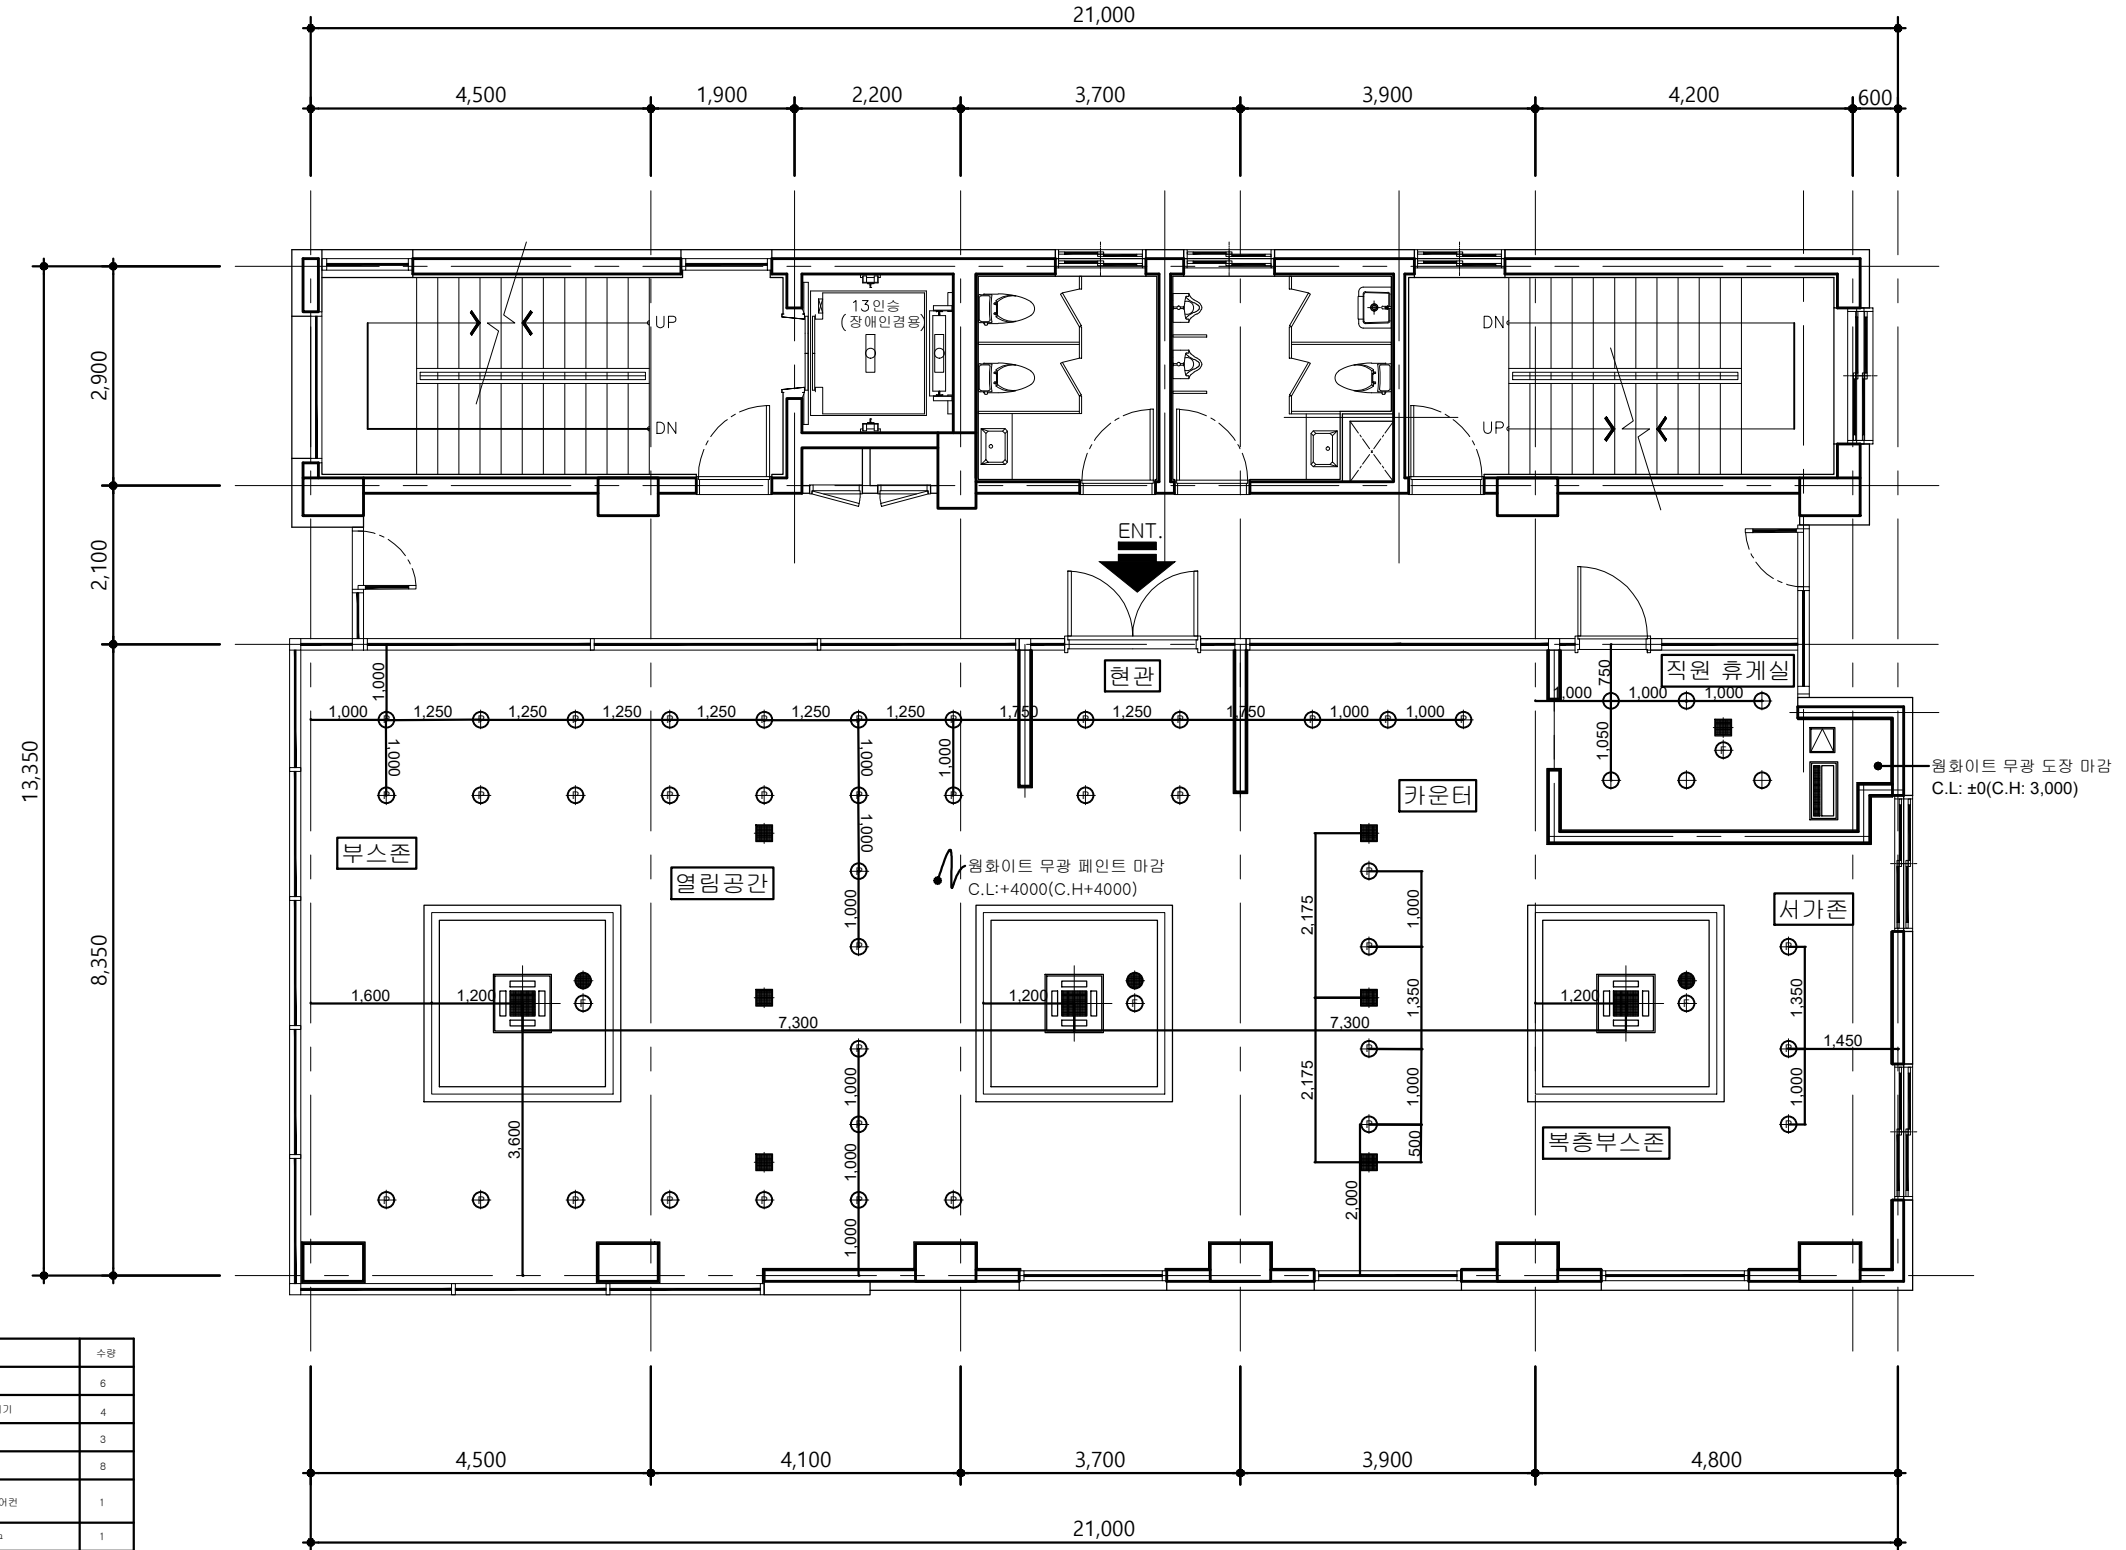

천 장 도

축척 1/100

특기사항
NOTE

수정사항
REVISION

번호 NO	일 자 DATE	수 정 DESCRIPTION	날 인 SIGN
△			
△			
△			
△			
△			
△			
△			
△			
△			

공사명
PROJECT TITLE

축 척
SCALE

작성일
DATE

설 계
DESIGNED BY

제 도
DRAWN BY

검 사
CHECKED BY

승 인
APPROVED BY


도면명
NAME OF DRAWING

도면번호
DRAWING NO

--	--	--	--	--	--


사업번호
PROJECT NO

TD					
----	--	--	--	--	--

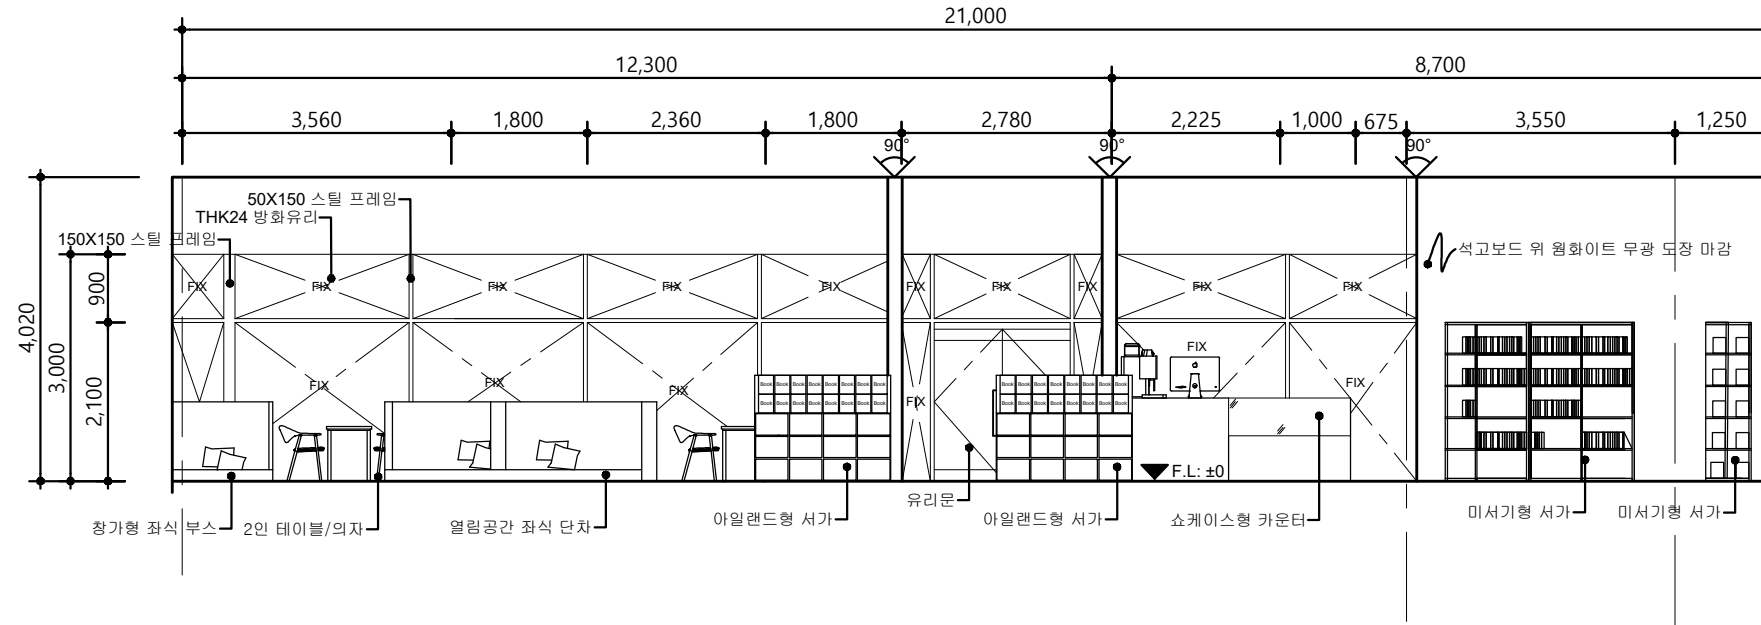

내부입면도-A

축척 1/100

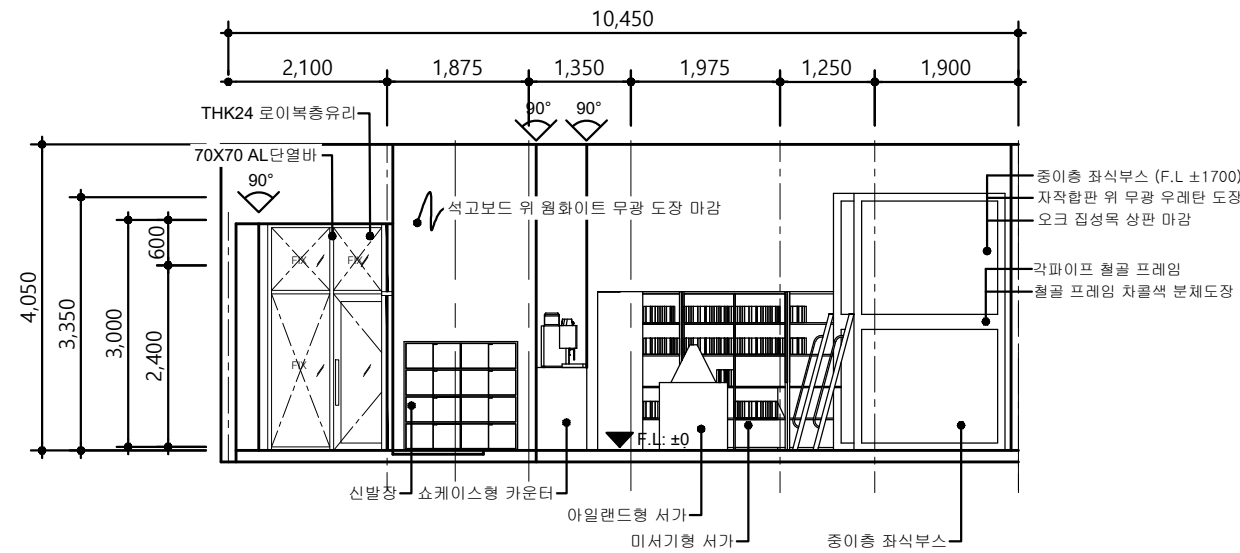

내부입면도-B

축척 1/100

특기사항
NOTE

수정사항
REVISION

번호 NO	일 자 DATE	수 정 DESCRIPTION	날 인 SIGN
△			
△			
△			
△			
△			
△			
△			
△			
△			

공사명
PROJECT TITLE

축척
SCALE

작성일
DATE

설계
DESIGNED BY

제도
DRAWN BY

검사
CHECKED BY

승인
APPROVED BY


도면명
NAME OF DRAWING

도면번호
DRAWING NO

--	--	--	--	--	--


시공번호
PROJECT NO

TD					
----	--	--	--	--	--

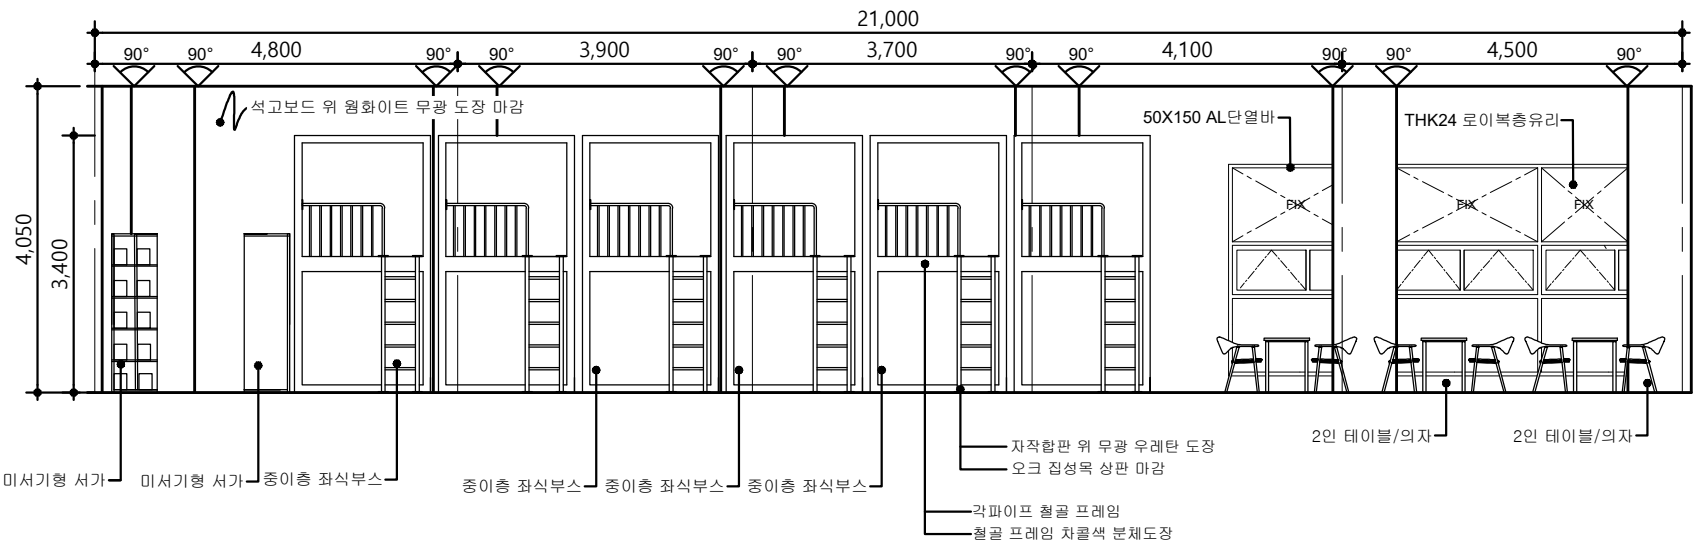

내부입면도-C

축척 1/100

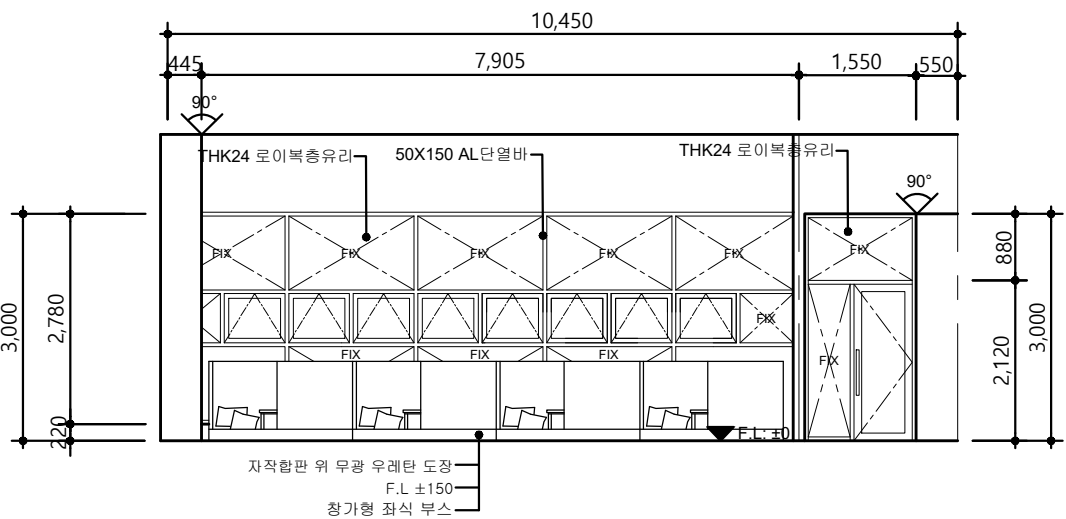

내부입면도-D

축척 1/100

특기사항
NOTE

수정사항
REVISION

번호 NO	일자 DATE	수정 DESCRIPTION	날인 SIGN
△			
△			
△			
△			
△			
△			
△			
△			
△			

공사명
PROJECT TITLE

축척
SCALE

작성일
DATE

설계
DESIGNED BY

제도
DRAWN BY

검사
CHECKED BY

승인
APPROVED BY


도면명
NAME OF DRAWING

도면번호
DRAWING NO

□ □ □ □ □ □

시공번호
PROJECT NO

TD □ □ □ □ □ □

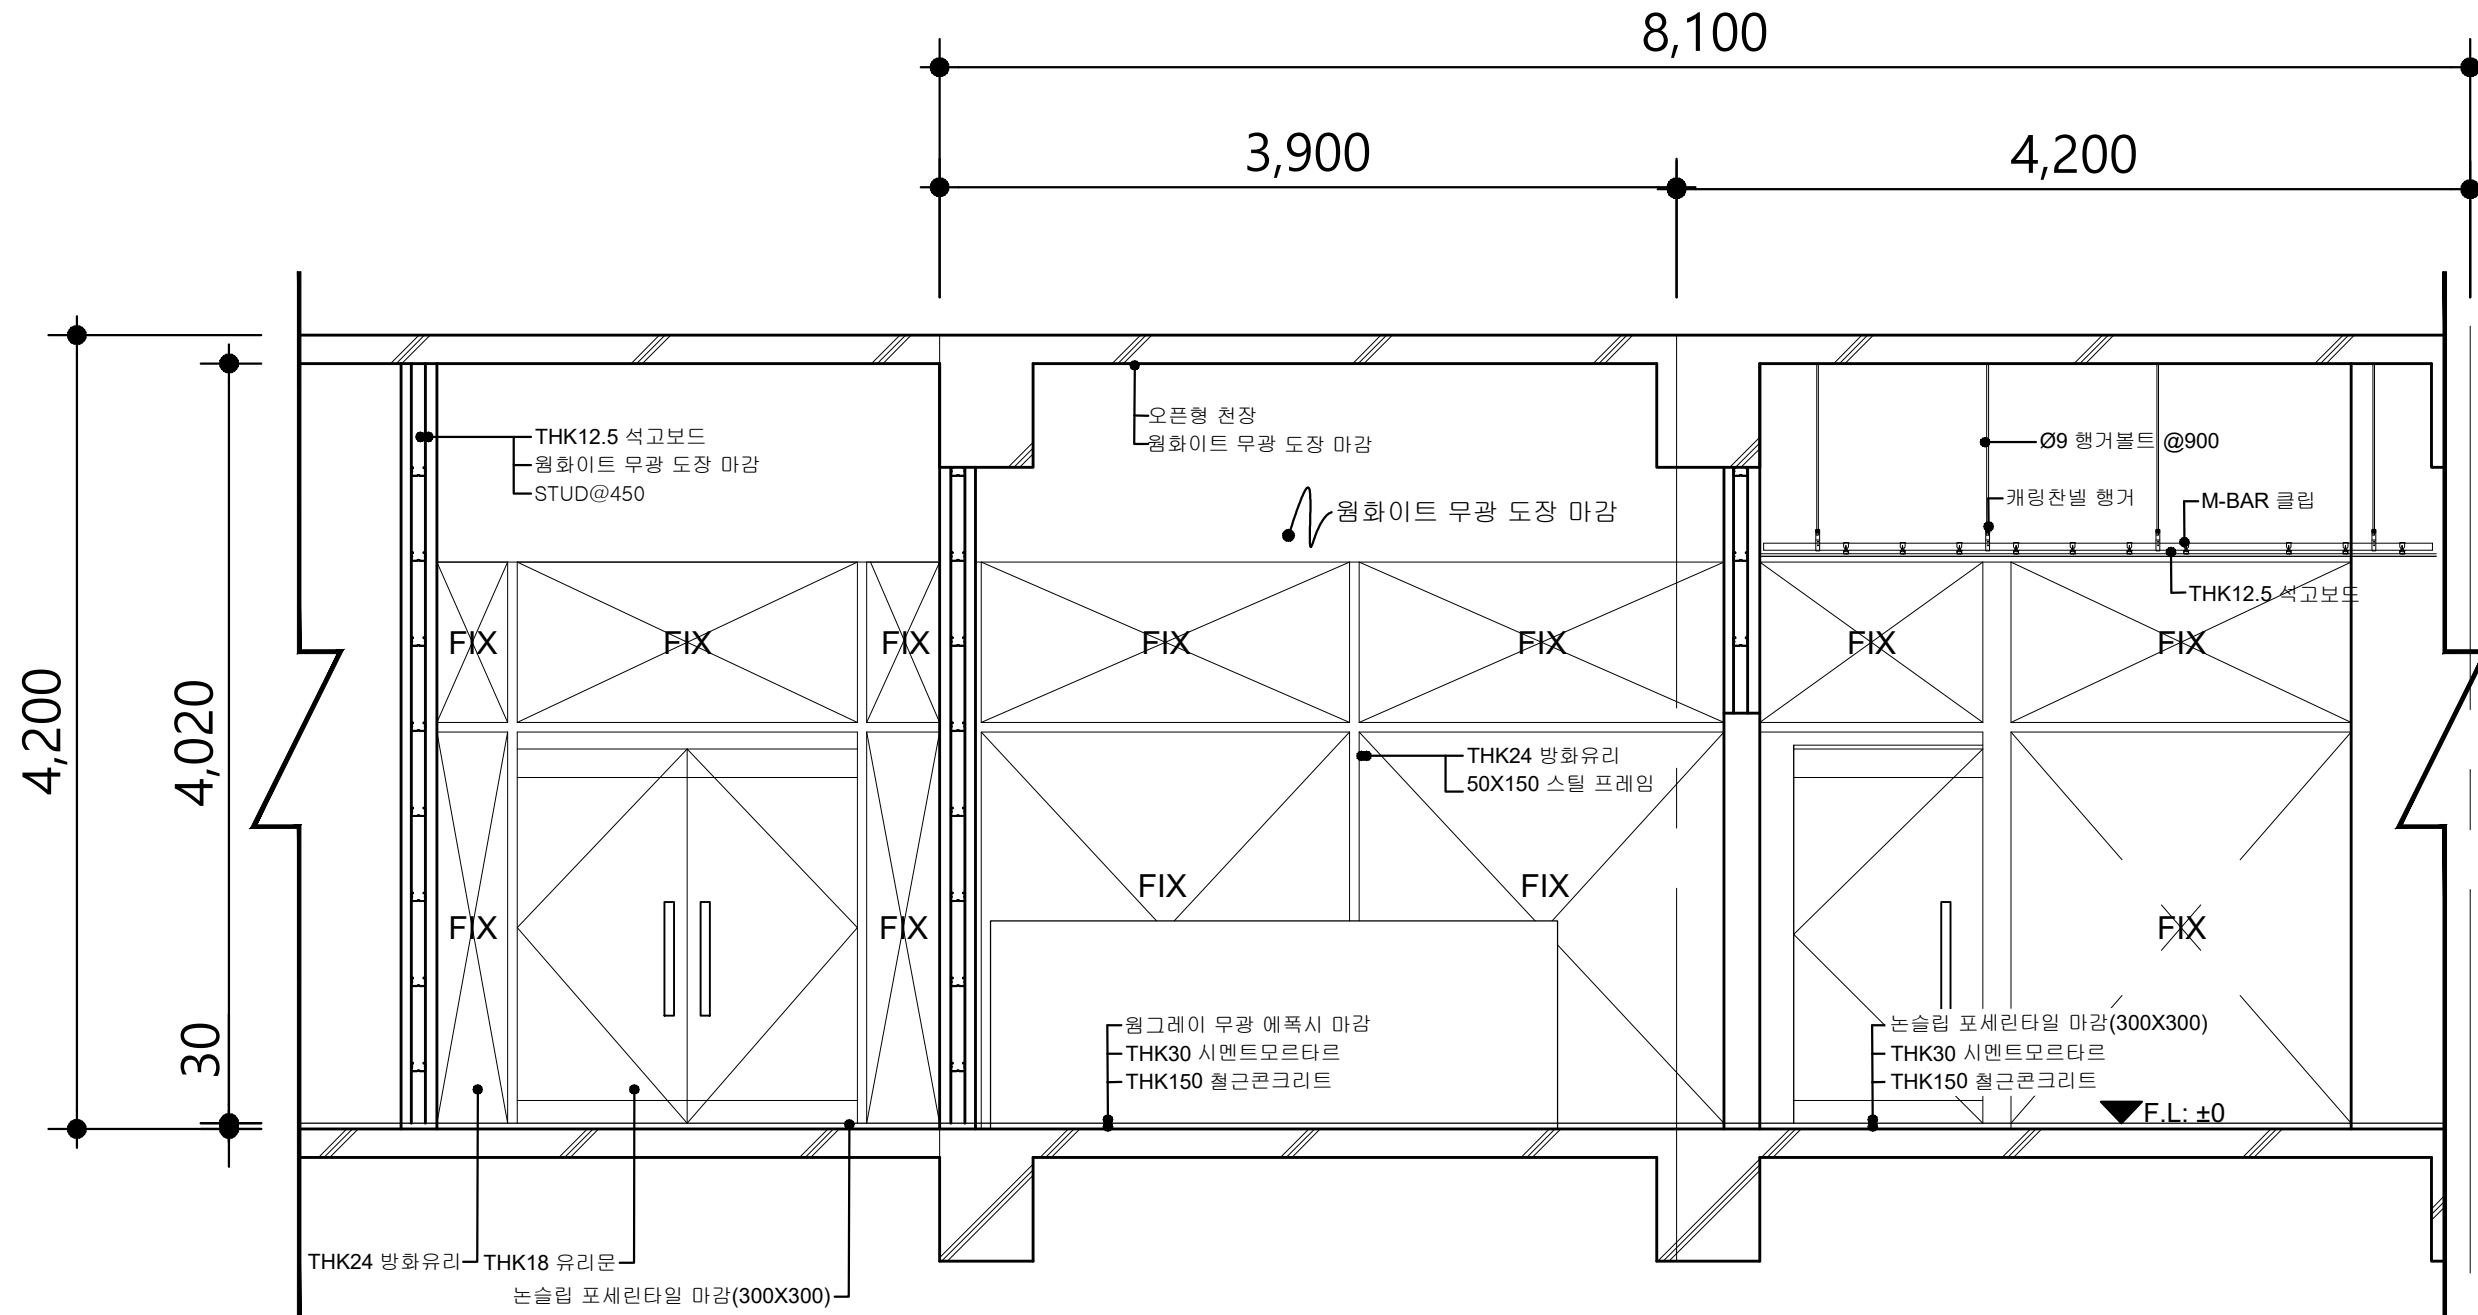

A' 부분 단면도

축척 1/40

특기사항
NOTE

수정사항
REVISION

번호 NO	일 자 DATE	수 정 DESCRIPTION	날 인 SIGN
△			
△			
△			
△			
△			
△			
△			
△			
△			

공사명
PROJECT TITLE

축 척
SCALE

작성일
DATE

설 계
DESIGNED BY

제 도
DRAWN BY

검 사
CHECKED BY

승 인
APPROVED BY


도면명
NAME OF DRAWING

도면번호
DRAWING NO

--	--	--	--	--	--



시공번호
PROJECT NO

TD					
----	--	--	--	--	--

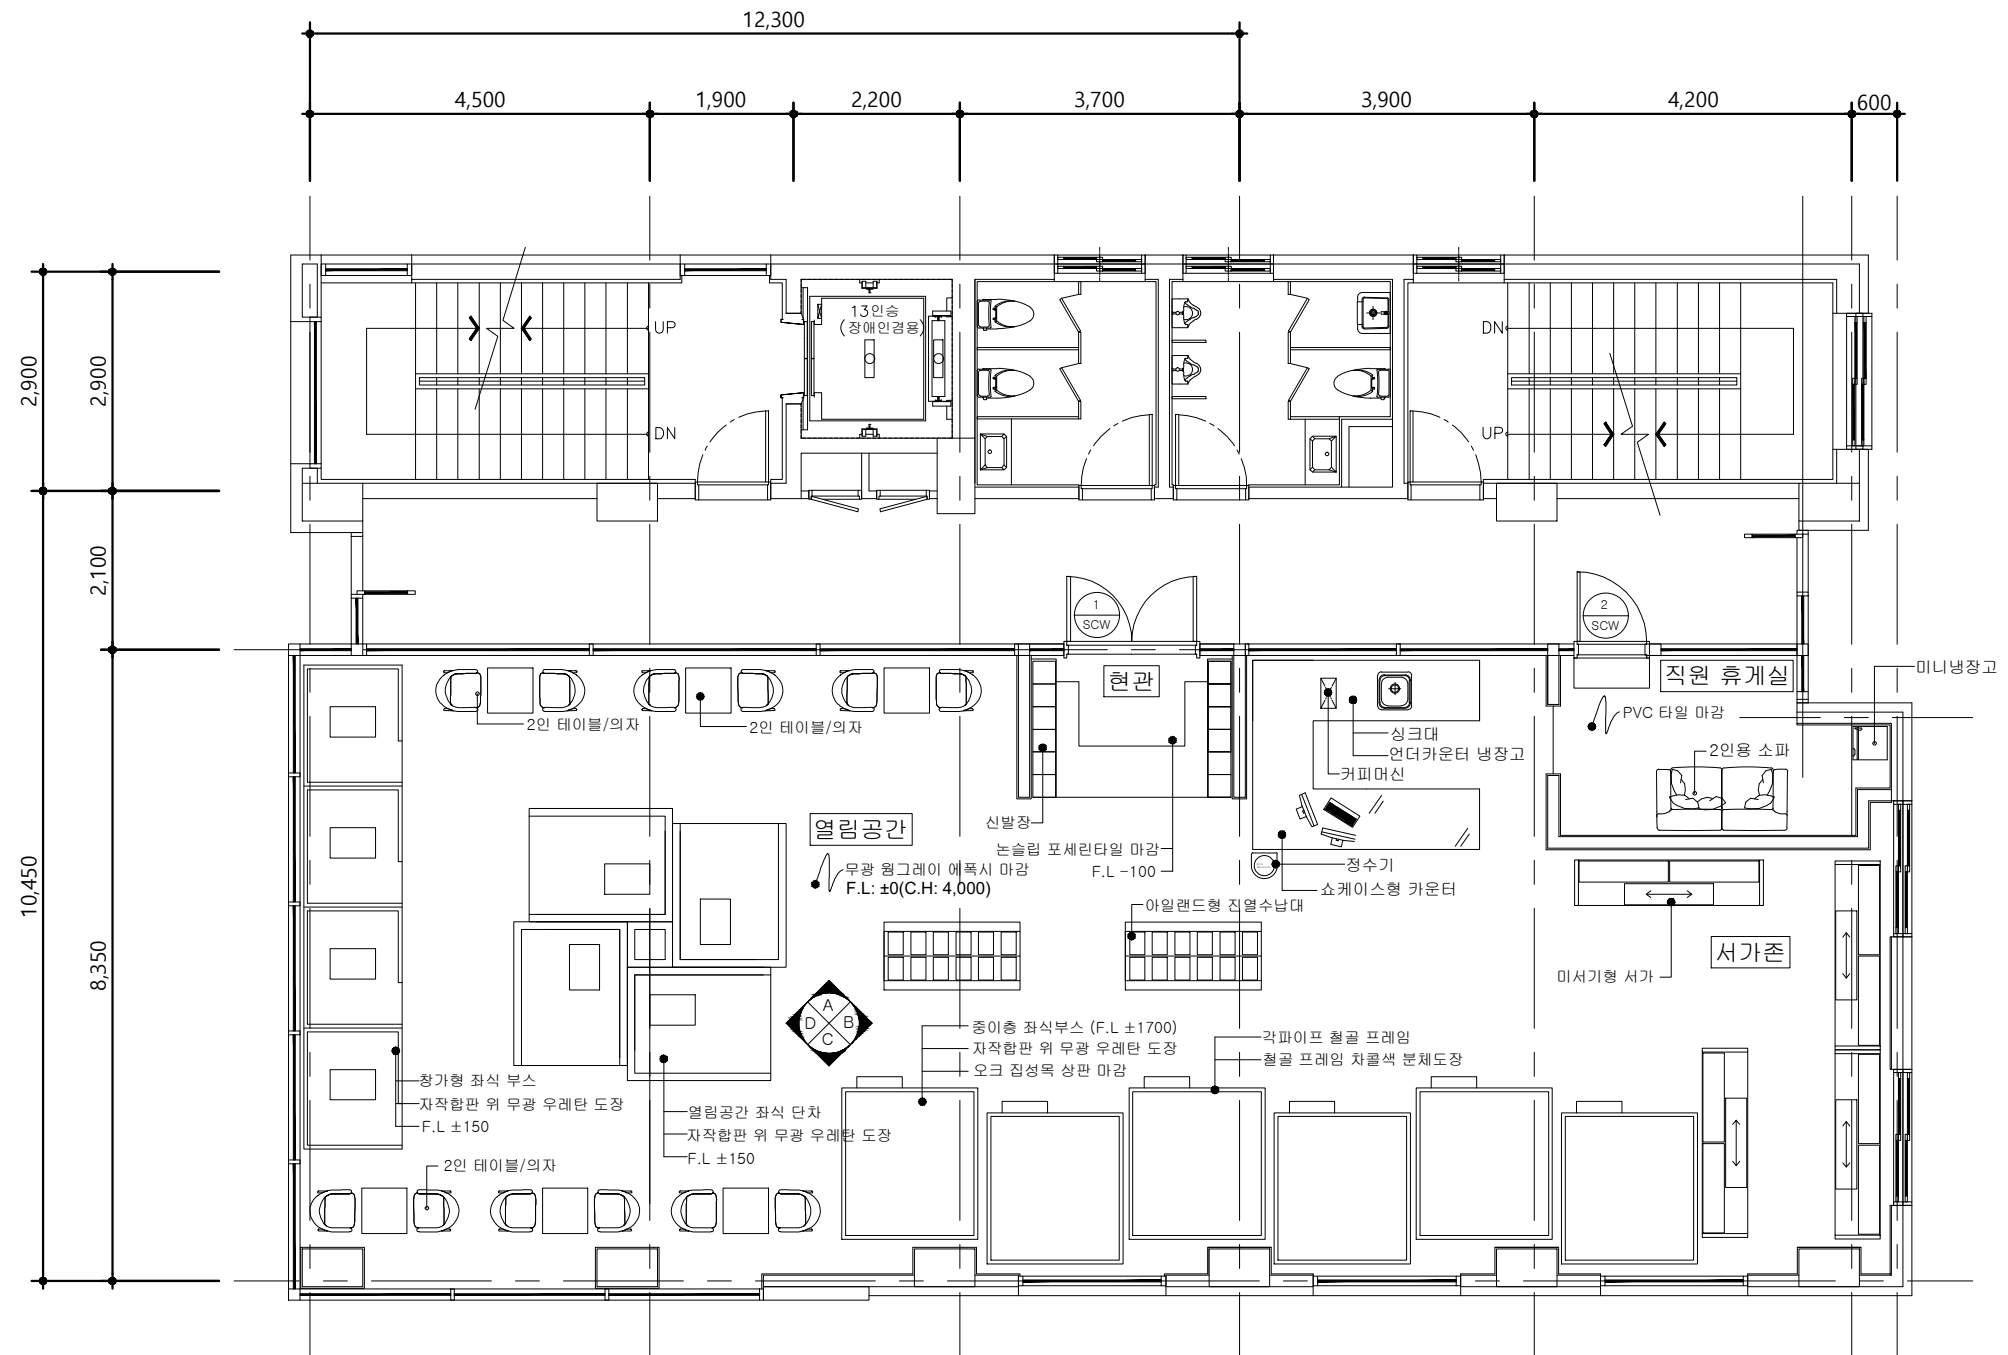

창호안내도

축척 1/100

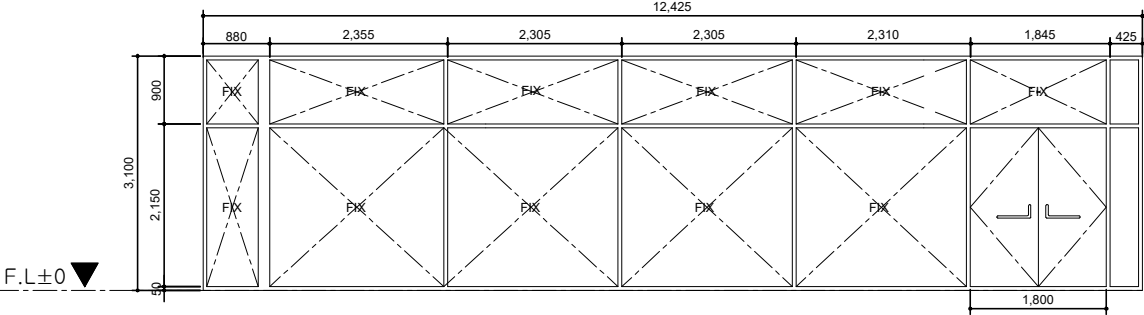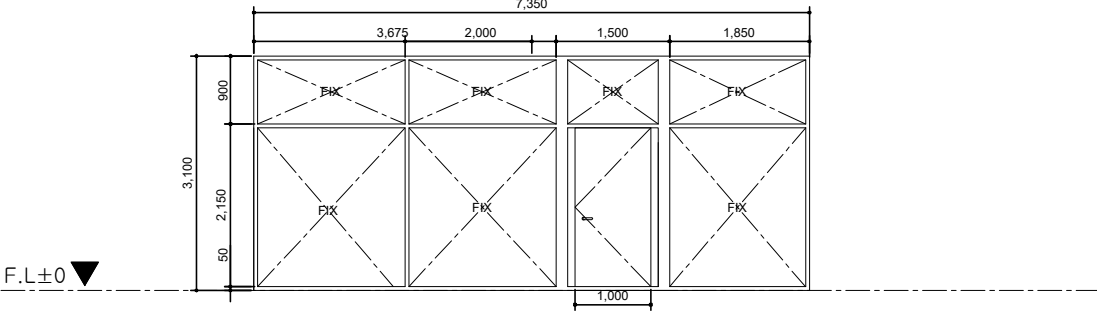영 태		
		
	창호제작처수(개구부치수)	12,425X3,100
	명 칭, 위 치	1 SCW / 스틸커튼월 출입구
	재 료	SCW 스틸 프레임/방화 유리
형 태	마 감	-
	부 속	점금장치 일체, 스토퍼
	창호제작처수(개구부치수)	
	명 칭, 위 치	
	재 료	
영 태	마 감	
	부 속	
	창호제작처수(개구부치수)	
	명 칭, 위 치	
	재 료	
형 태	마 감	
	부 속	
	창호제작처수(개구부치수)	
	명 칭, 위 치	
	재 료	

1

A 01

창호일람표

SCALE : N.S

EZDESIGN

이지디자인컴퓨터학원

(043)272-3550~1

특기사항

NOTE

수정사항

REVISION

번호 NO	일 자 DATE	수 정 DESCRIPTION	날 인 SIGN
△			
△			
△			
△			
△			
△			
△			
△			
△			

공사명

PROJECT TITLE

축 척

SCALE

작성일

DATE

설 계

DESIGNED BY

제 도

DRAWN BY

검 사

CHECKED BY

승 인

APPROVED BY

도면명

NAME OF DRAWING

분류번호

DRAWING NO

□□□□□□

사업번호

PROJECT NO

TD□□□□□□

형 태				
가구제작치수	1,300X1,600	3,600X3,600	1,800X900	1,300X1,600
명 칭, 위 치	창가형 착식 부스	창가 착식공간	열림공간	열림공간
재 료	자작합판, 목재 각재, 고밀도 폼	목재 각재, 합판	자작합판 또는 MDF	자작합판, 목재 각재, 고밀도 폼
마 감	오크 무늬목 또는 목재 시트, 무광 투명도장, 패브릭	카펫타일 또는 마루게 마감	다크오크 무늬목/목재 시트, 무광 마감	오크 무늬목 또는 목재 시트, 패브릭
부 속	좌방석, 등받이 쿠션, 고정철물	고정철물, 마감물딩	선반, 수납도어, 경첩, 손잡이	좌방석, 등받이 쿠션, 고정철물
형 태				
가구제작치수	2,500X600	2,500X3,000		
명 칭, 위 치	미서기형 서가	벽면 또는 서가공간	쇼케이스형 카운터	카운터 및 서비스공간
재 료	자작합판 또는 MDF, 금속 프레임	자작합판 또는 MDF, 강화유리		
마 감	다크오크 무늬목 또는 목재 시트, 분체도장	다크오크 무늬목 또는 목재 시트, 무광 마감		
부 속	슬라이딩 레일, 스토퍼, 손잡이, 고정철물	강화유리, 선반, 경첩, 손잡이, 조명		
형 태				
가구제작치수				
명 칭, 위 치				
재 료				
마 감				
부 속				

번호 NO	일 자 DATE	수 정 DESCRIPTION	날 인 SIGN
△			
△			
△			
△			
△			
△			
△			
△			
△			

특기사항
NOTE

수정사항
REVISION

번호 NO	일 자 DATE	수 정 DESCRIPTION	날 인 SIGN
△			
△			
△			
△			
△			
△			
△			
△			
△			

공사명
PROJECT TITLE

축 척
SCALE

작성일
DATE

설 계
DESIGNED BY

제 도
DRAWN BY

검 사
CHECKED BY

승 인
APPROVED BY


도면명
NAME OF DRAWING

도면번호
DRAWING NO

시공번호
PROJECT NO






TD

구분	실명	바닥				걸레받이				벽			천장			비고
		바탕	마감	두께	부호	바탕	마감	높이	부호	바탕	마감	부호	바탕	마감	부호	
3층	부스존	시멘트 모르타르	원그레이 무광 에폭시 마감	30		-	-	-		방화유리/강화유리/망입유리	-		시멘트 모르타르	원화이트 무광 페인트		
	열림공간	시멘트 모르타르	원그레이 무광 에폭시 마감	30		-	-	-		방화유리/강화유리/망입유리	-		시멘트 모르타르	원화이트 무광 페인트		
	현관	시멘트 모르타르	논슬립 포세린타일 마감	10		-	-	-		석고보드(12.5T)	원화이트 무광 페인트		시멘트 모르타르	원화이트 무광 페인트		
	카운터	시멘트 모르타르	원그레이 무광 에폭시 마감	30		-	-	-		방화유리/강화유리/망입유리	-		시멘트 모르타르	원화이트 무광 페인트		
	복층부스존	시멘트 모르타르	원그레이 무광 에폭시 마감	30		-	-	-		시멘트모르타르	원화이트 무광 페인트		시멘트 모르타르	원화이트 무광 페인트		
										방화유리/강화유리/망입유리	-					
	서가존	시멘트 모르타르	원그레이 무광 에폭시 마감	30		-	-	-		시멘트모르타르	원화이트 무광 페인트		시멘트 모르타르	원화이트 무광 페인트		
										방화유리/강화유리/망입유리	-					
	직원휴게실	시멘트 모르타르	오크 우드 플로어 마감	30		-	-	-		석고보드(12.5T)	원화이트 무광 페인트		석고보드(12.5T)	원화이트 무광 페인트		
										방화유리/강화유리/망입유리	-					

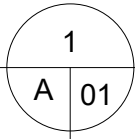

실내재료 마감표

SCALE : N.S

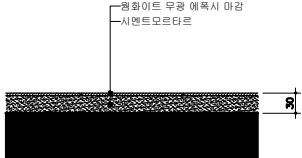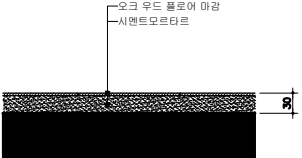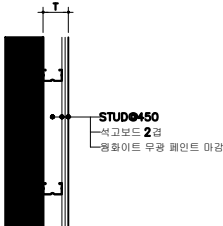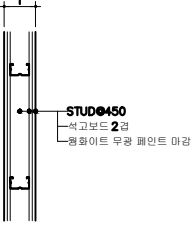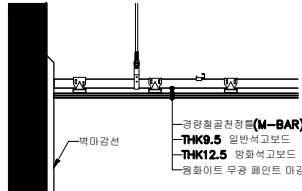바닥				
부호	F01 열림공간, 카운터, 복층부스존, 서가존	F02 직원휴게실	F03 현관	-
단면				
부호	W01 열림공간, 카운터, 복층부스존, 서가존	W02 현관, 직원휴게실	-	-
단면				
부호	C01 직원휴게실	C01 열림공간, 카운터, 복층부스존, 서가존, 현관	-	-
단면				
부호	-	-	-	-

특기사항
NOTE

수정사항
REVISION

번호 NO	일자 DATE	수정 DESCRIPTION	날인 SIGN
△			
△			
△			
△			
△			
△			
△			
△			
△			

공사명
PROJECT TITLE

축척
SCALE

작성일
DATE

설계
DESIGNED BY

제도
DRAWN BY

검사
CHECKED BY

승인
APPROVED BY


도면명
NAME OF DRAWING

도면번호
DRAWING NO

□□□□□□

시공번호
PROJECT NO

TD□□□□□□

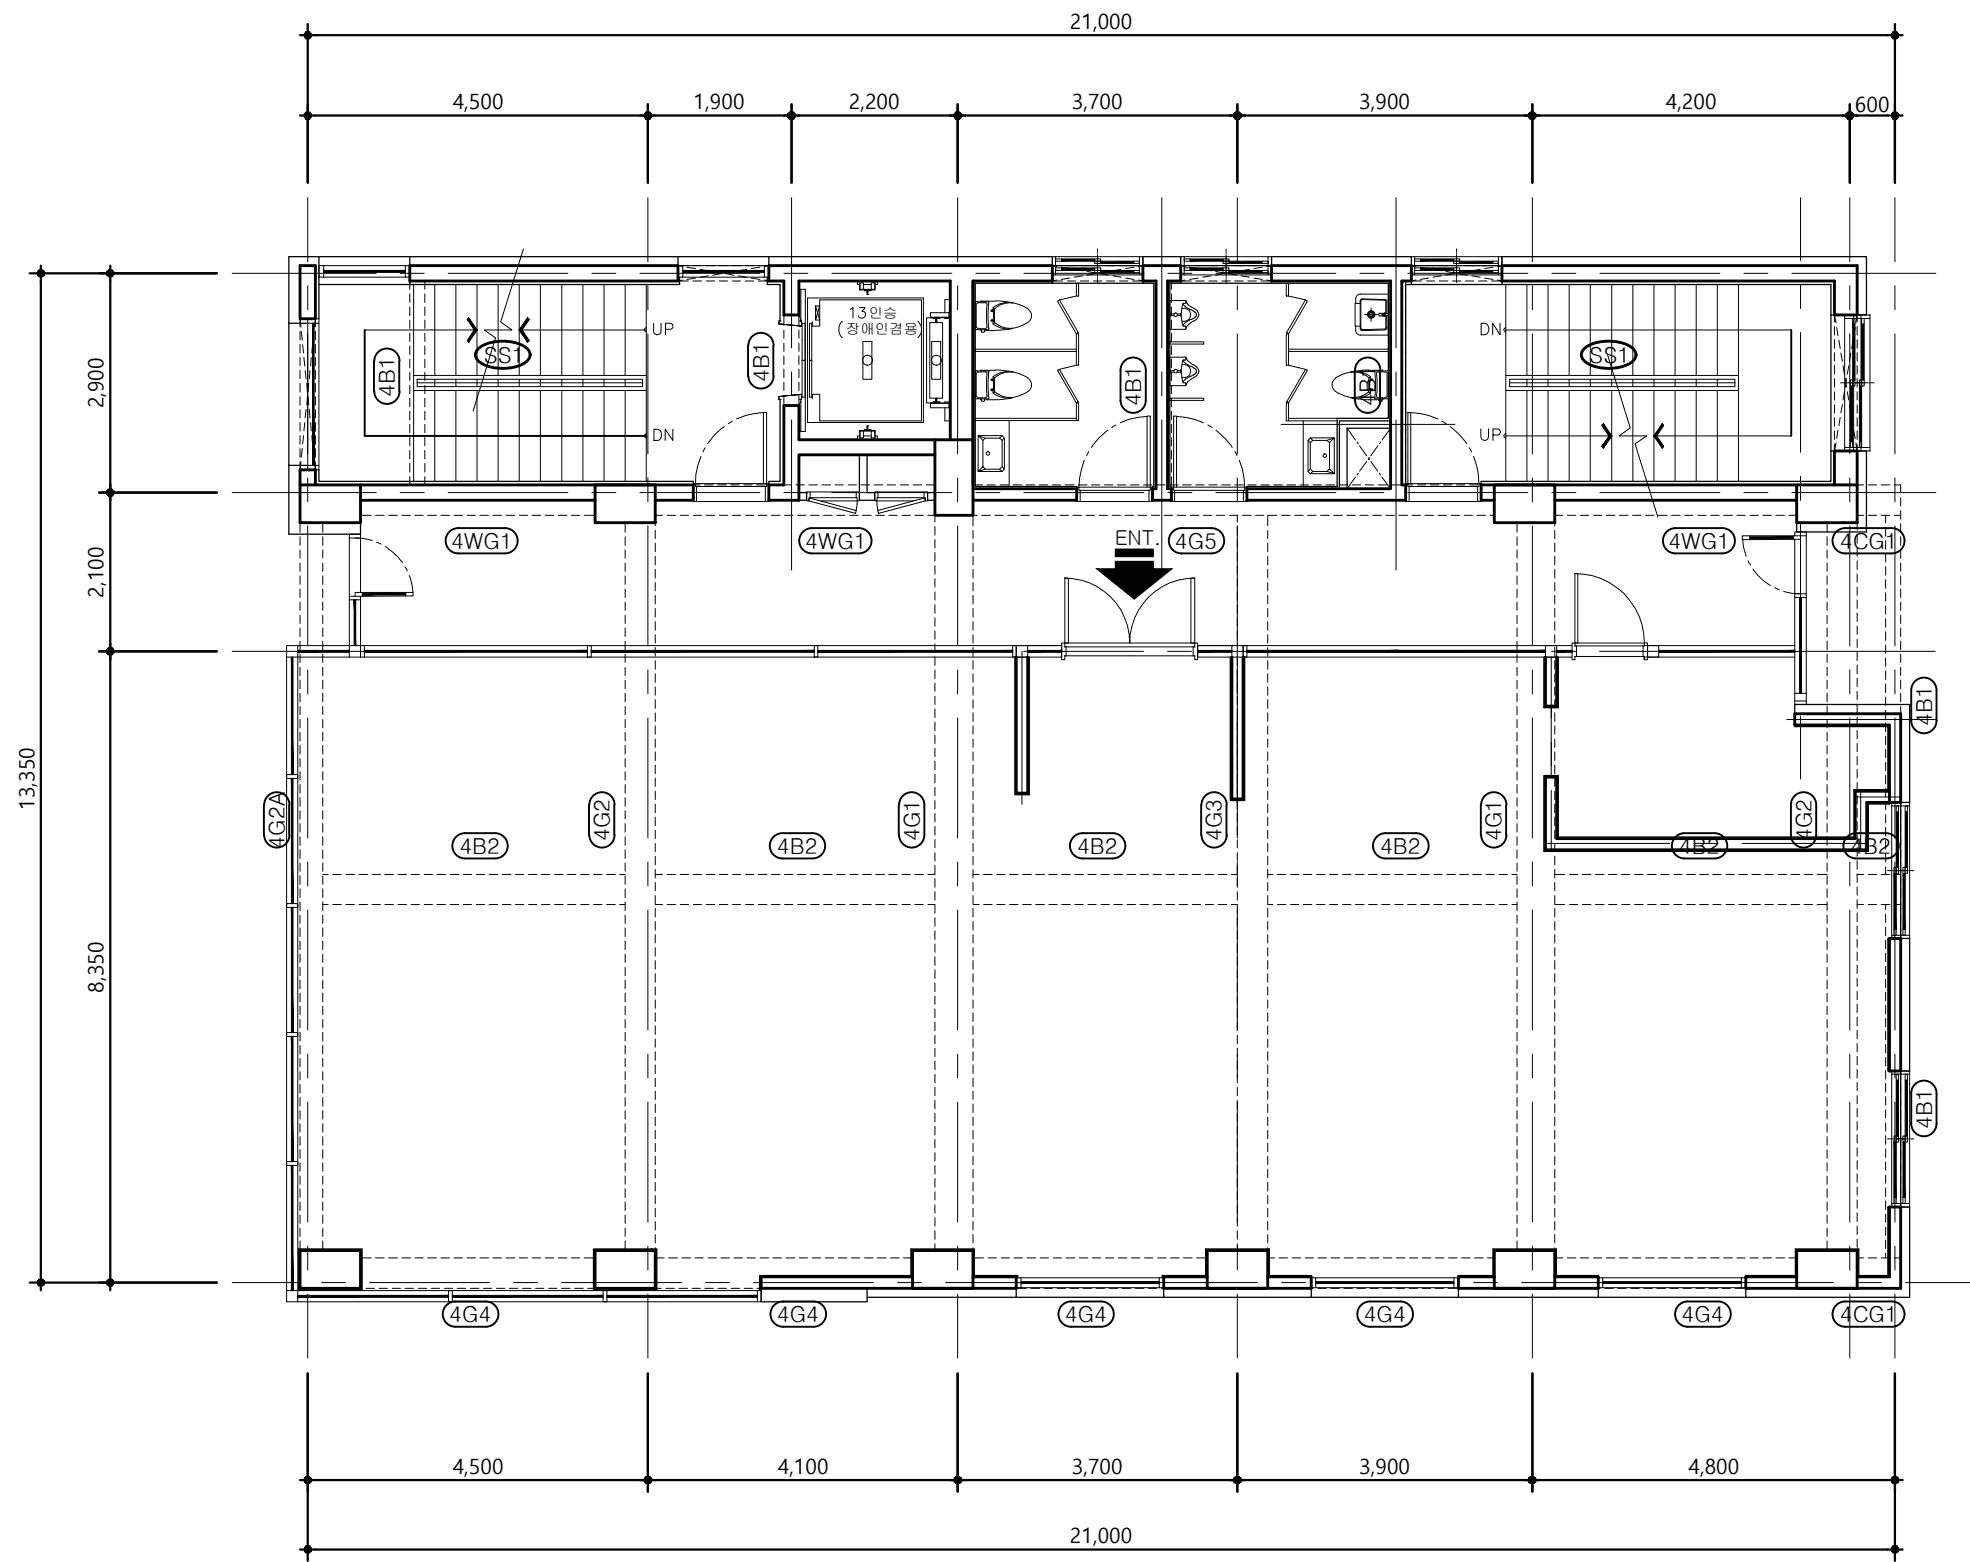

구조부재위치도

축척 1/100

특기사항
NOTE

수정사항
REVISION

번호 NO	일 자 DATE	수 정 DESCRIPTION	날 인 SIGN
△			
△			
△			
△			
△			
△			
△			
△			
△			

공사명
PROJECT TITLE

축 척
SCALE

작성일
DATE

설 계
DESIGNED BY

제 도
DRAWN BY

검 사
CHECKED BY

승 인
APPROVED BY

도면명
NAME OF DRAWING

도면번호
DRAWING NO

□□□□□□

시공번호
PROJECT NO

TD□□□□□□



보 일 랑 표 - 1

축 척:

1/40

EZDESIGN
이지디자인컴퓨터학원

(043)272-3550~1

특기사항

NOTE

수정사항

REVISION

번호 NO	일 자 DATE	수 정 DESCRIPTION	날 인 SIGN
△			
△			
△			
△			
△			
△			
△			

공사명

PROJECT TITLE

축 척

SCALE

작성일

DATE

설 계

DESIGNED BY

제 도

DRAWN BY

검 사

CHECKED BY

승 인

APPROVED BY

도면명

NAME OF DRAWING

도면번호


DRAWING NO

시공번호

PROJECT NO

TD-□□□□□□

부 호	5~2G1	5~2G2	6~2G2A	5~2G3
형 태				
구 분	BOTH.END	BOTH.END	BOTH.END	INT.END
상 부근	10-HD22	8-HD22	5-HD22	8-HD22
하 부근	4-HD22	4-HD22	3-HD22	4-HD22
느 근	HD10@150	HD10@150	HD10@200	HD10@150
부 호	6~2G4	5~2G5	6~3CG1	6~2WG1
형 태				
구 분	ALL	BOTH.END	ALL	ALL
상 부근	4-HD22	8-HD22	4-HD22	3-HD22
하 부근	4-HD22	4-HD22	4-HD22	3-HD22
느 근	HD10@150	HD10@150	HD10@100	HD10@300
부 호	PHR~1B1	6~2B2		
형 태				
구 분				
상 부근				
하 부근				
느 근				
부 호				
형 태				
구 분				
상 부근				
하 부근				
느 근				

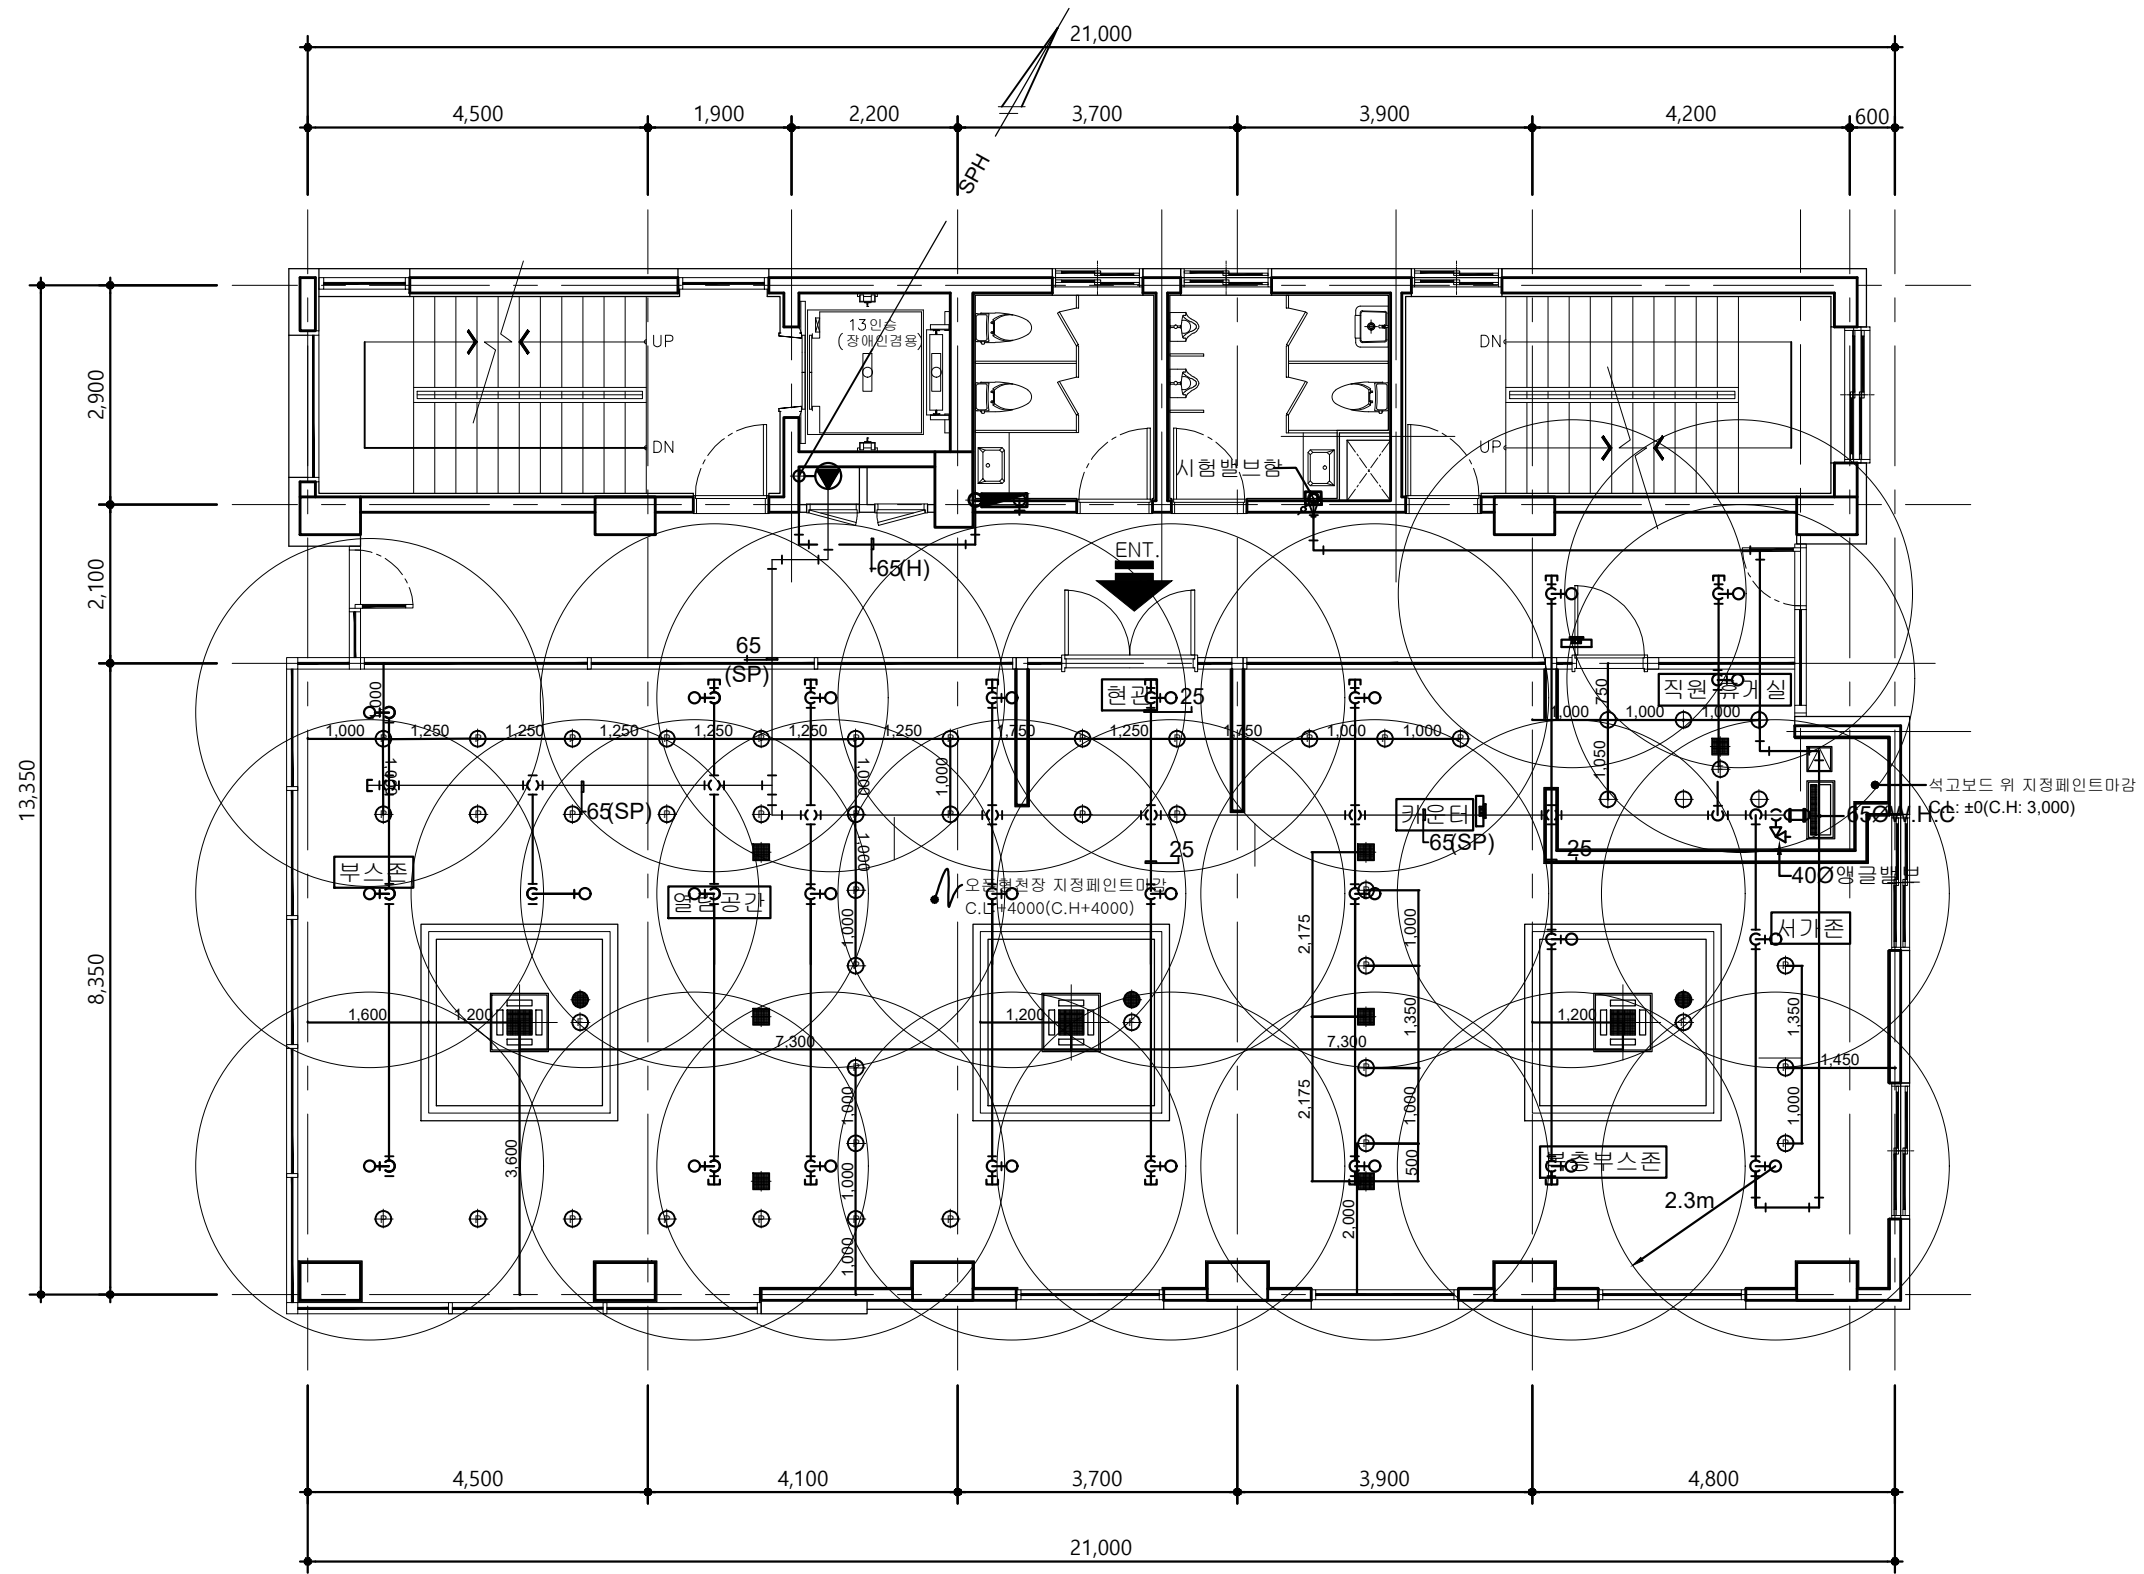

소 방 (기존) 축척 1/100

특기사항
NOTE

수정사항
REVISION

번호 NO	일 자 DATE	수 정 DESCRIPTION	날 인 SIGN
△			
△			
△			
△			
△			
△			
△			
△			
△			

공사명
PROJECT TITLE

축 척
SCALE

작성일
DATE

설 계
DESIGNED BY

제 도
DRAWN BY

검 사
CHECKED BY

승 인
APPROVED BY

도면명
NAME OF DRAWING

도면번호
DRAWING NO

□□□□□□

시공번호
PROJECT NO

TD□□□□□□