

특기사항
NOTE

수정사항
REVISION

번호 NO	일 자 DATE	수 정 DESCRIPTION	날 인 SIGN
△			
△			
△			
△			
△			
△			
△			
△			
△			

공사명
PROJECT TITLE

축 력
SCALE

작성일
DATE

설 계
DESIGNED BY

제 도
DRAWN BY

검 사
CHECKED BY

승 인
APPROVED BY




도면명
NAME OF DRAWING

도면번호
DRAWING NO

□ □ □ □ □ □

사업번호
PROJECT NO

TD □ □ □ □ □ □

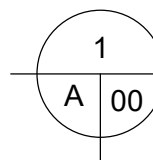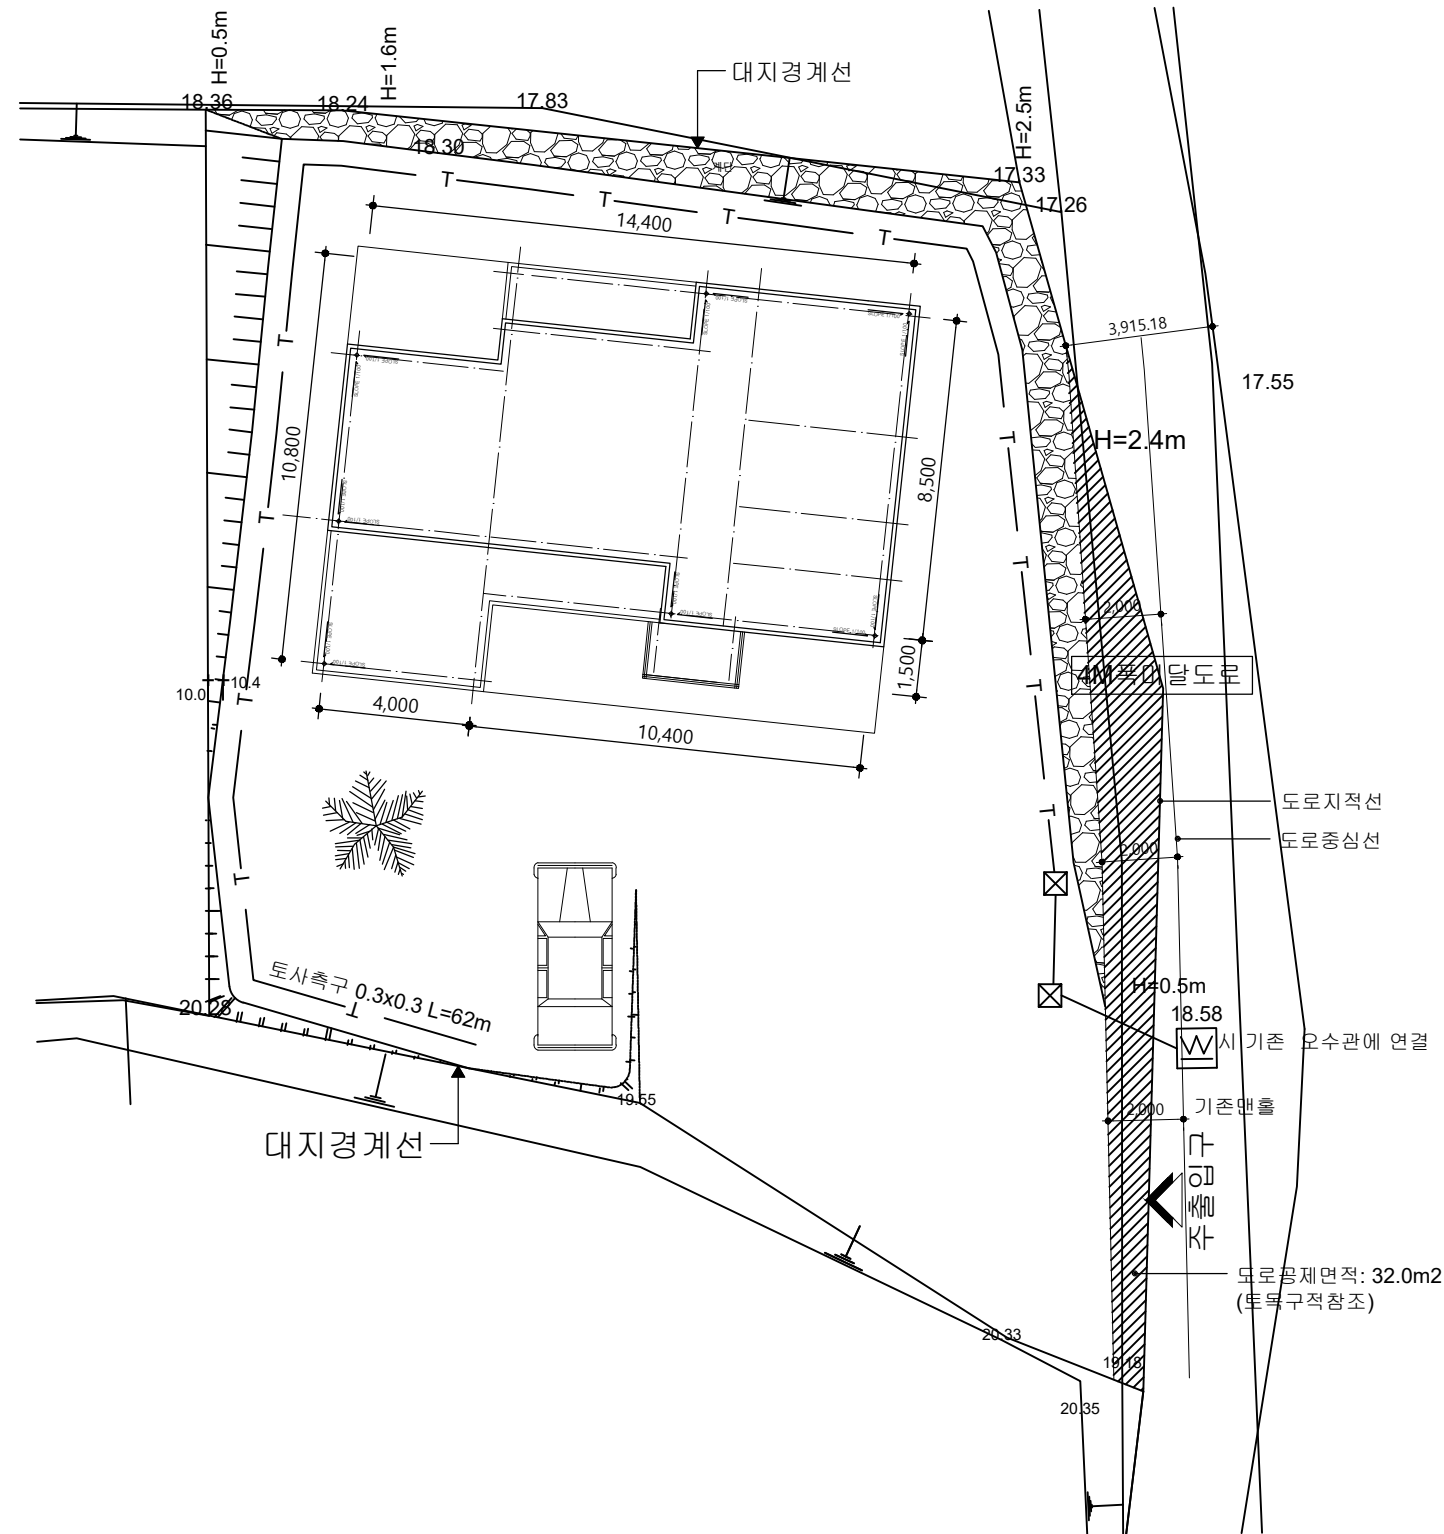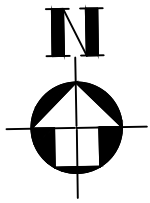

배 치 도
SCALE : 1/200

특기사항
NOTE

수정사항
REVISION

번호 NO	일 자 DATE	수 정 DESCRIPTION	날 인 SIGN
△			
△			
△			
△			
△			
△			
△			
△			
△			

공사명
PROJECT TITLE

축 치
SCALE

작성일
DATE

설 계
DESIGNED BY

제 도
DRAWN BY

검 사
CHECKED BY

승 인
APPROVED BY




도면명
NAME OF DRAWING

도면번호
DRAWING NO

--	--	--	--	--	--

시공번호
PROJECT NO

TD					
----	--	--	--	--	--

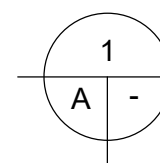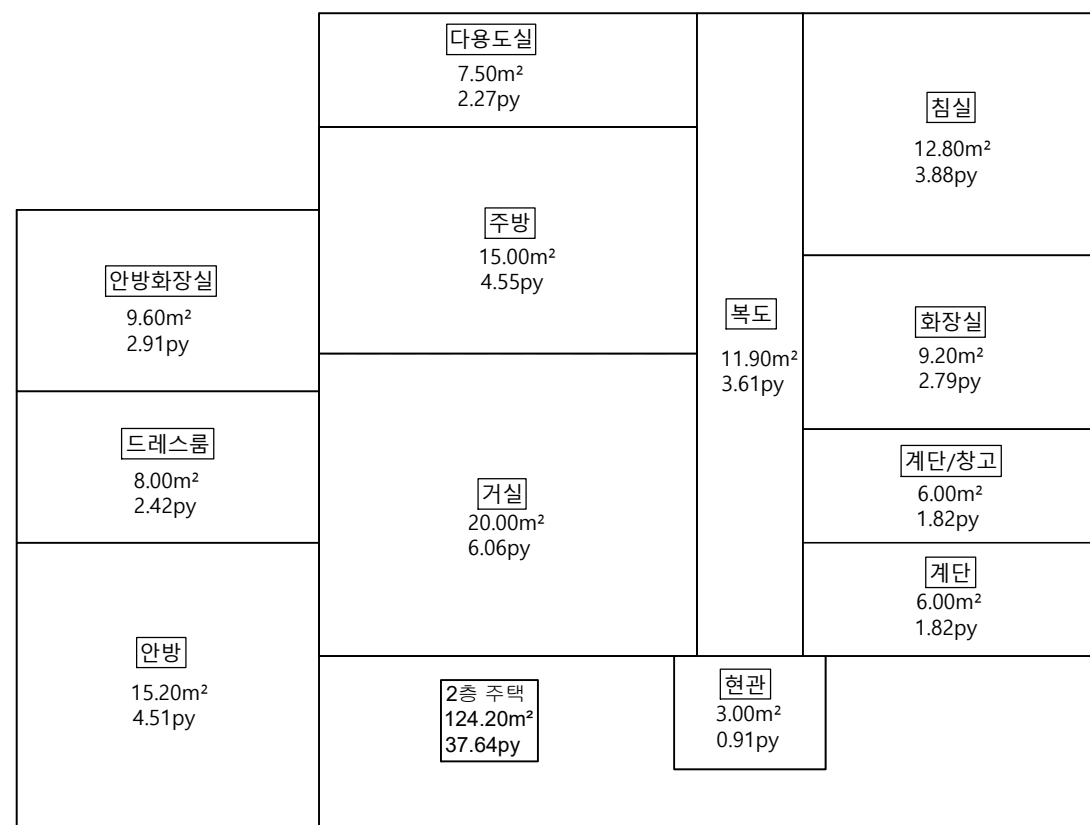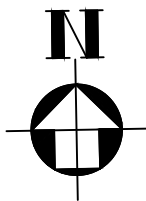

면적구획(실구획도)

SCALE : 1/100

특기사항

NOTE

수정사항

REVISION

번호 NO	일 자 DATE	수 정 DESCRIPTION	날 인 SIGN
△			
△			
△			
△			
△			
△			
△			
△			
△			

공사명

PROJECT TITLE

축 령

SCALE

작성일

DATE

설 계

DESIGNED BY

제 도

DRAWN BY

검 사

CHECKED BY

승 인

APPROVED BY

도면명

NAME OF DRAWING

도면번호

DRAWING NO

--	--	--	--	--	--

사업번호


PROJECT NO

TD					
----	--	--	--	--	--


설 계 개 요

설 계 명	강원도 동해시 초구동 282-1번지 단독주택 신축공사		
지 역, 지 구	도시지역, 자연녹지지역, 도시계획구역		
지 목	전		
대 지 위 치	동해시 초구동 282-1 번지		
대 지 면 적	공부상 면적	282-1 번지	660.0 M2
	도로후퇴면적	토목구적에의함	32.0 M2
	실사용 면적		628.0 M2
공 사 종 별	신 축		
도 로 현 황	폭 4M 도로에 31.6M 접함		
건물최고높이	7.60 M		
바 닥 면 적		바 닥 면 적	
	1 층	124.2 M2	
	2 층	121.2 M2	
	합 계	245.4 M2	
	용 도	단독주택	
	소유자		
수평 투영 면적	124.2		M2
건 축 면 적	124.2		M2
연 면 적	245.4		M2
용적율산정시 연 면 적	124.2(1층) + 121.2(2층) = 245.4		M2
건 폐 율	124.2 / 660.00 X 100 = 18.82 %		
용 적 율	245.4/ 660.00 X 100 = 37.18 %		
규 모	신축 :지상 2층		
구 조	기둥 및 벽체: 철근콘크리트, 지붕: 철근콘크리트		
오수정화설비	10인용 정화조		
조 경 면 적	해당없음		
주차대수 산정	1대		
비 고			

면 적 산 출

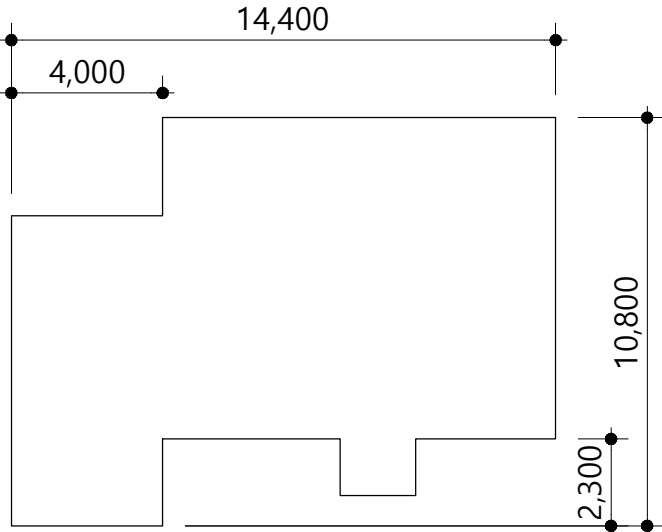

1층 124.20m²

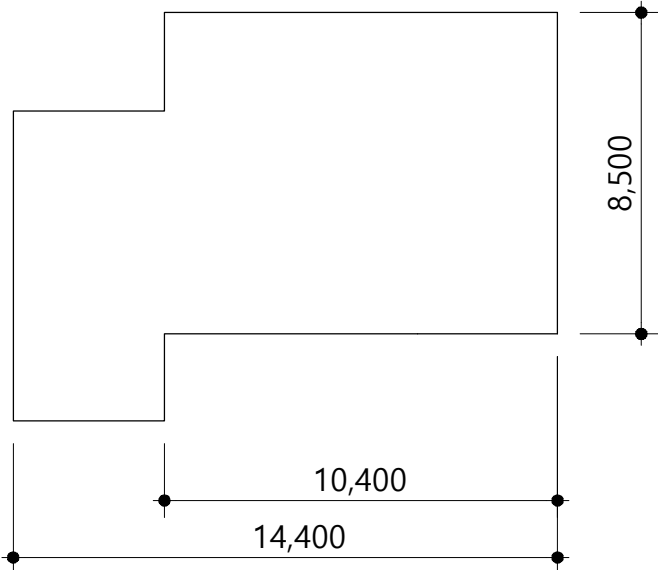

2층 121.20m²

총 합계 : 1층+2층 = 245.4m²

특기사항

NOTE

수정사항

REVISION

번호 NO	일 자 DATE	수 정 DESCRIPTION	날 인 SIGN
△			
△			
△			
△			
△			
△			
△			
△			
△			
△			

공사명
PROJECT TITLE

축척

SCALE

작성일

DATE

설계

DESIGNED BY

제도

DRAWN BY

검사

CHECKED BY

승인

APPROVED BY

도면명

NAME OF DRAWING

도면번호


DRAWING NO

사업번호

PROJECT NO

TD


구분	실명	바닥				걸레받이				벽			천장			비고
		바탕	마감	두께	부호	바탕	마감	높이	부호	바탕	마감	부호	바탕	마감	부호	
1층	거실	시멘트 모르타르	고급강마루	40		우드	지정 페인트	80		시멘트모르타르	지정 실크벽지		미장합판	지정 천장지 마감		
	안방	시멘트 모르타르	고급강마루	40		우드	지정 페인트	80		시멘트모르타르	지정 실크벽지		미장합판	지정 천장지 마감		
	주방	시멘트 모르타르	고급강마루	40		우드	지정 페인트	80		시멘트모르타르	지정 실크벽지		미장합판	지정 천장지 마감		
	침실	시멘트 모르타르	고급강마루	40		우드	지정 페인트	80		시멘트모르타르	지정 실크벽지		미장합판	지정 천장지 마감		
	계단 밑 창고	시멘트 모르타르	고급강마루	40		우드	지정 페인트	80		시멘트모르타르	지정 실크벽지		미장합판	지정 천장지 마감		
	화장실	시멘트 모르타르(액체방수)	포세린타일(300X300)	80		-	-	-		시멘트 모르타르(액체방수)	포세린타일(300X300)		욕실 SMC 천장	지정색상		
	안방화장실	시멘트 모르타르(액체방수)	포세린타일(300X300)	80		-	-	-		시멘트 모르타르(액체방수)	포세린타일(300X300)		욕실 SMC 천장	지정색상		
	다용도실	시멘트 모르타르	자기질타일(300X300)	80		-	-	-		시멘트모르타르	자기질타일(300X300)		미장합판	지정 천장지 마감		
	드레스룸	시멘트 모르타르	고급강마루	40		우드	지정 페인트	80		시멘트모르타르	지정 실크벽지		미장합판	지정 천장지 마감		
	현관	시멘트 모르타르	자기질타일(300X300)	80		우드	지정 페인트	80		시멘트모르타르	지정 실크벽지		미장합판	지정 천장지 마감		
2층	가족실	시멘트 모르타르	고급비닐시트	40		우드	지정 페인트	80		시멘트모르타르	지정 실크벽지		미장합판	지정 천장지 마감		
	취미실	시멘트 모르타르	고급강마루	40		우드	지정 페인트	80		시멘트모르타르	지정 실크벽지		미장합판	지정 천장지 마감		
	게스트룸	시멘트 모르타르	고급강마루	40		우드	지정 페인트	80		시멘트모르타르	지정 실크벽지		미장합판	지정 천장지 마감		
	화장실	시멘트 모르타르(액체방수)	포세린타일(300X300)	80		-	-	-		시멘트 모르타르(액체방수)	포세린타일(300X300)		욕실 SMC 천장	지정색상		

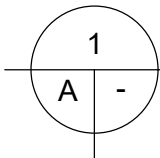

실내재료 마감표

SCALE : N.S

바 닥								
부 호	F01	1층 테라스	F02	옥상(ROOF), 발코니(베란다)	F03	1층 거실, 1/2층 방1/2, 안방(드레스룸), 1/2층 복도	F04	2층 거실
바 닥								
부 호	F05	1층 화장실, 2층 화장실, 안방 화장실	F06	현관, 다용도실	F07		F08	
걸레받이								
부 호	B01							
표								
부 호	W01	1/2층 거실, 1/2층 방1/2, 다용도실 안방(드레스룸), 1/2층 복도, 현관	W02	1층 화장실, 2층 화장실, 안방 화장실	W03	외벽		

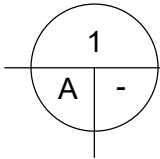

마감상세도-1

SCALE : N.S

특기사항

NOTE

수정사항

REVISION

번호 NO	일 자 DATE	수 정 DESCRIPTION	날 인 SIGN
△			
△			
△			
△			
△			
△			
△			
△			
△			

공사명

PROJECT TITLE

축 치

SCALE

작성일

DATE

설 계

DESIGNED BY

제 도

DRAWN BY

검 사

CHECKED BY

승 인

APPROVED BY

도면명

NAME OF DRAWING

도면번호

DRAWING NO

--	--	--	--	--	--

사업번호

PROJECT NO

TD					
----	--	--	--	--	--

특기사항
NOTE

수정사항
REVISION

번호 NO	일 자 DATE	수 정 DESCRIPTION	날 인 SIGN
△			
△			
△			
△			
△			
△			
△			
△			
△			

공사명
PROJECT TITLE

축 치
SCALE

작성일
DATE

설 계
DESIGNED BY

제 도
DRAWN BY

검 사
CHECKED BY

승 인
APPROVED BY



도면명
NAME OF DRAWING


도면번호
DRAWING NO

--	--	--	--	--	--

시공번호
PROJECT NO


TD					
----	--	--	--	--	--

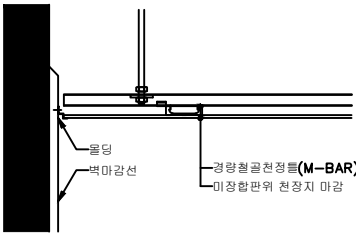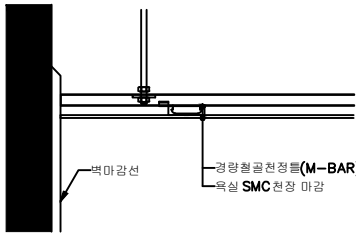바 닥				
부 호	C01	1/2층 거실, 1/2층 방1/2, 다용도실, 현관 안방(드레스룸), 1/2층 복도	C02	1층 화장실, 2층 화장실, 안방 화장실
바 닥				
부 호				
결레받이				
부 호				
표				
부 호				

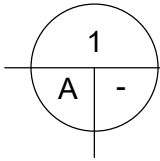




마감상세도-2

SCALE : N.S

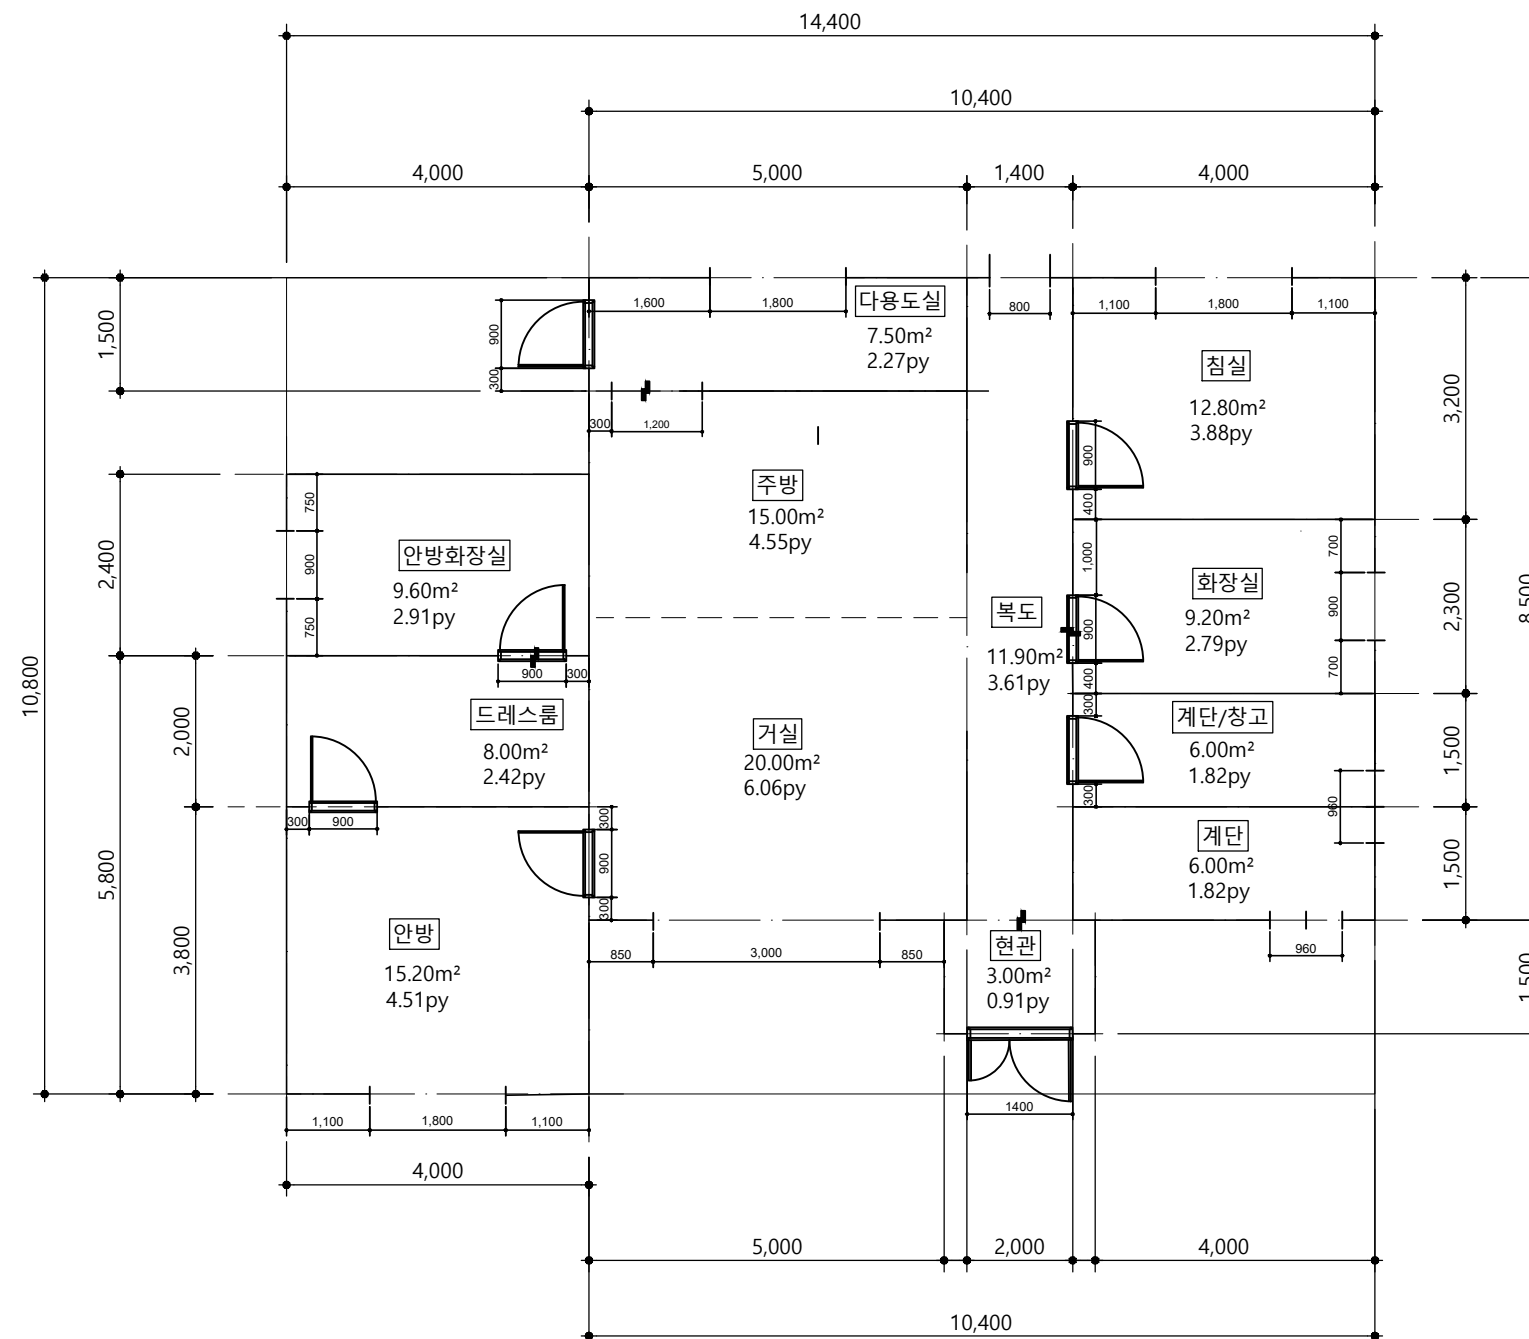

특기사항
NOTE수정사항
REVISION

번호 NO	일 자 DATE	수 정 DESCRIPTION	날 인 SIGN
△			
△			
△			
△			
△			
△			
△			
△			
△			

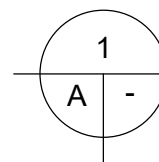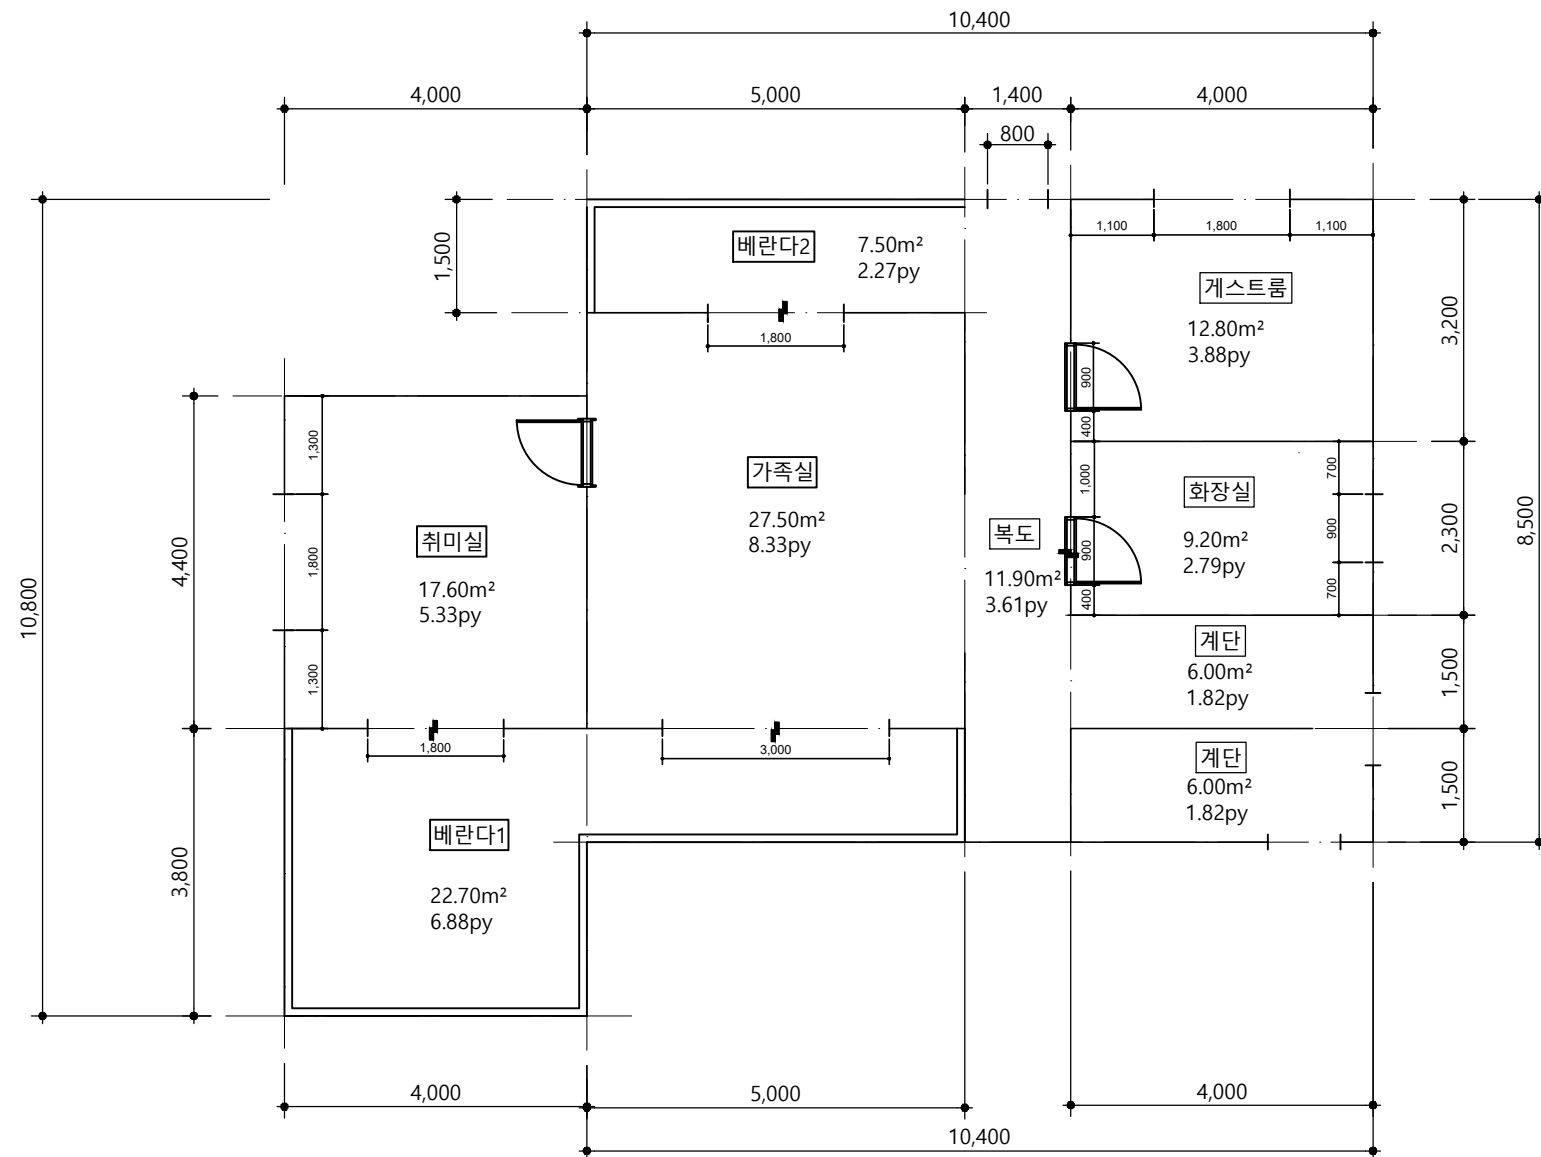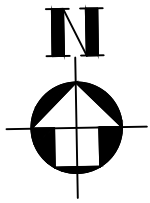공사명
PROJECT TITLE축 치
SCALE작성일
DATE설 계
DESIGNED BY제 도
DRAWN BY검 사
CHECKED BY승 인
APPROVED BY도면명
NAME OF DRAWING도면번호
DRAWING NO시공번호
PROJECT NOTD

2층 평면도 (계획안)

SCALE : 1/100

특기사항
NOTE

수정사항
REVISION

번호 NO	일 자 DATE	수 정 DESCRIPTION	날 인 SIGN
△			
△			
△			
△			
△			
△			
△			
△			
△			

공사명
PROJECT TITLE

축 치
SCALE

작성일
DATE

설 계
DESIGNED BY

제 도
DRAWN BY

검 사
CHECKED BY

승 인
APPROVED BY




도면명
NAME OF DRAWING

도면번호
DRAWING NO

□ □ □ □ □ □

시공번호
PROJECT NO

TD □ □ □ □ □ □

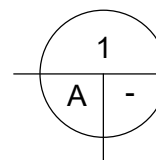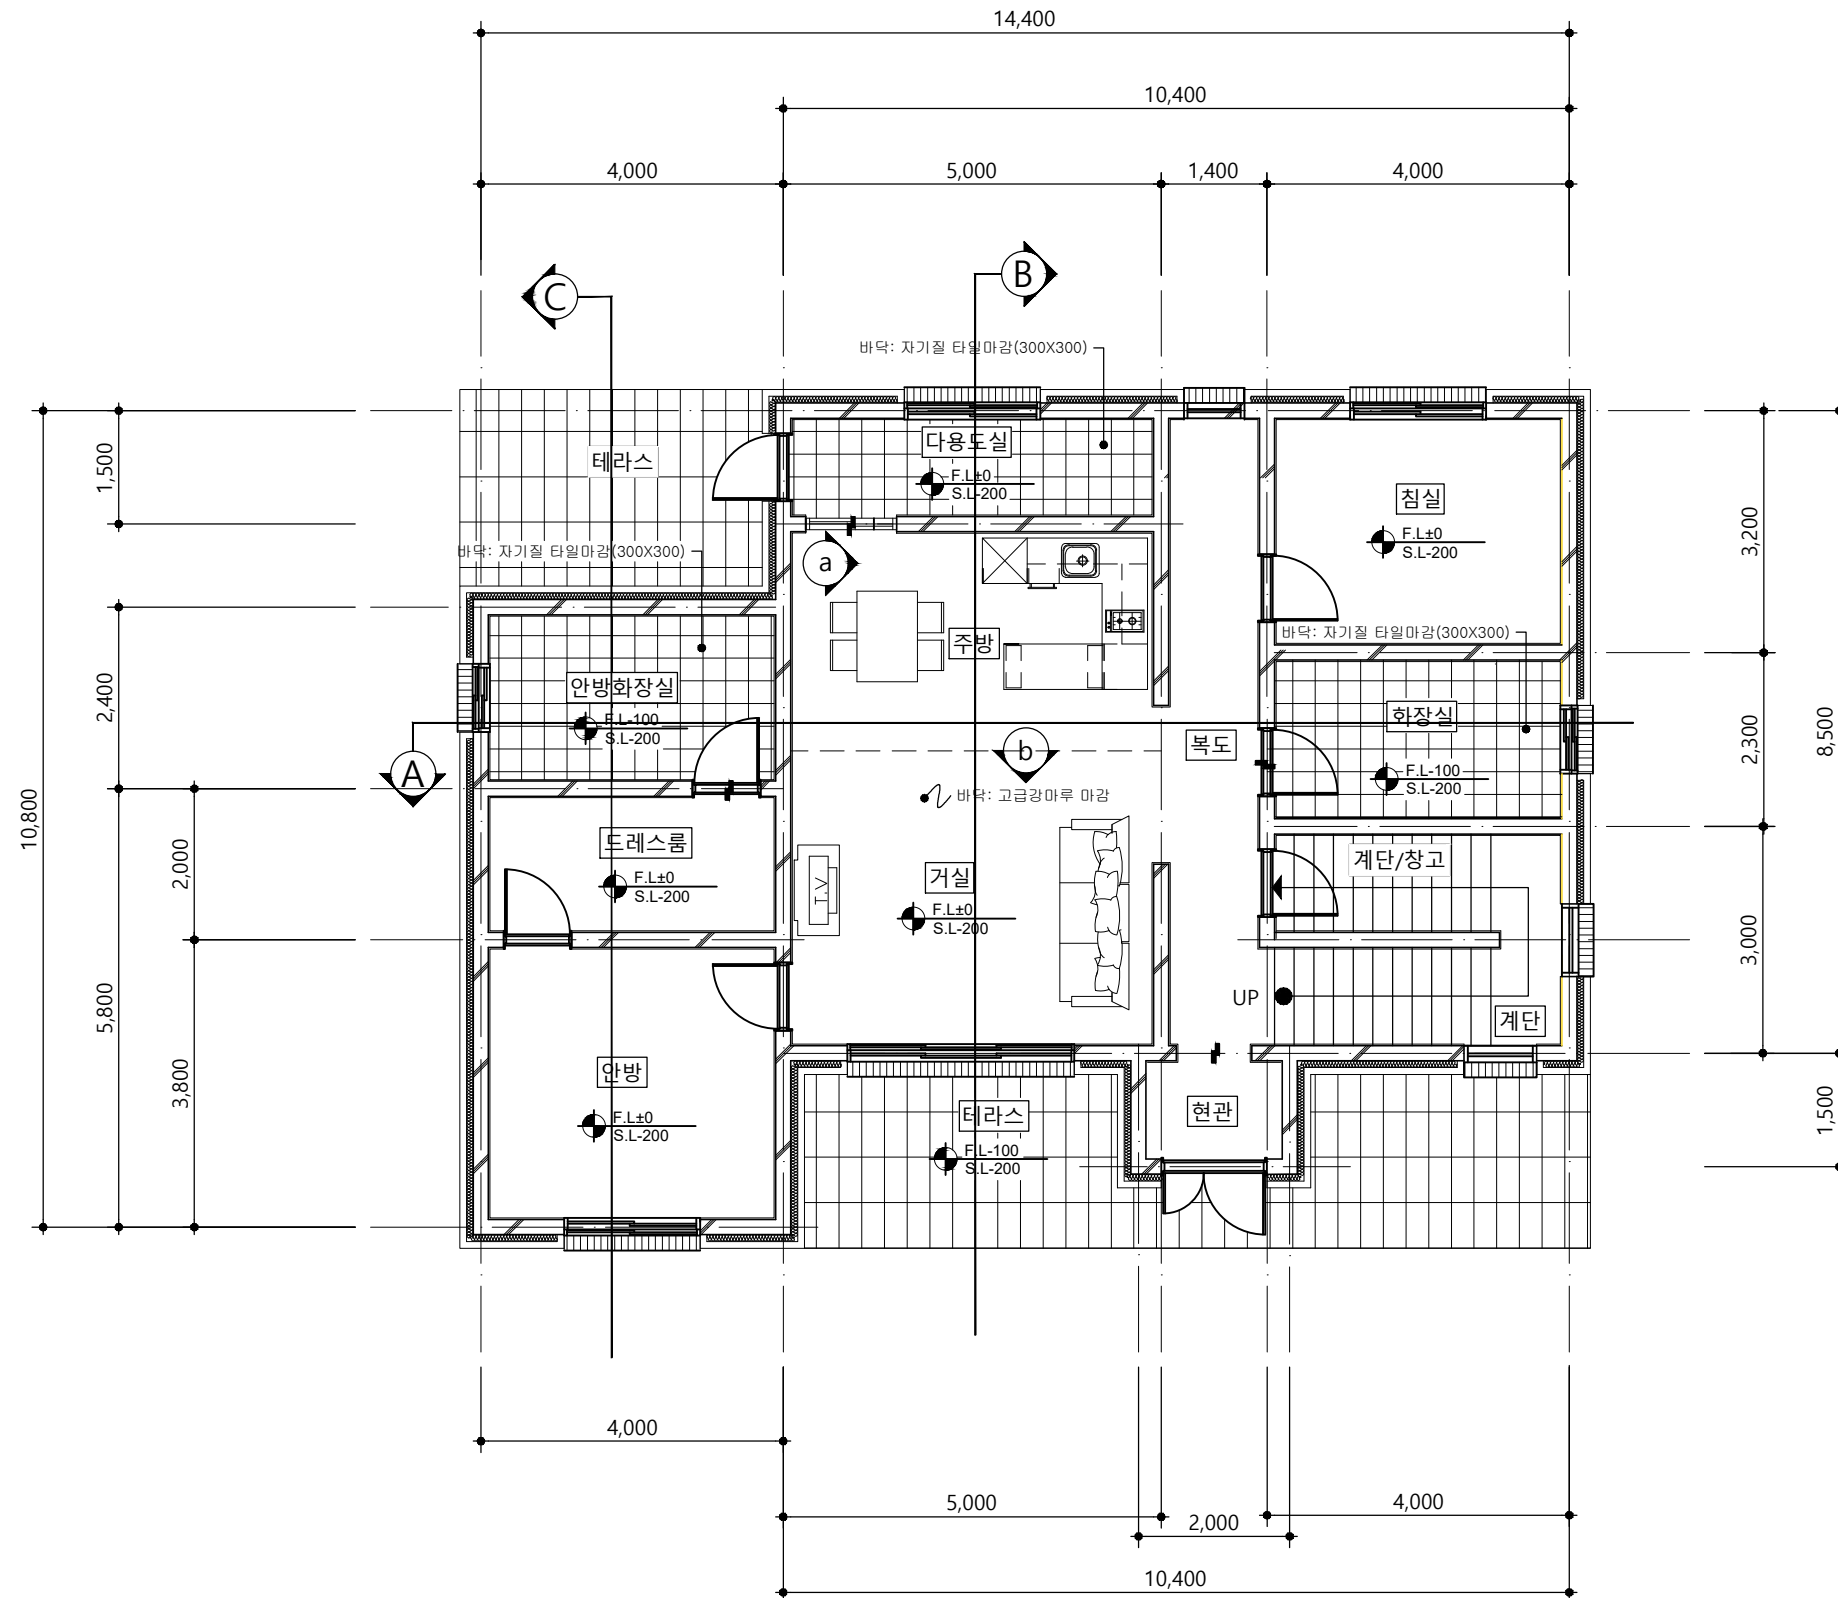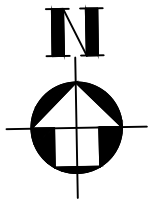

1층 평면도

SCALE : 1/100

특기사항
NOTE

수정사항
REVISION

번호 NO	일 자 DATE	수 정 DESCRIPTION	날 인 SIGN
△			
△			
△			
△			
△			
△			
△			
△			
△			

공사명
PROJECT TITLE

축 치
SCALE

작성일
DATE

설 계
DESIGNED BY

제 도
DRAWN BY

검 사
CHECKED BY

승 인
APPROVED BY




도면명
NAME OF DRAWING

도면번호
DRAWING NO

□ □ □ □ □ □

시공번호
PROJECT NO

TD □ □ □ □ □ □

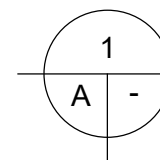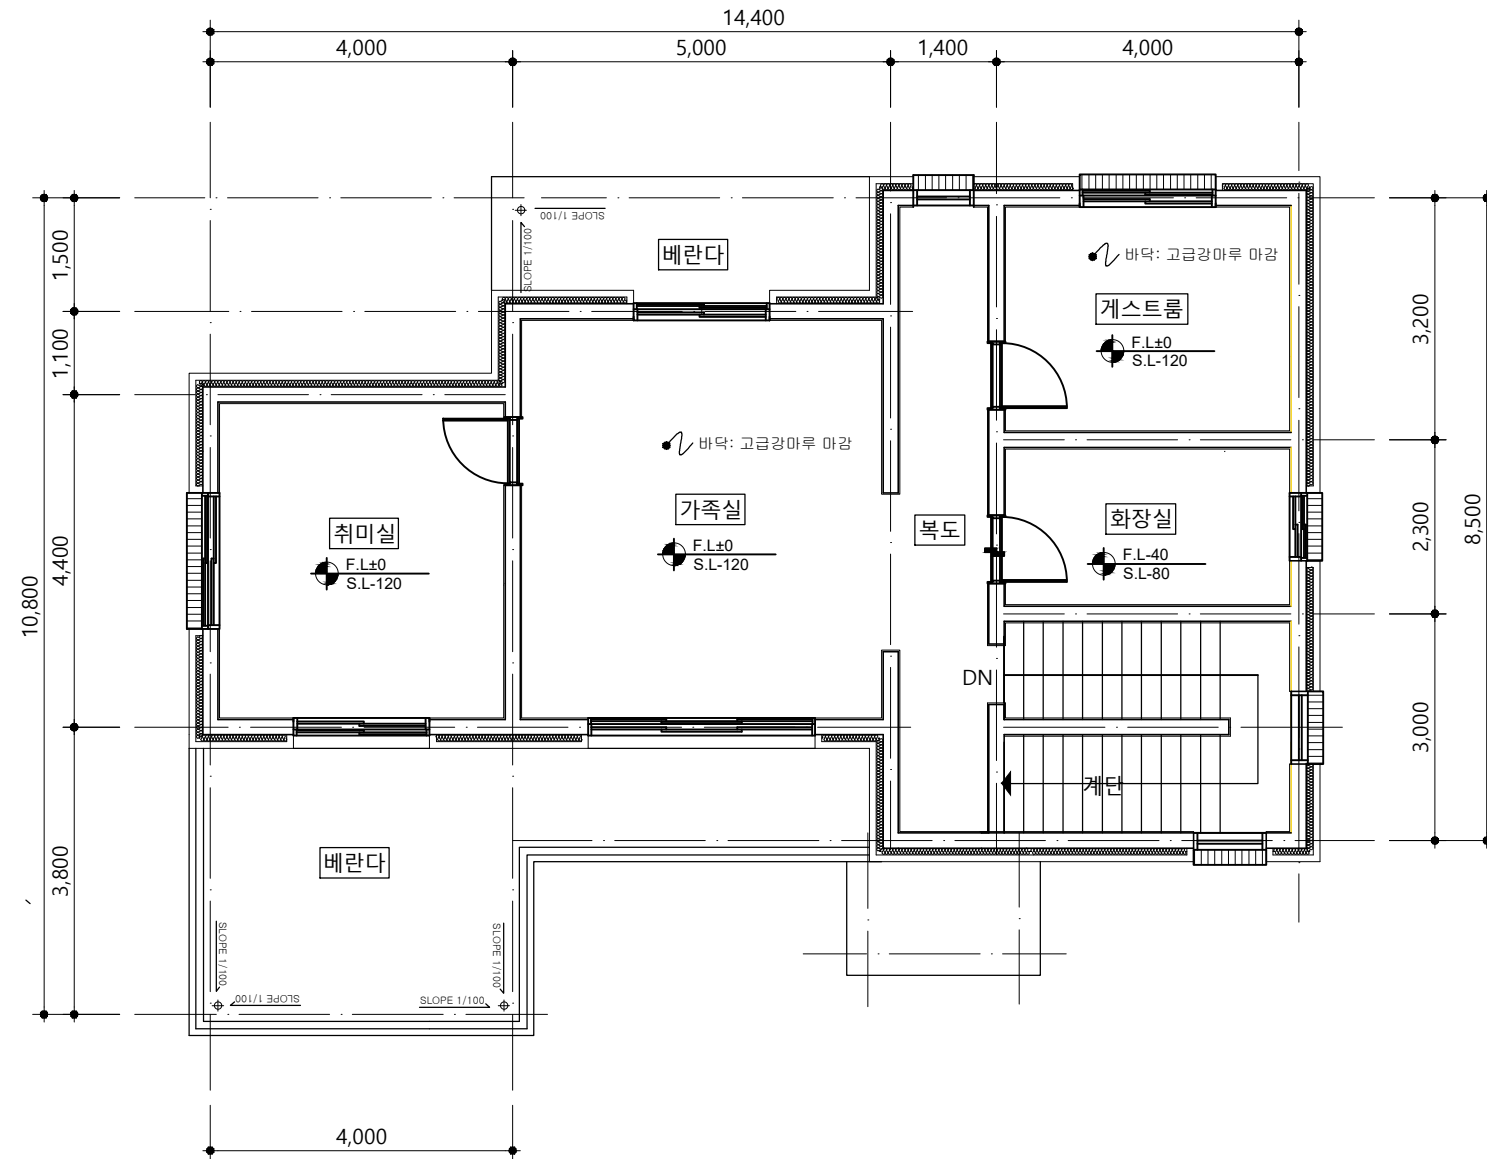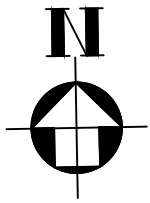

2층 평면도

SCALE : 1/100

특기사항
NOTE수정사항
REVISION




번호 NO	일 자 DATE	수 정 DESCRIPTION	날 인 SIGN
△			
△			
△			
△			
△			
△			
△			
△			
△			

공사명
PROJECT TITLE축 치
SCALE작성일
DATE설 계
DESIGNED BY제 도
DRAWN BY검 사
CHECKED BY승 인
APPROVED BY도면명
NAME OF DRAWING도면번호
DRAWING NO

--	--	--	--	--	--

시공번호
PROJECT NO

TD					
----	--	--	--	--	--

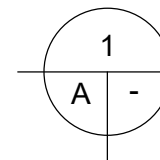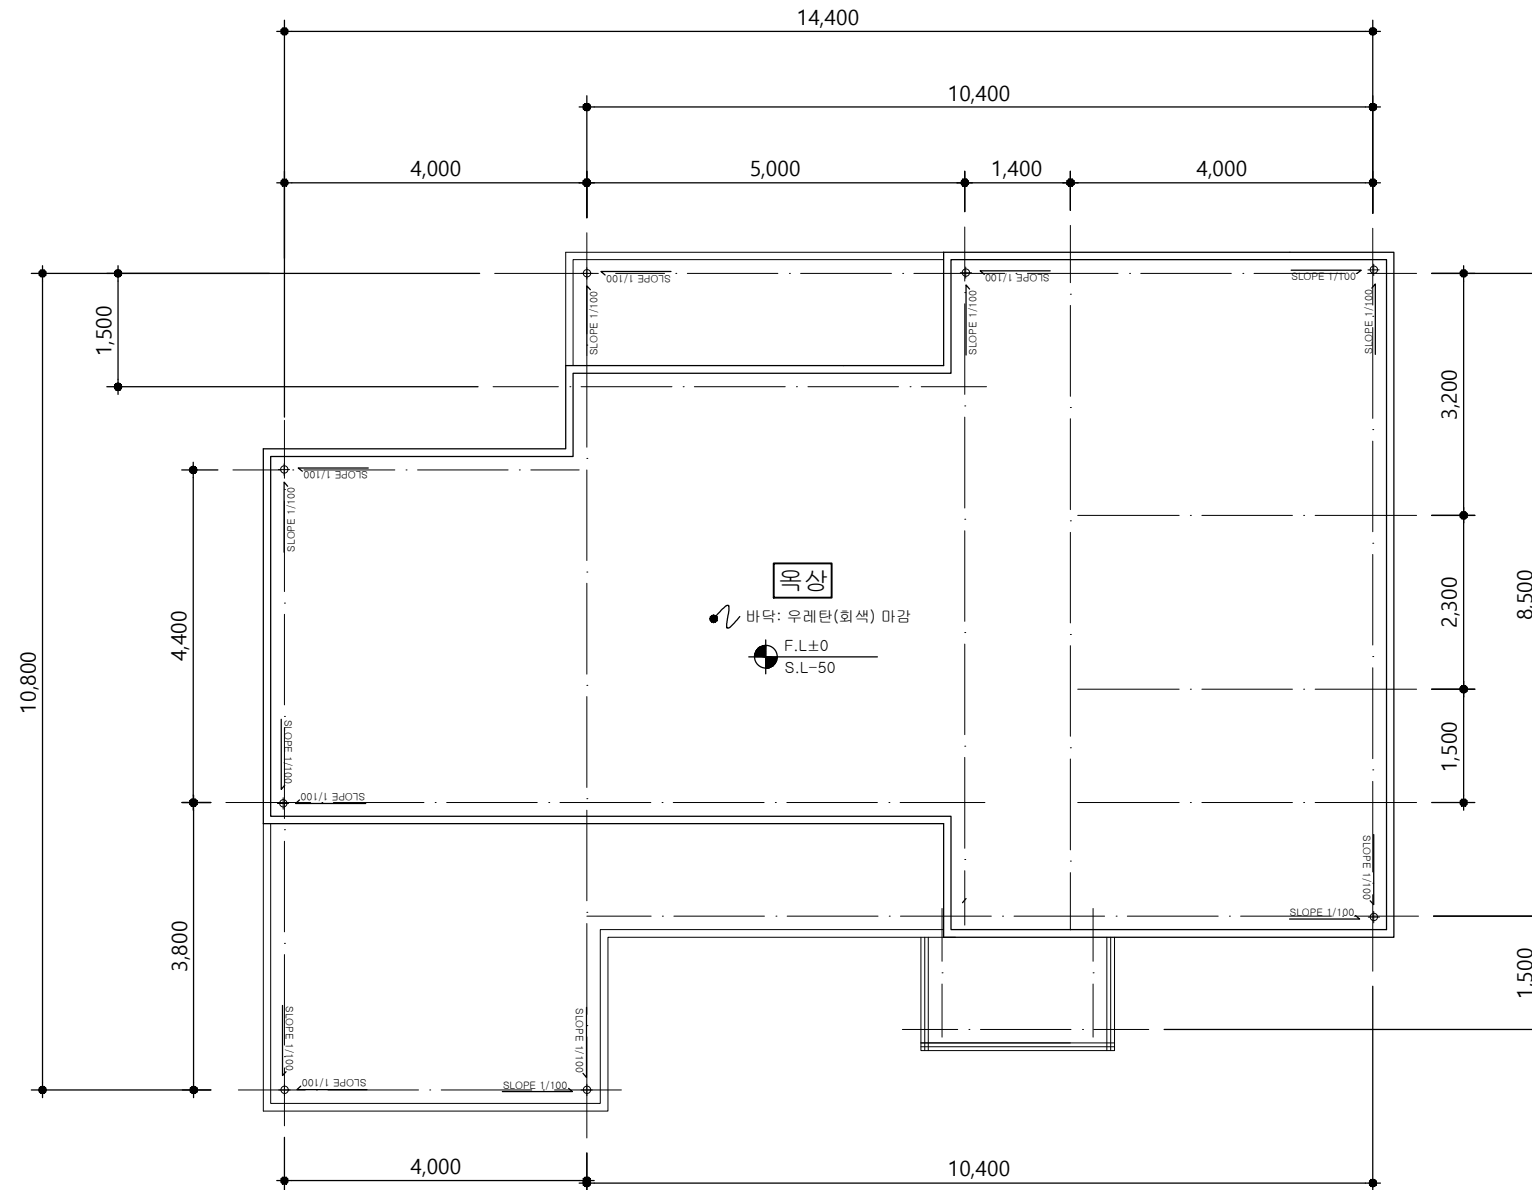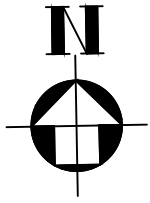

지붕 평면도

SCALE : 1/100

특기사항
NOTE

수정사항
REVISION

번호 NO	일 자 DATE	수 정 DESCRIPTION	날 인 SIGN
△			
△			
△			
△			
△			
△			
△			
△			
△			

공사명
PROJECT TITLE

축 치
SCALE

작성일
DATE

설 계
DESIGNED BY

제 도
DRAWN BY

검 사
CHECKED BY

승 인
APPROVED BY



도면명
NAME OF DRAWING

도면번호
DRAWING NO

□□□□□□

시공번호
PROJECT NO

TD□□□□□□

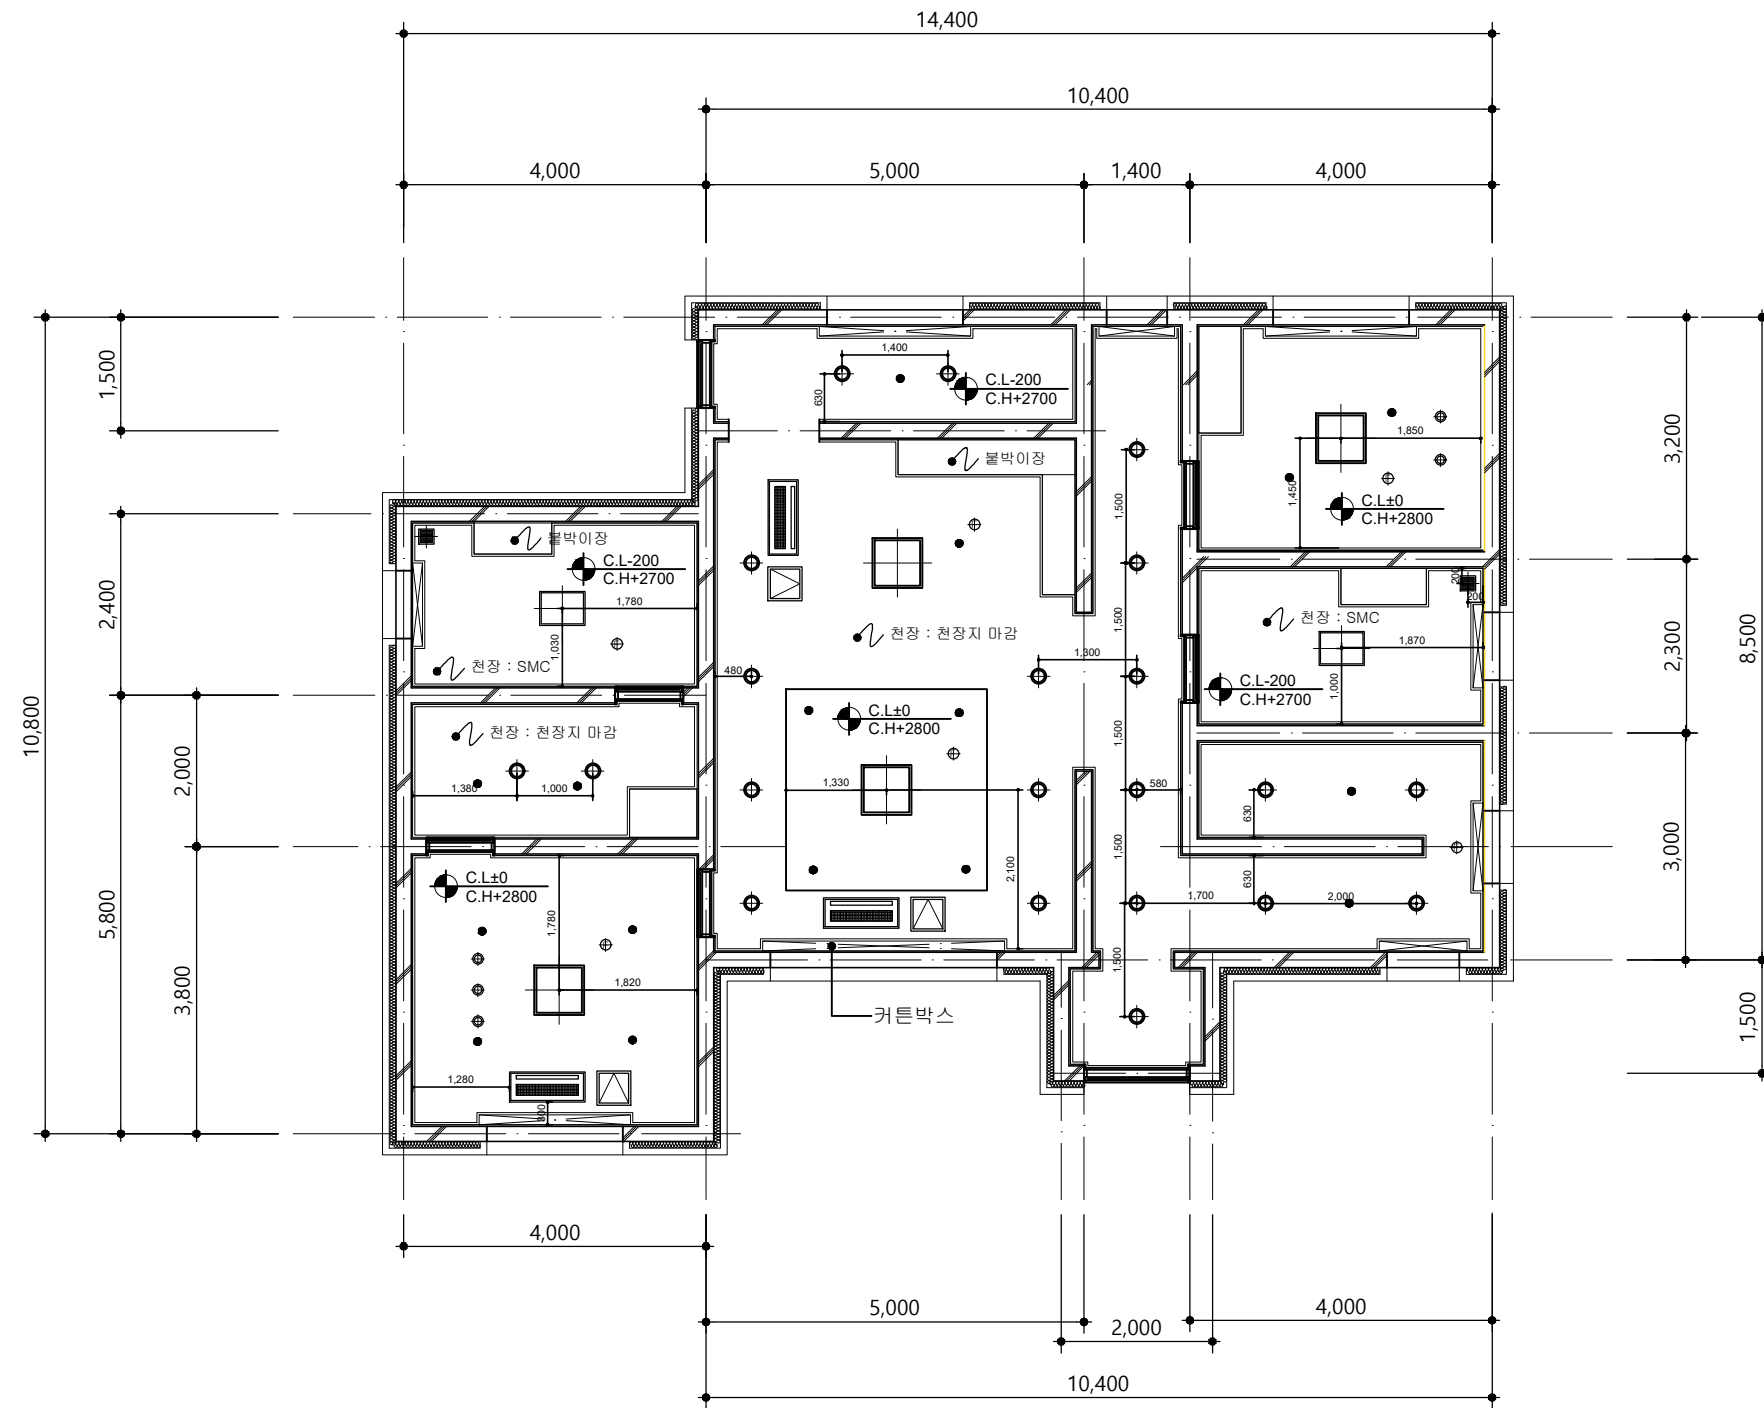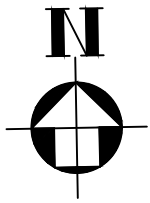


*범례

기 호	이 름(명 칭)	수 량
	SYSTEM A/C 600×600	3
	스프링클러	15
	LED 600×600	4
	LED 원형등 Ø200	21
	환기구 200×200	2
	디퓨저 400x400	3
	LED 방등 410x560	2
	화재감지기	6
	LED 원형등 Ø140	5

1층 천장도

SCALE : 1/100

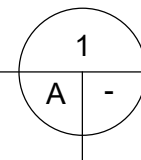

특기사항
NOTE수정사항
REVISION



번호 NO	일자 DATE	수정 DESCRIPTION	날인 SIGN
△			
△			
△			
△			
△			
△			
△			
△			
△			

공사명
PROJECT TITLE축척
SCALE작성일
DATE설계
DESIGNED BY제도
DRAWN BY검사
CHECKED BY승인
APPROVED BY도면명
NAME OF DRAWING도면번호
DRAWING NO

--	--	--	--	--	--

사업번호
PROJECT NOTD-

--	--	--	--	--	--

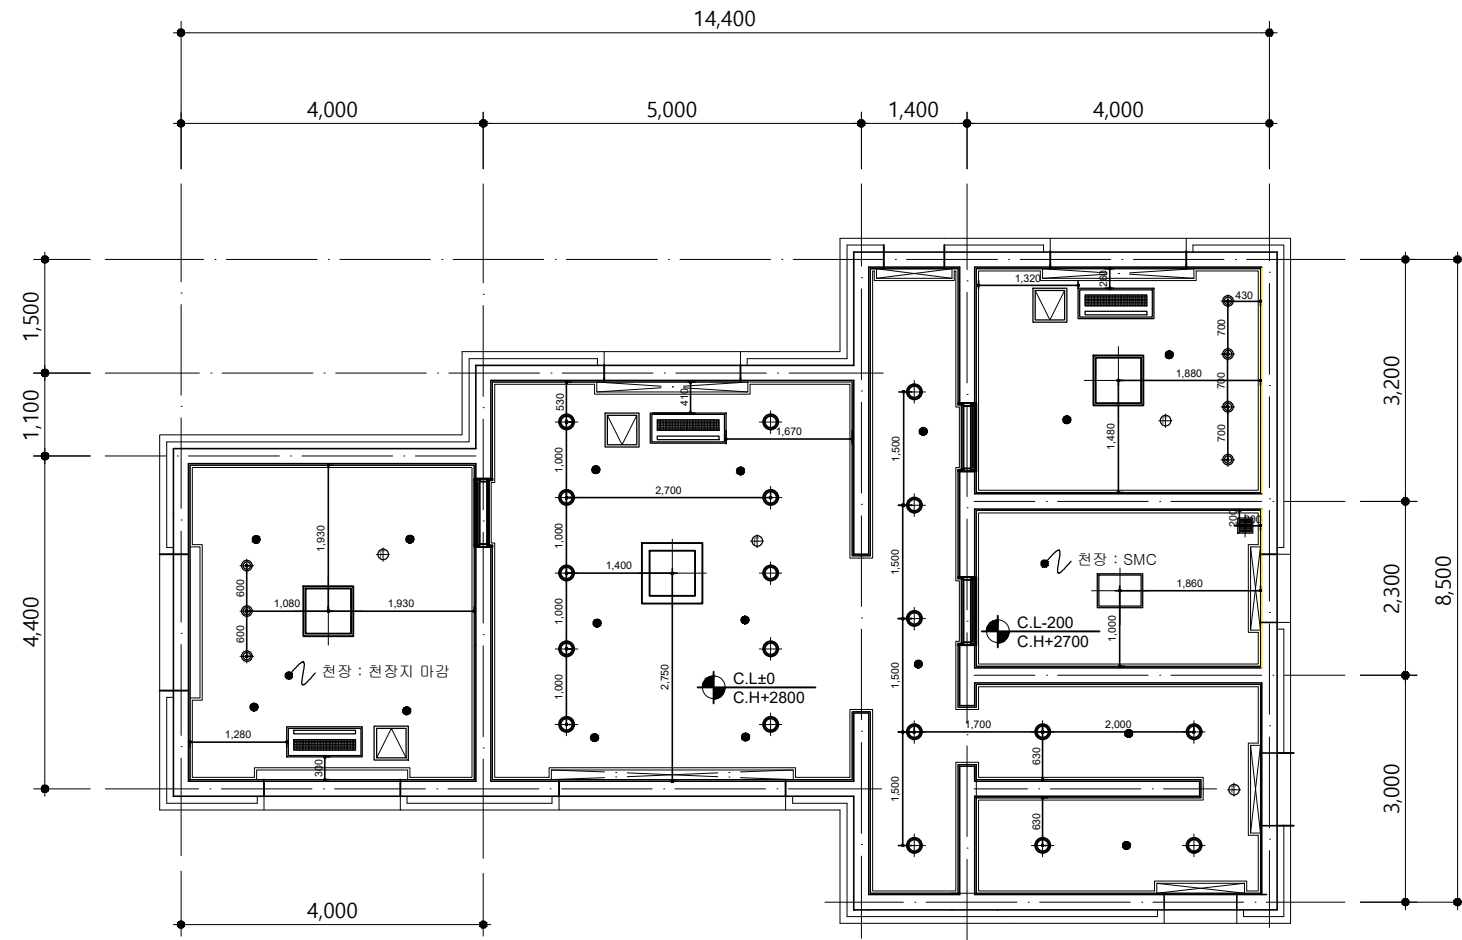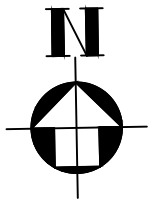

*범례

기호	이름(명칭)	수량
	SYSTEM A/C 600×600	3
	스프링클러	16
	LED 600×600	2
	LED 원형등 Ø200	19
	환기구 200×200	1
	디퓨저 400×400	3
	LED 방등 410×560	1
	화재감지기	3
	LED 원형등 Ø140	7
	LED 방등 800×800	1

2층 천장도

SCALE : 1/100

1
A -

특기사항
NOTE

수정사항
REVISION

번호 NO	일 자 DATE	수 정 DESCRIPTION	날 인 SIGN
△			
△			
△			
△			
△			
△			
△			
△			
△			

공사명
PROJECT TITLE

축 치
SCALE

작성일
DATE

설 계
DESIGNED BY

제 도
DRAWN BY

검 사
CHECKED BY

승 인
APPROVED BY



도면명
NAME OF DRAWING

도면번호
DRAWING NO

--	--	--	--	--	--



시공번호
PROJECT NO

TD					
----	--	--	--	--	--

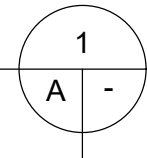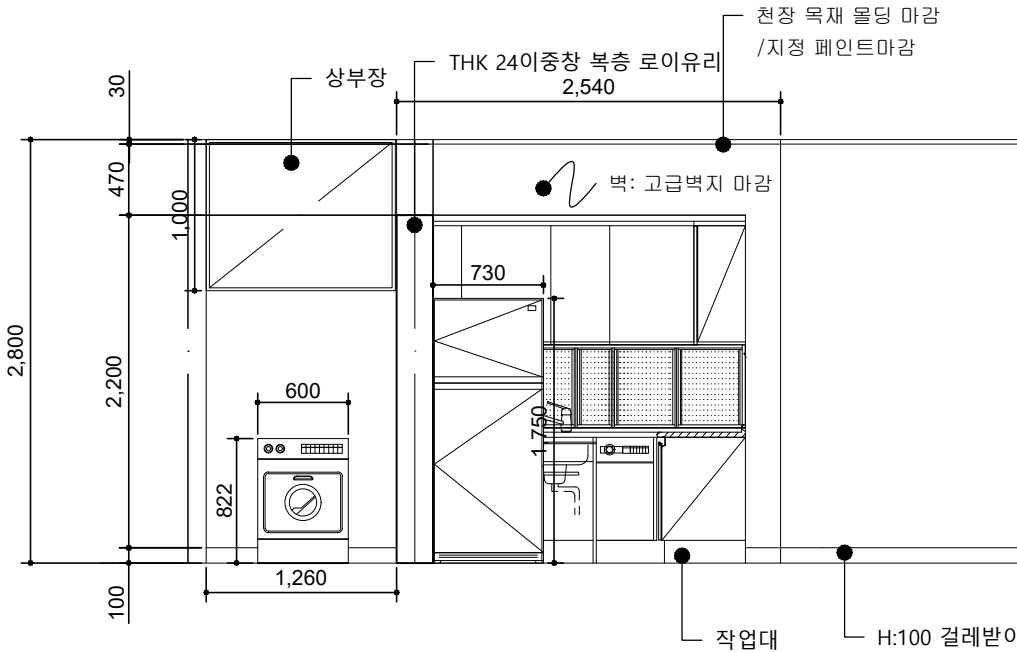

내부입면도 a

SCALE : 1/50

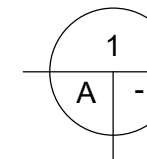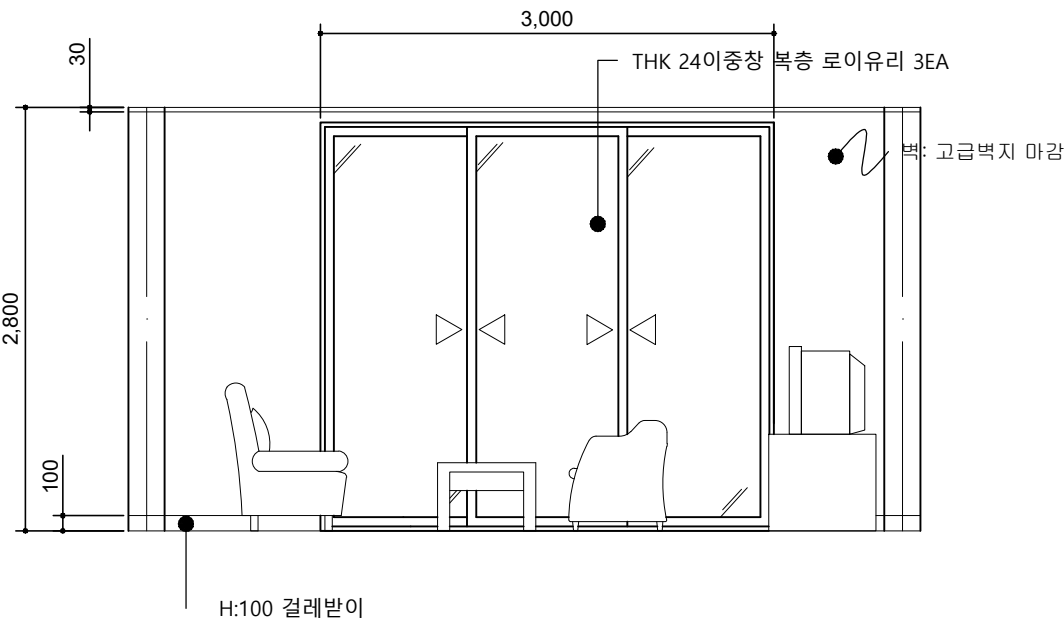

내부입면도 b

SCALE : 1/50

특기사항
NOTE

수정사항
REVISION

번호 NO	일 자 DATE	수 정 DESCRIPTION	날 인 SIGN
△			
△			
△			
△			
△			
△			
△			
△			
△			

공사명
PROJECT TITLE

축 측
SCALE

작성일
DATE

설 계
DESIGNED BY

제 도
DRAWN BY

검 사
CHECKED BY

승 인
APPROVED BY



도면명
NAME OF DRAWING

도면번호
DRAWING NO

--	--	--	--	--	--

시공번호
PROJECT NO

TD					
----	--	--	--	--	--

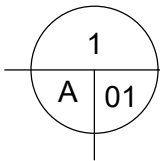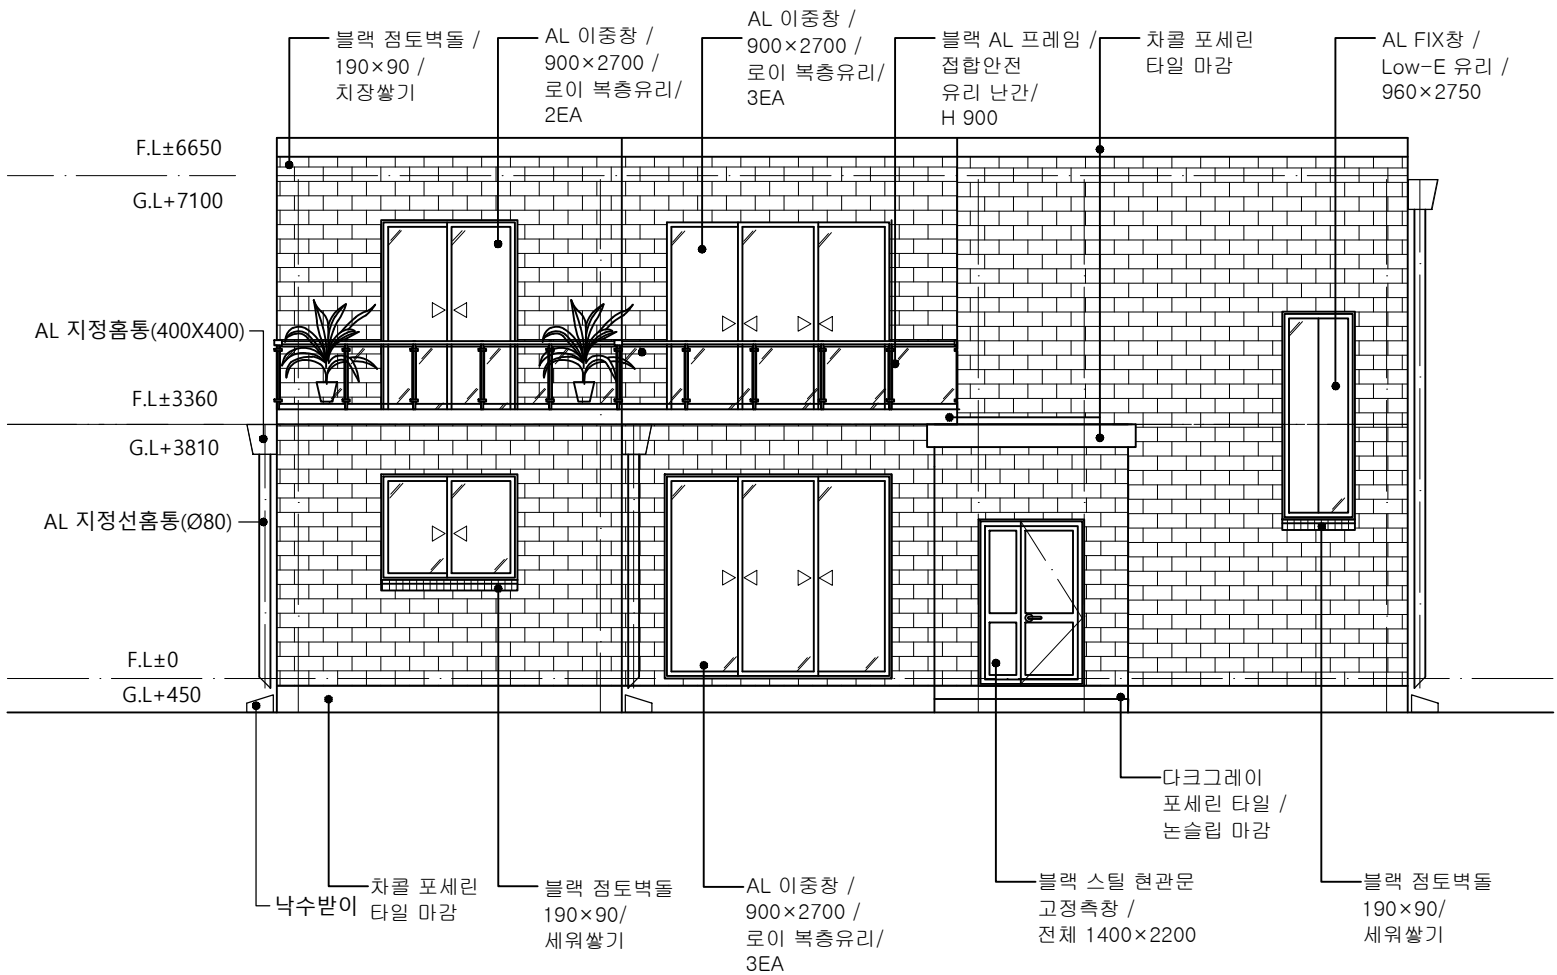

정면도(남측면도)
SCALE : 1/100

특기사항
NOTE

수정사항
REVISION

번호 NO	일 자 DATE	수 정 DESCRIPTION	날 인 SIGN
△			
△			
△			
△			
△			
△			
△			
△			
△			

공사명
PROJECT TITLE

축 치
SCALE

작성일
DATE

설 계
DESIGNED BY

제 도
DRAWN BY

검 사
CHECKED BY

승 인
APPROVED BY



도면명
NAME OF DRAWING

도면번호
DRAWING NO

--	--	--	--	--	--

시공번호
PROJECT NO

TD					
----	--	--	--	--	--

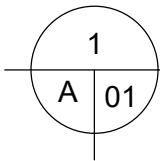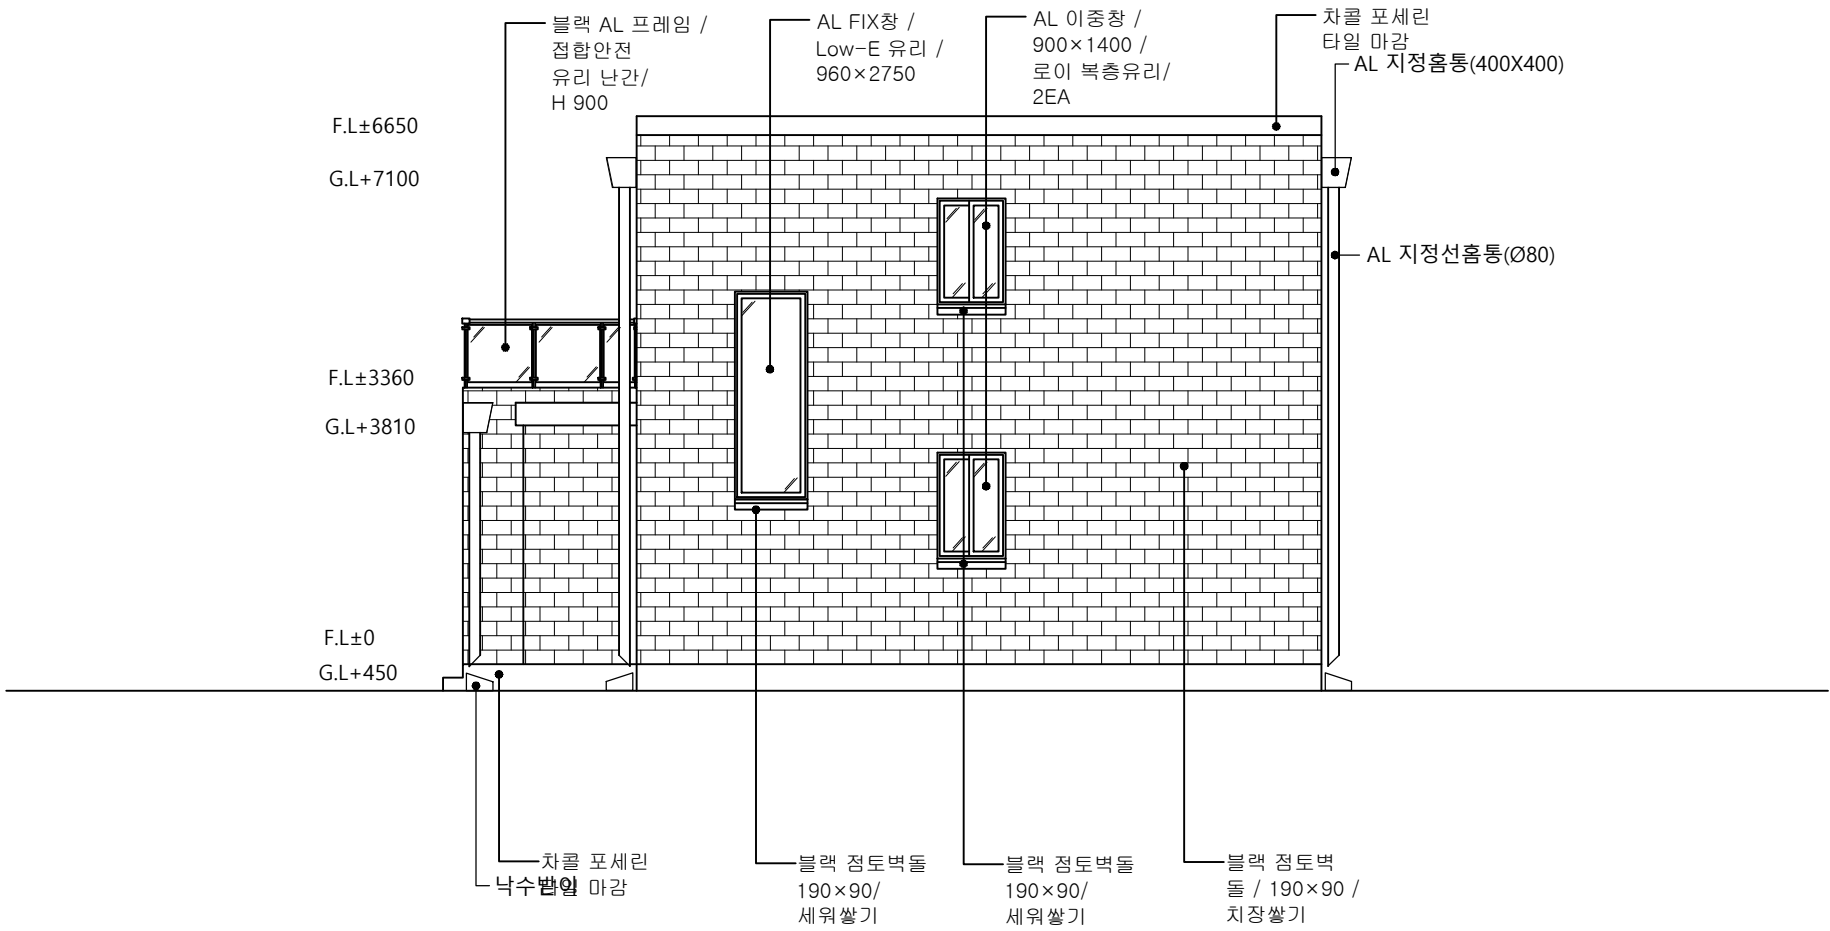

우측면도

SCALE : 1/100

특기사항

NOTE

수정사항

REVISION

번호 NO	일 자 DATE	수 정 DESCRIPTION	날 인 SIGN
△			
△			
△			
△			
△			
△			
△			
△			
△			

공사명

PROJECT TITLE

축 치

SCALE

작성일

DATE

설 계

DESIGNED BY

제 도

DRAWN BY

검 사

CHECKED BY

승 인

APPROVED BY

도면명

NAME OF DRAWING

도면번호



DRAWING NO

--	--	--	--	--	--

시공번호

PROJECT NO

TD					
----	--	--	--	--	--

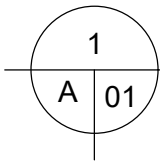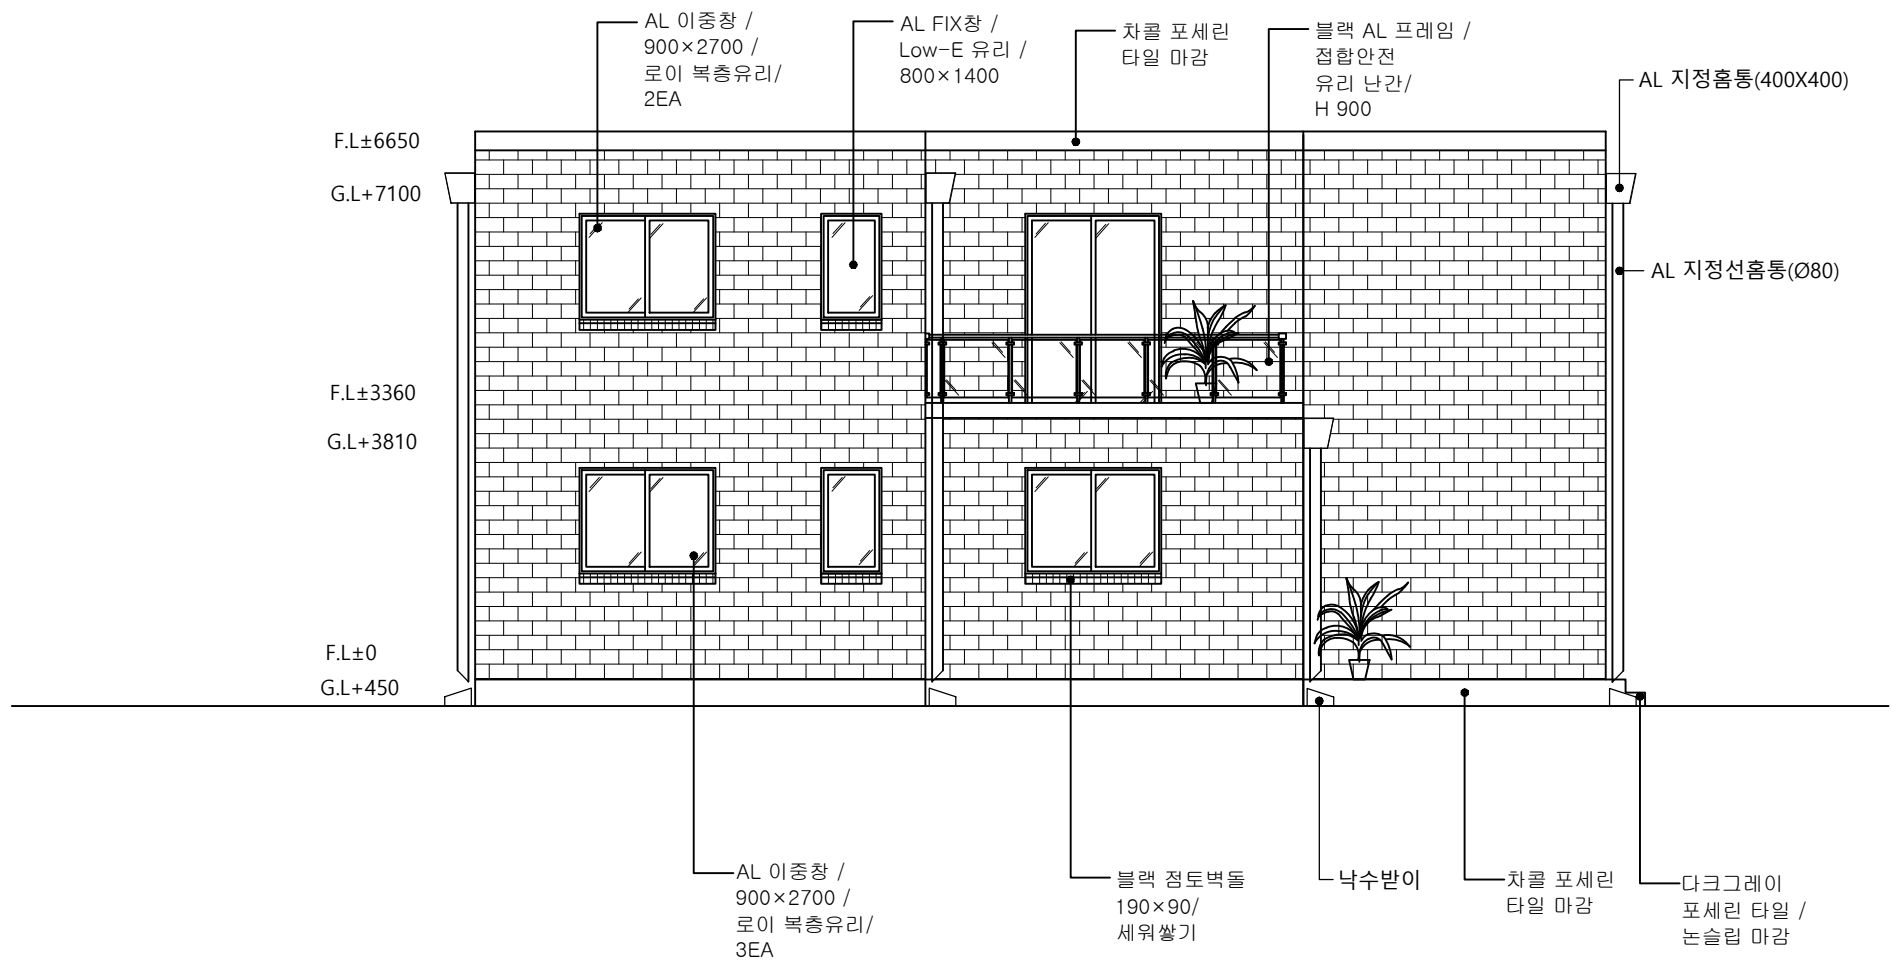

배면도

SCALE : 1/100

특기사항
NOTE

수정사항
REVISION

번호 NO	일 자 DATE	수 정 DESCRIPTION	날 인 SIGN
△			
△			
△			
△			
△			
△			
△			
△			
△			

공사명
PROJECT TITLE

축 측
SCALE

작성일
DATE

설 계
DESIGNED BY

제 도
DRAWN BY

검 사
CHECKED BY

승 인
APPROVED BY



도면명
NAME OF DRAWING

도면번호
DRAWING NO

--	--	--	--	--	--


시공번호
PROJECT NO

TD					
----	--	--	--	--	--

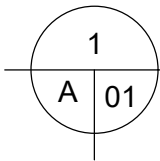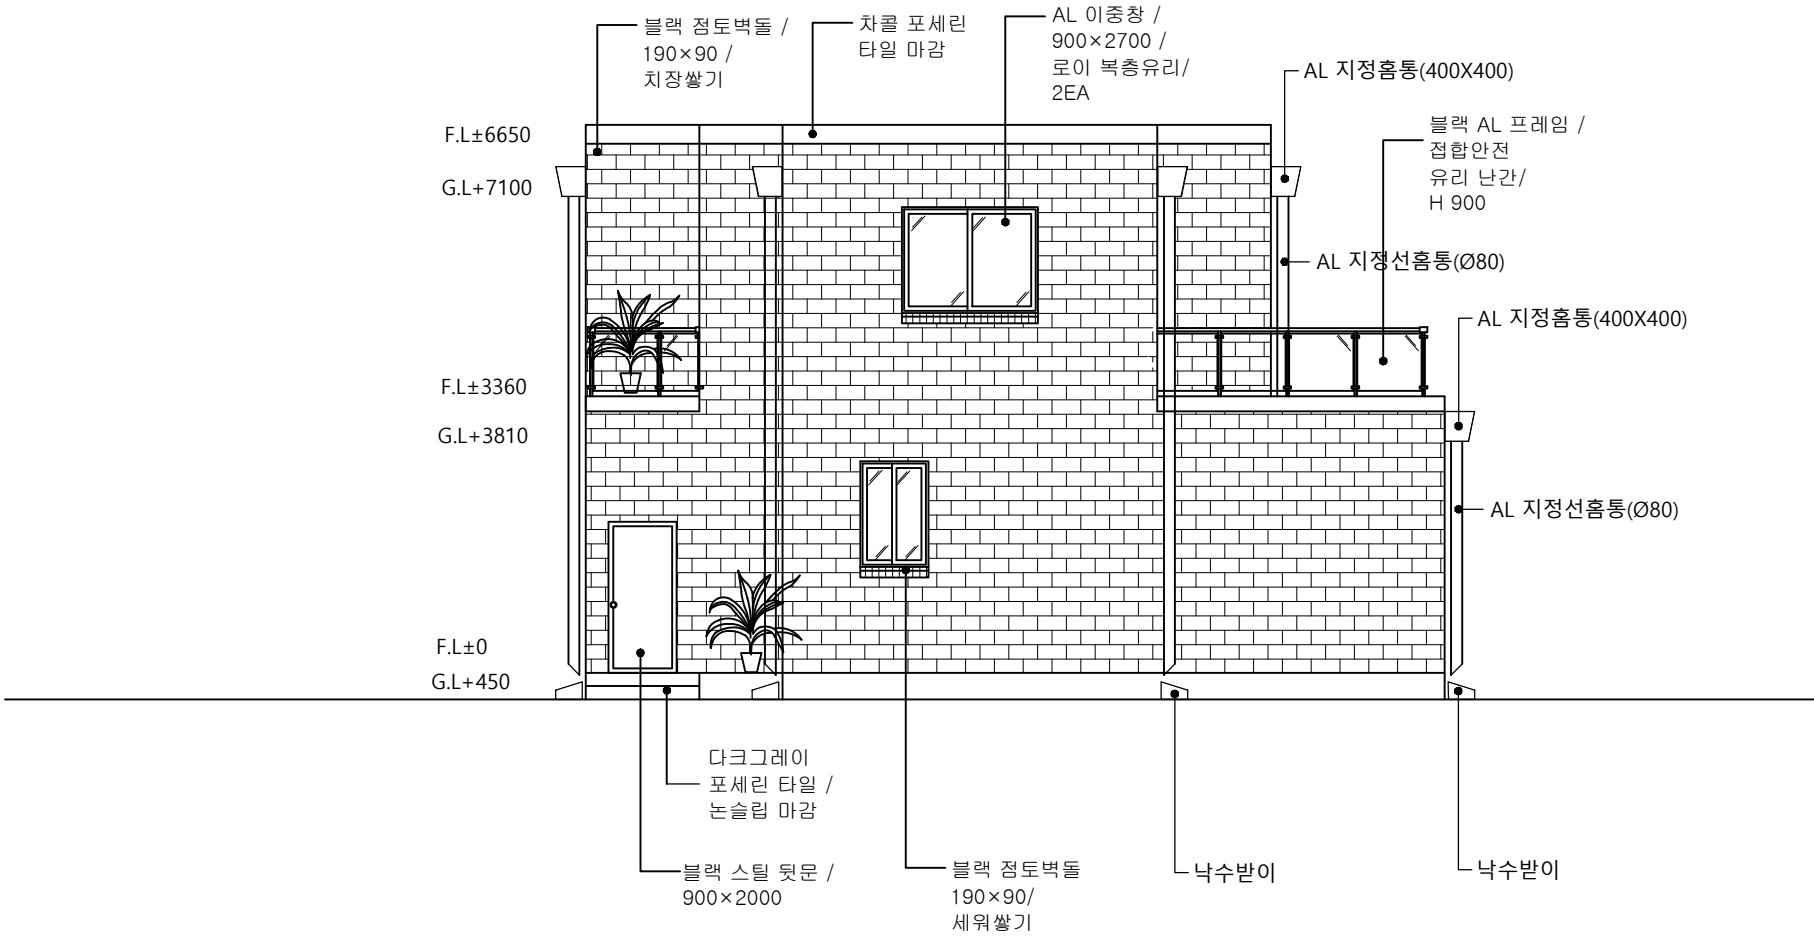

좌측면도

SCALE : 1/100

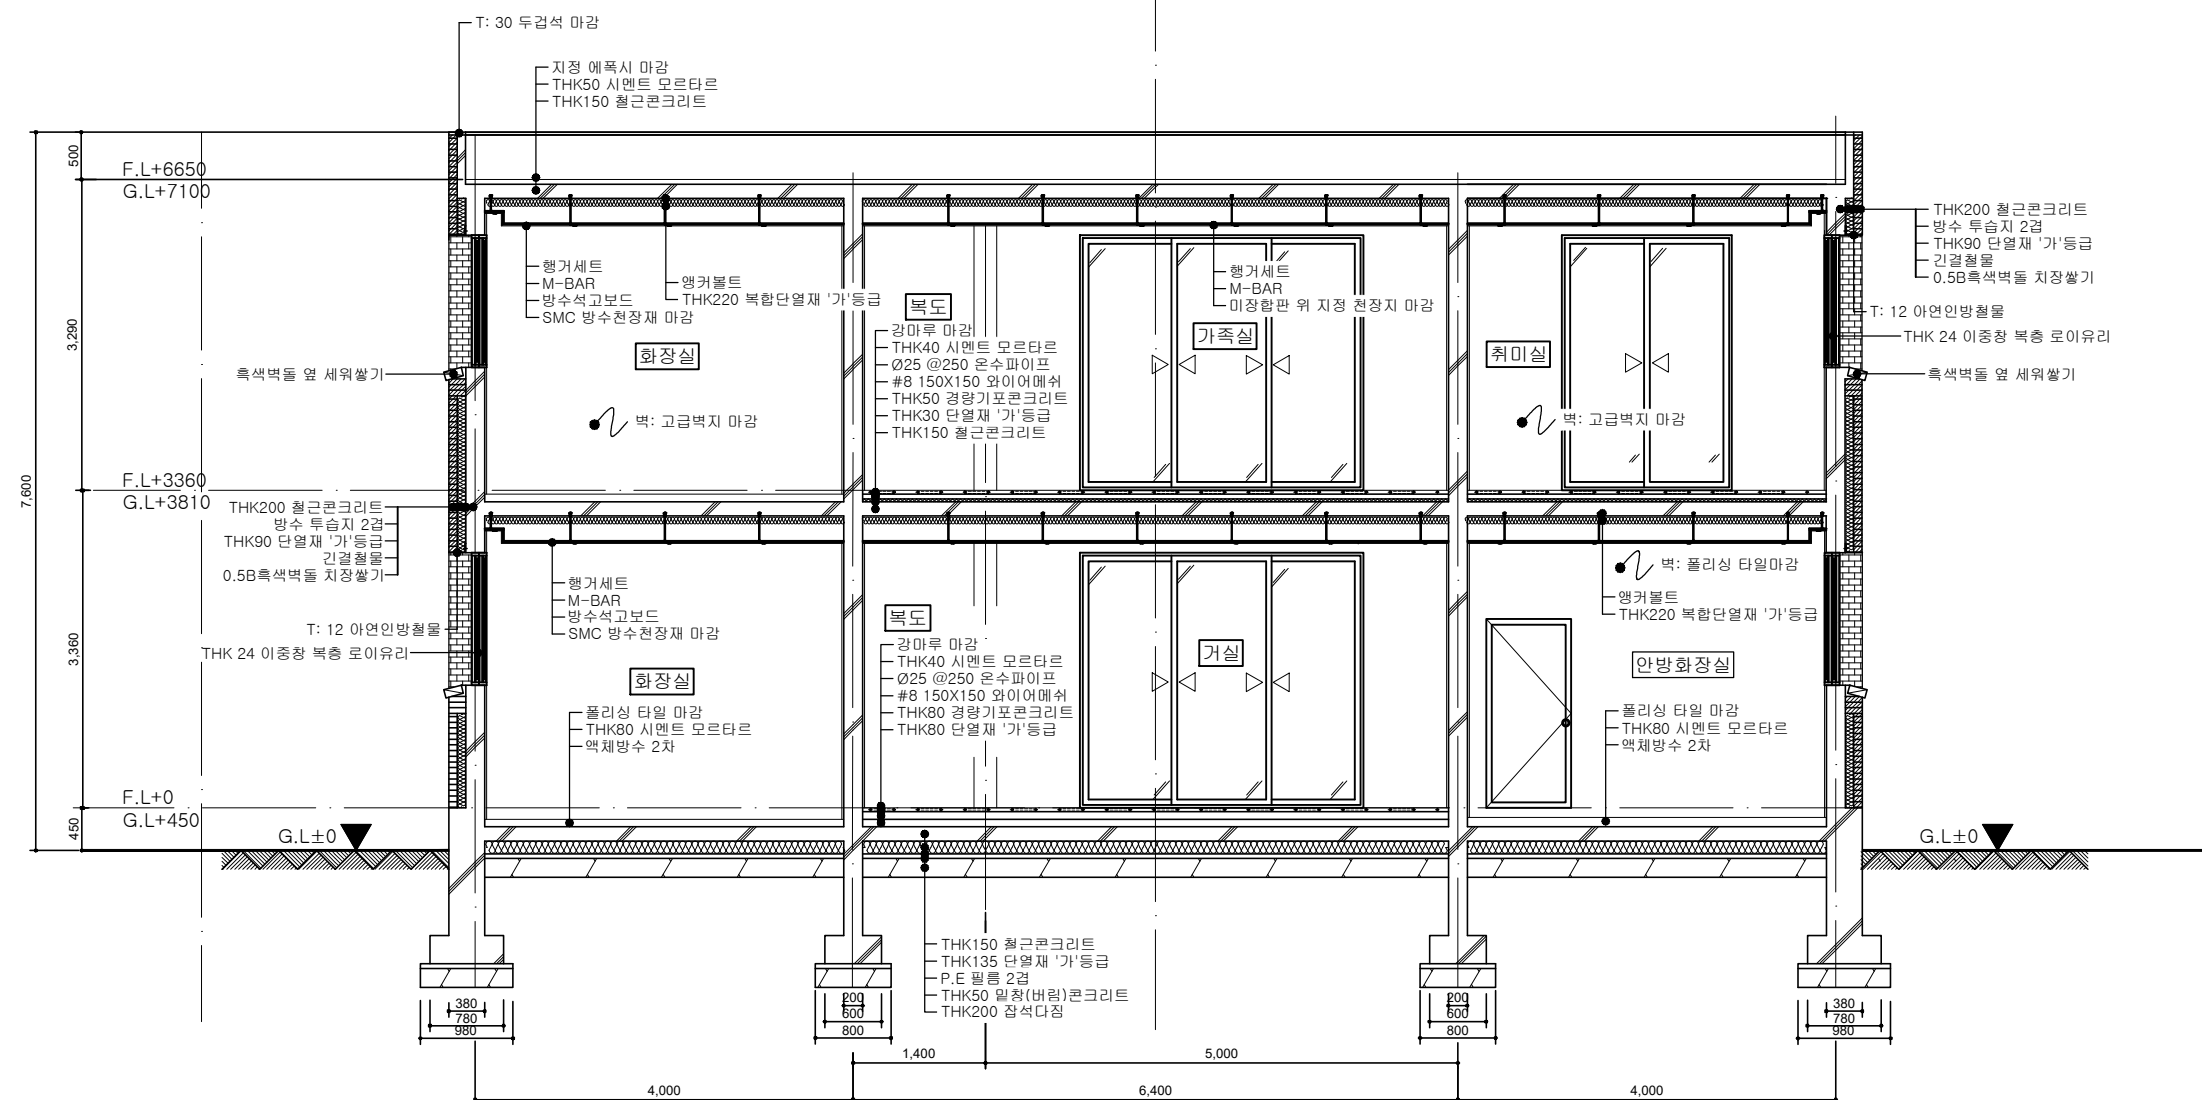

A circle divided into three regions: a top region labeled '1', a bottom-left region labeled 'A', and a bottom-right region labeled '01'.

단면도-A

SCALE : 1/80

[illegible]

공사명
PROJECT TITLE

측 척
SCALE

작성일
DATE

설 계
DESIGNED BY

제 도
DRAWN BY

검 사
CHECKED BY

승인
APPROVED BY


도면명
NAME OF DRAWING

분류번호
DRAWING NO.

Age Group	Number of People
13-17	10
18-24	15
25-34	15
35-44	15
45-54	10
55-64	10

사업번호
PROJECT NO

TD					
----	--	--	--	--	--

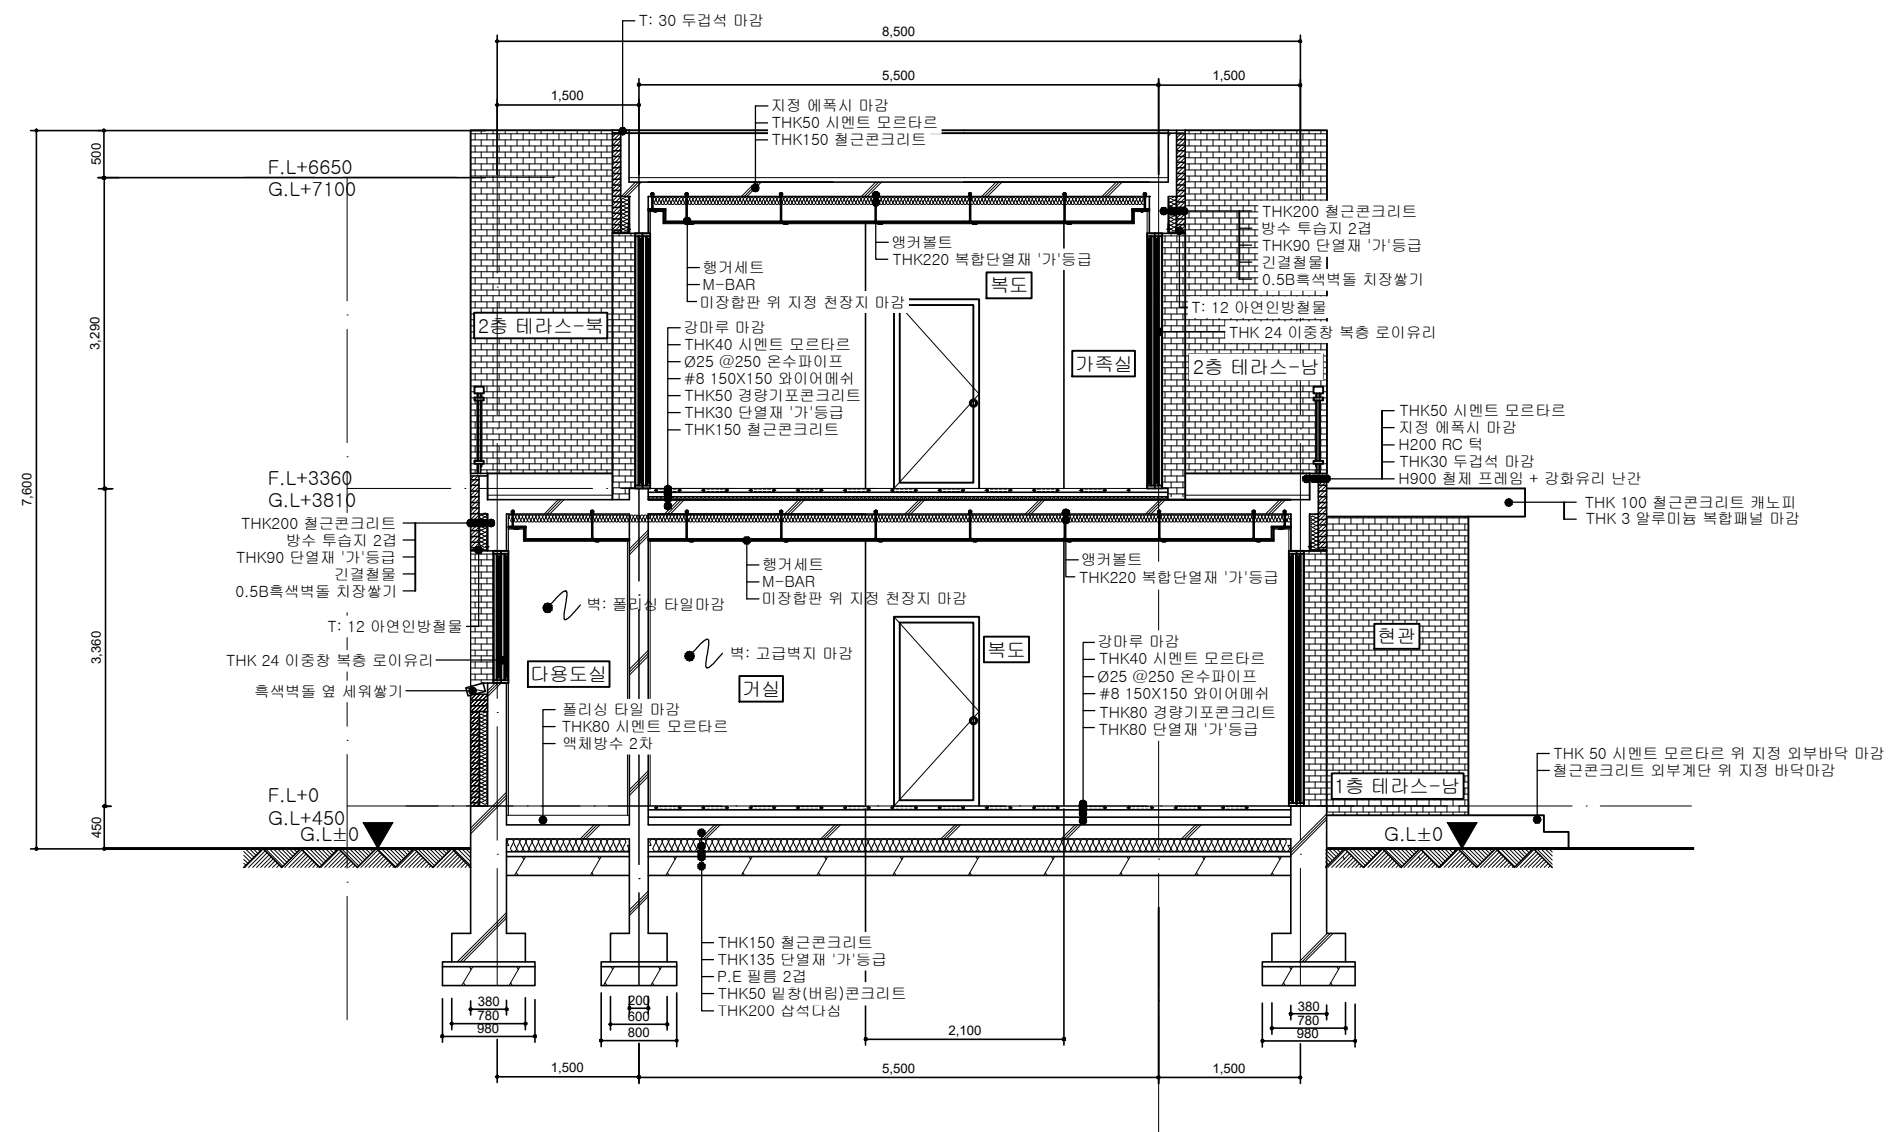

SCALE : 1/80

[illegible]

공사명
PROJECT TITLE

측 척
SCALE

작성일
DATE

설 계
DESIGNED BY

제 도
DRAWN BY

검 사
CHECKED BY

승 인
APPROVED BY

도면명
NAME OF DRAWING


분류번호
DRAWING NO

Age Group	Number of People
13-17	10
18-24	8
25-34	8
35-44	8
45-54	5
55-64	5

사업번호
PROJECT NO

TD					
----	--	--	--	--	--

TD					
----	--	--	--	--	--

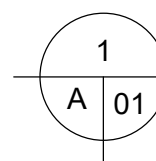

SCALE : 1/80

특기사항

NOTE

수정사항

REVISION

번호 NO	일자 DATE	수정 DESCRIPTION	날인 SIGN
△			
△			
△			
△			
△			
△			
△			
△			
△			

공사명

PROJECT TITLE

축척

SCALE

작성일

DATE

설계

DESIGNED BY

제도

DRAWN BY

검사

CHECKED BY

승인

APPROVED BY

도면명

NAME OF DRAWING

도면번호

DRAWING NO

--	--	--	--	--	--

시공번호

PROJECT NO

TD					
----	--	--	--	--	--

F.L+6650
G.L+7100

F.L+3360
G.L+3810

F.L+0
G.L+450

G.L±0

G.L±0

복도

계단실

복도

H900: 40Ø 철제 벽부형 계단간

T20 지정 우드 철판
T20 지정 우드 디딤판

모르타르 위 지정 페인트 마감

1.680

3,120

1

A 01

계단 단면도

SCALE : 1/50

특기사항
NOTE

수정사항
REVISION

번호 NO	일 자 DATE	수 정 DESCRIPTION	날 인 SIGN
△			
△			
△			
△			
△			
△			
△			
△			
△			

공사명
PROJECT TITLE

축 치
SCALE

작성일
DATE

설 계
DESIGNED BY

제 도
DRAWN BY

검 사
CHECKED BY

승 인
APPROVED BY




도면명
NAME OF DRAWING

도면번호
DRAWING NO

□ □ □ □ □ □

시공번호
PROJECT NO

TD □ □ □ □ □ □

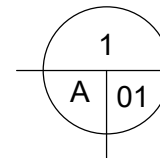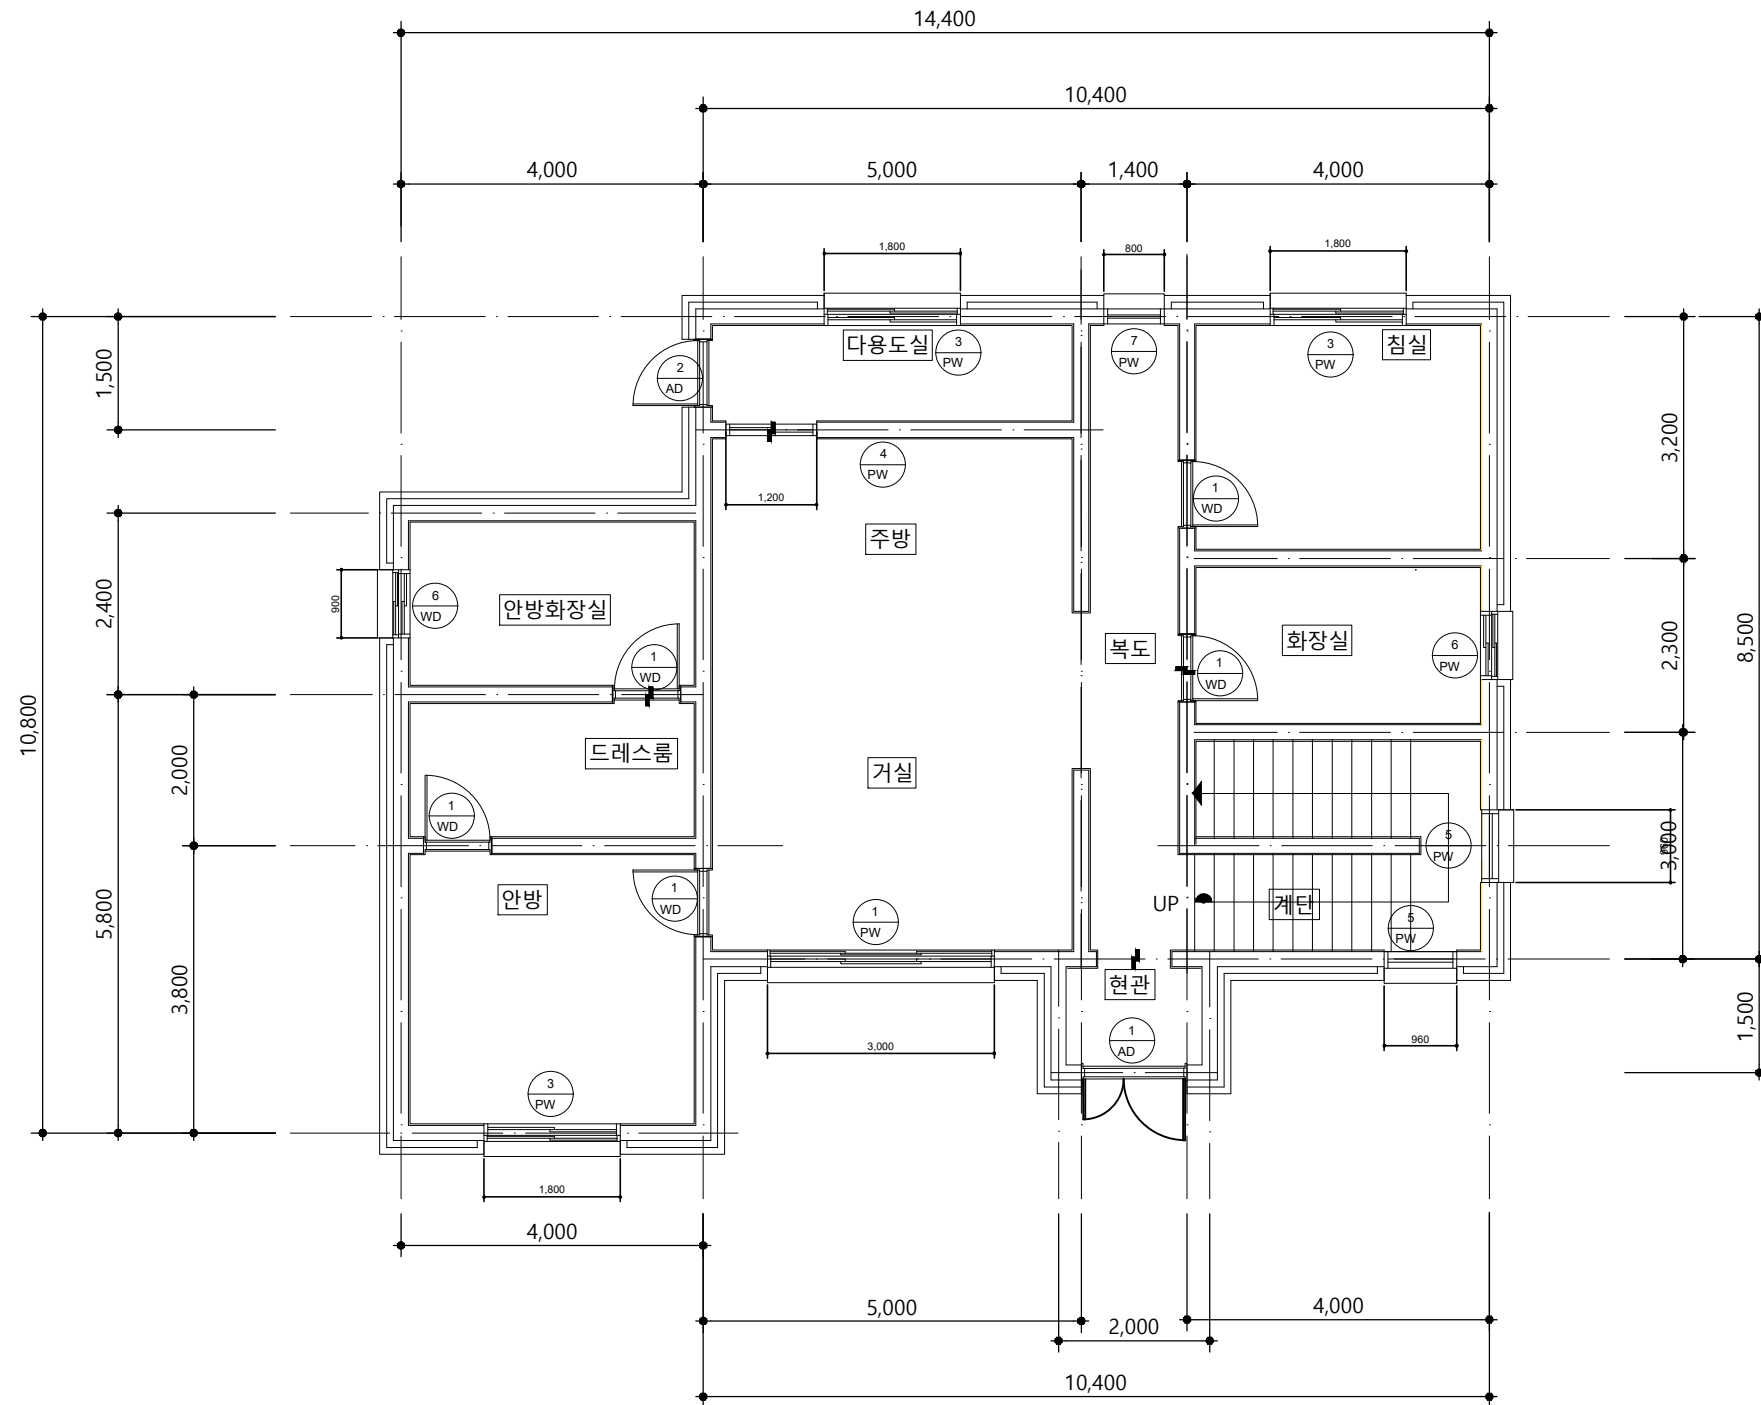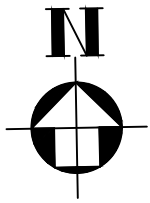

1층 창호안내도

SCALE : 1/100

특기사항
NOTE

수정사항
REVISION

번호 NO	일 자 DATE	수 정 DESCRIPTION	날 인 SIGN
△			
△			
△			
△			
△			
△			
△			
△			
△			

공사명
PROJECT TITLE

축 치
SCALE

작성일
DATE

설 계
DESIGNED BY

제 도
DRAWN BY

검 사
CHECKED BY

승 인
APPROVED BY


도면명
NAME OF DRAWING

분류번호
DRAWING NO

--	--	--	--	--	--


시공번호
PROJECT NO

TD					
----	--	--	--	--	--

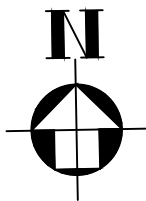

2층 창호안내도

SCALE : 1/100

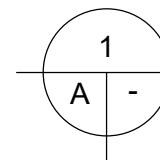

특기사항

NOTE

수정사항

REVISION

번호 NO	일자 DATE	수 DESCRIPTION	정 SIGN
△			
△			
△			
△			
△			
△			
△			
△			
△			

공사명

PROJECT TITLE

축
SCALE

작성
DATE

설
DESIGNED BY

제
DRAWN BY

검
CHECKED BY

승
APPROVED BY








도면
NAME OF DRAWING


도면
DRAWING NO

--	--	--	--	--	--

시공
PROJECT NO

TD					
----	--	--	--	--	--

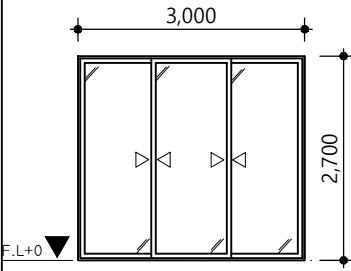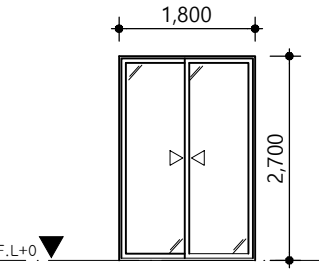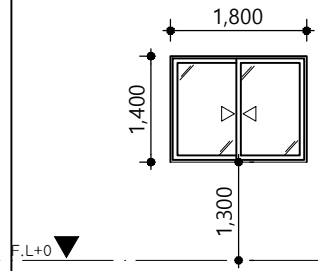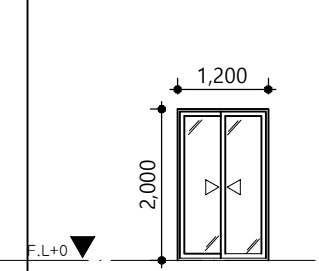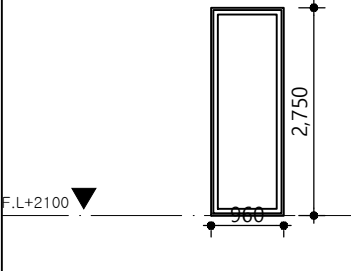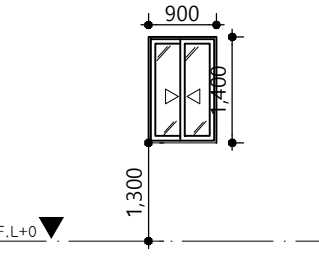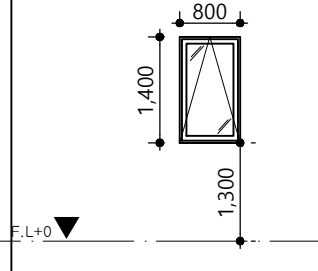형 태				
창호제작성(제구부착수)	3000×2700	1800×2700	1800×1400	1200×2000
명 칭, 위 치	1 3연동 미서기창	2 2연동 미서기창	3 2연동 미서기창	4 2연동 미서기창
재 료	PW AL, 복층유리	PW AL, 복층유리	PW AL, 복층유리	PW AL, 복층유리
마 감	분체도장	분체도장	분체도장	분체도장
부 속	호차, 손잡이, 크레센트	호차, 손잡이, 크레센트	호차, 손잡이, 크레센트	호차, 손잡이, 크레센트
형 태				
창호제작성(제구부착수)	960×2750	900×1400	800×1400	
명 칭, 위 치	5 고정창(FIX)	6 2연동 미서기창	7 프로젝트창	
재 료	PW AL, 복층유리	PW AL, 복층유리	PW AL, 복층유리	
마 감	분체도장	분체도장	분체도장	
부 속	고정틀물	호차, 손잡이, 크레센트	프로젝트호차, 손잡이, 개폐기	
형 태				
창호제작성(제구부착수)				
명 칭, 위 치				
재 료				
마 감				
부 속				

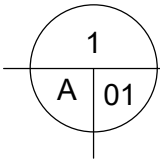

창호일람표

SCALE : N.S

특기사항
NOTE

수정사항
REVISION

번호 NO	일 자 DATE	수 정 DESCRIPTION	날 인 SIGN
△			
△			
△			
△			
△			
△			
△			
△			
△			
△			

공사명
PROJECT TITLE

축 척
SCALE

작성일
DATE

설 계
DESIGNED BY

제 도
DRAWN BY

검 사
CHECKED BY

승 인
APPROVED BY






도면명
NAME OF DRAWING


도면번호
DRAWING NO

--	--	--	--	--	--

시공번호
PROJECT NO

TD					
----	--	--	--	--	--

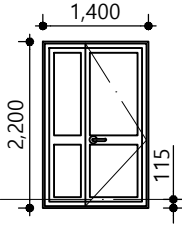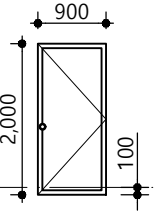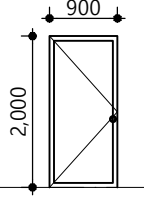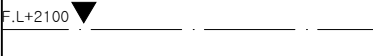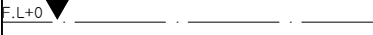형 태				
창호제형사수(개구부사수)	1400X2200	900x2000	900x2000	
형 칭, 위 치	1 한관문(양개문)	2 후문(단개문)	1 실내문(단개문)	
재 료	AD AL	AD AL	WD WOOD	
마 감	분체도장	분체도장	분체도장	
부 속	도어클로저, 손잡이, 도어록, 힌지	도어클로저, 손잡이, 도어록, 힌지	손잡이, 힌지	
형 태				
창호제형사수(개구부사수)				
형 칭, 위 치				
재 료				
마 감				
부 속				
형 태				
창호제형사수(개구부사수)				
형 칭, 위 치				
재 료				
마 감				
부 속				

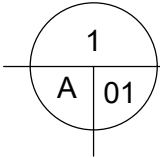

창호일람표

SCALE : N.S

특기사항
NOTE

수정사항
REVISION

번호 NO	일자 DATE	수정 DESCRIPTION	날인 SIGN
△			
△			
△			
△			
△			
△			
△			
△			
△			

공사명
PROJECT TITLE

축척
SCALE

작성일
DATE

설계
DESIGNED BY

제도
DRAWN BY

검사
CHECKED BY

승인
APPROVED BY



도면명
NAME OF DRAWING

도면번호
DRAWING NO

□□□□□□

시공번호
PROJECT NO

TD□□□□□□

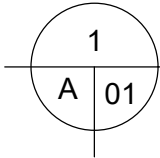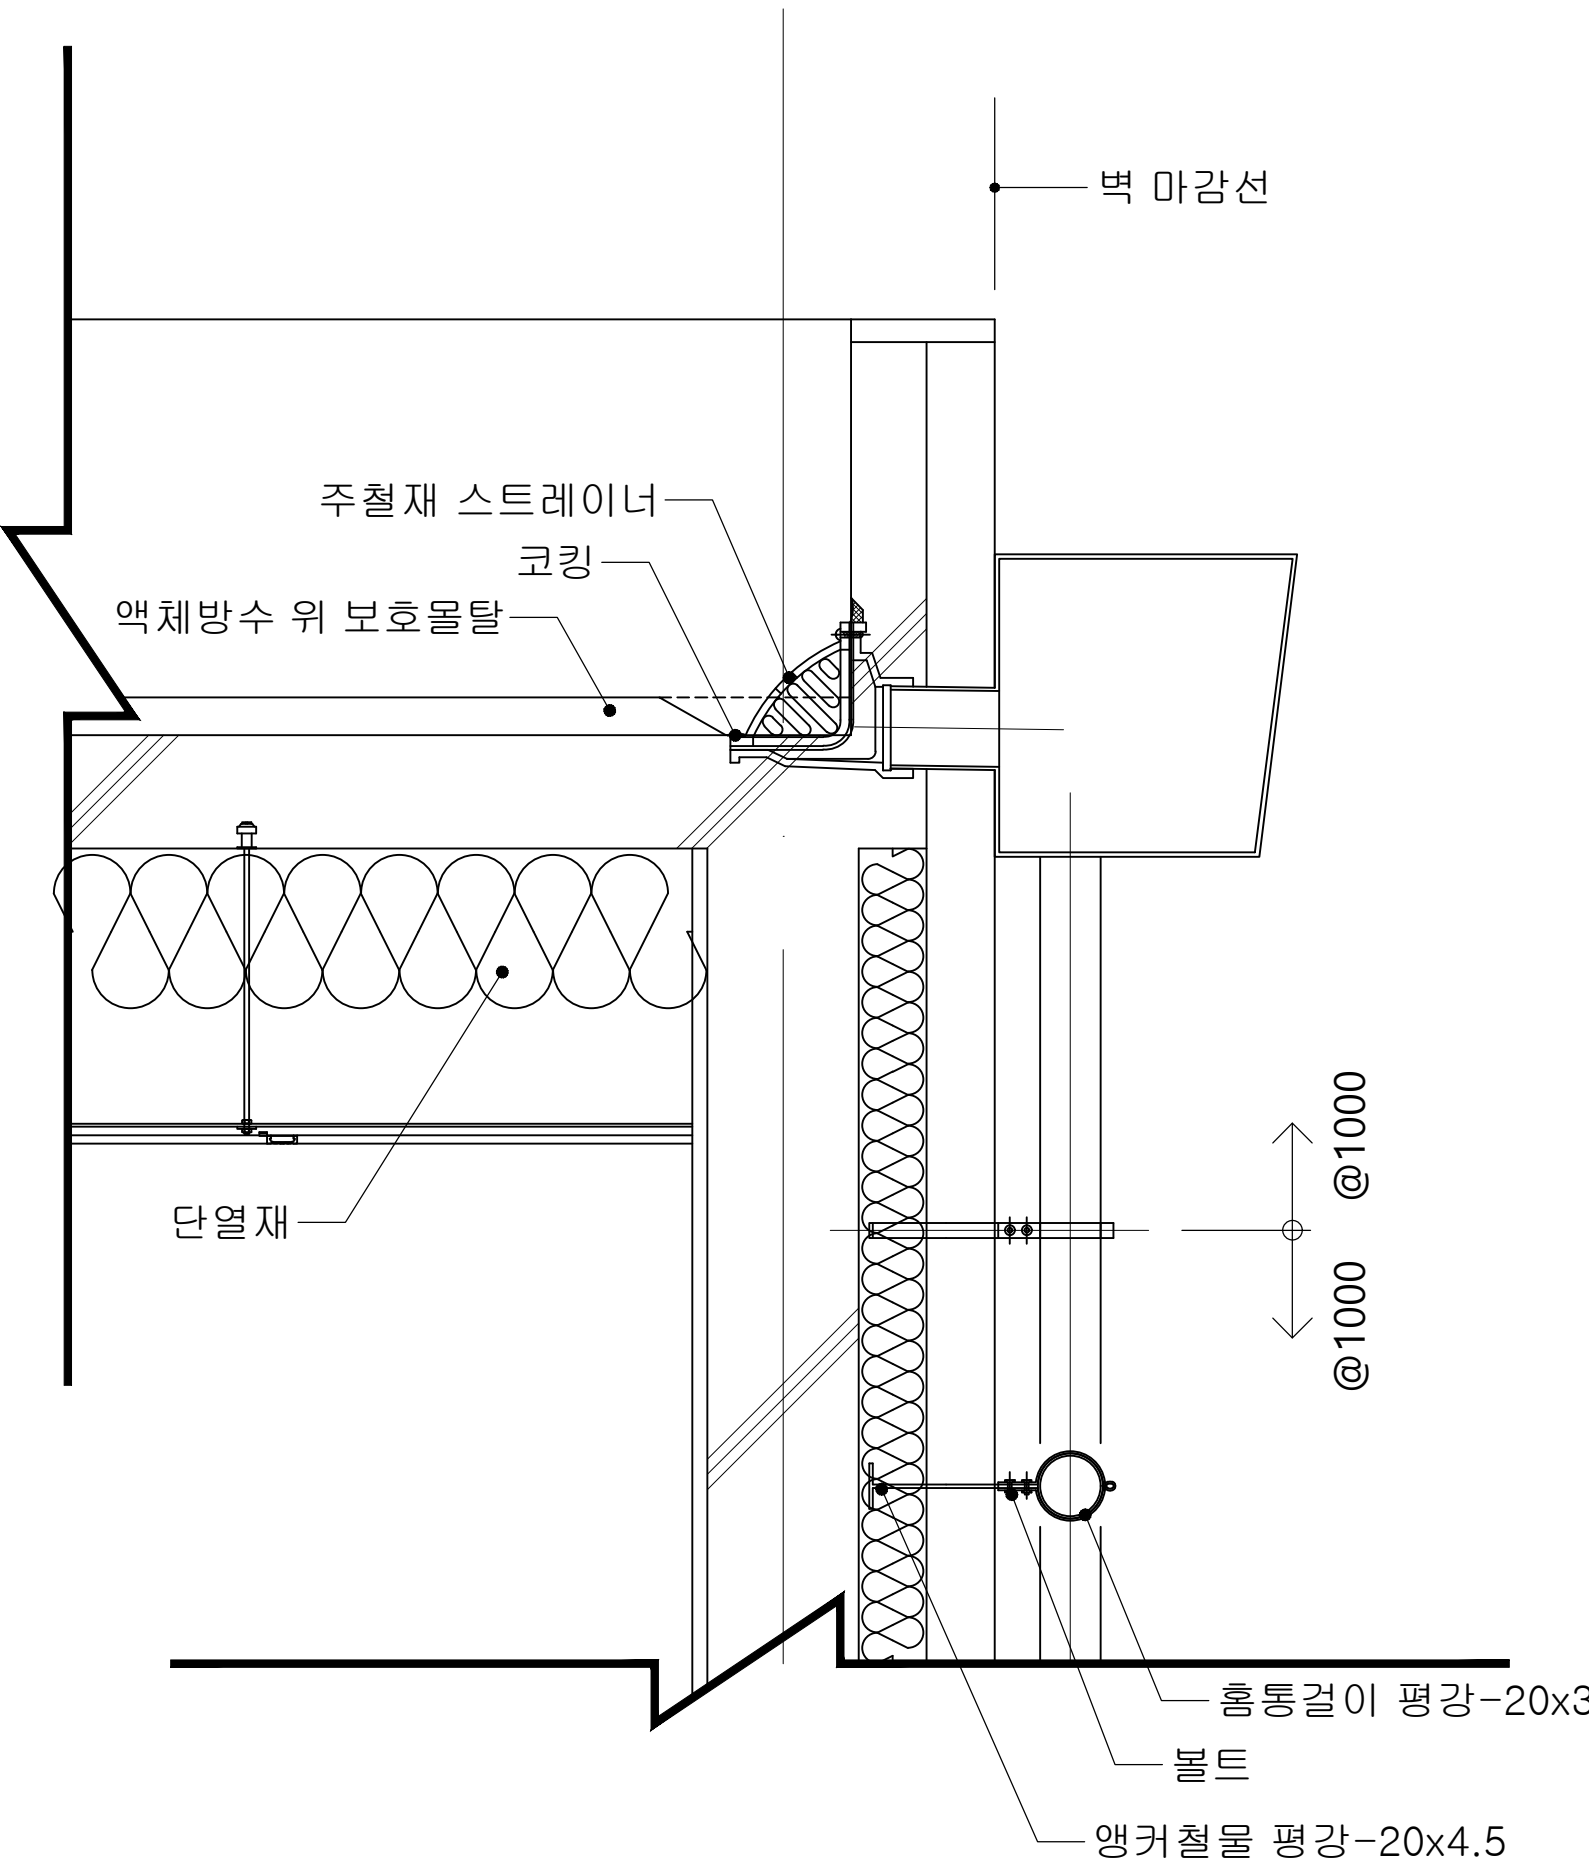

선홍통 상세도
SCALE : 1/10

특기사항
NOTE

수정사항
REVISION

번호 NO	일 자 DATE	수 정 DESCRIPTION	날 인 SIGN
△			
△			
△			
△			
△			
△			
△			
△			
△			

공사명
PROJECT TITLE

축 치
SCALE

작성일
DATE

설 계
DESIGNED BY

제 도
DRAWN BY

검 사
CHECKED BY

승 인
APPROVED BY



도면명
NAME OF DRAWING

도면번호
DRAWING NO

--	--	--	--	--	--

시공번호
PROJECT NO

TD					
----	--	--	--	--	--

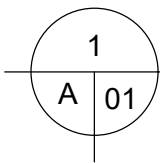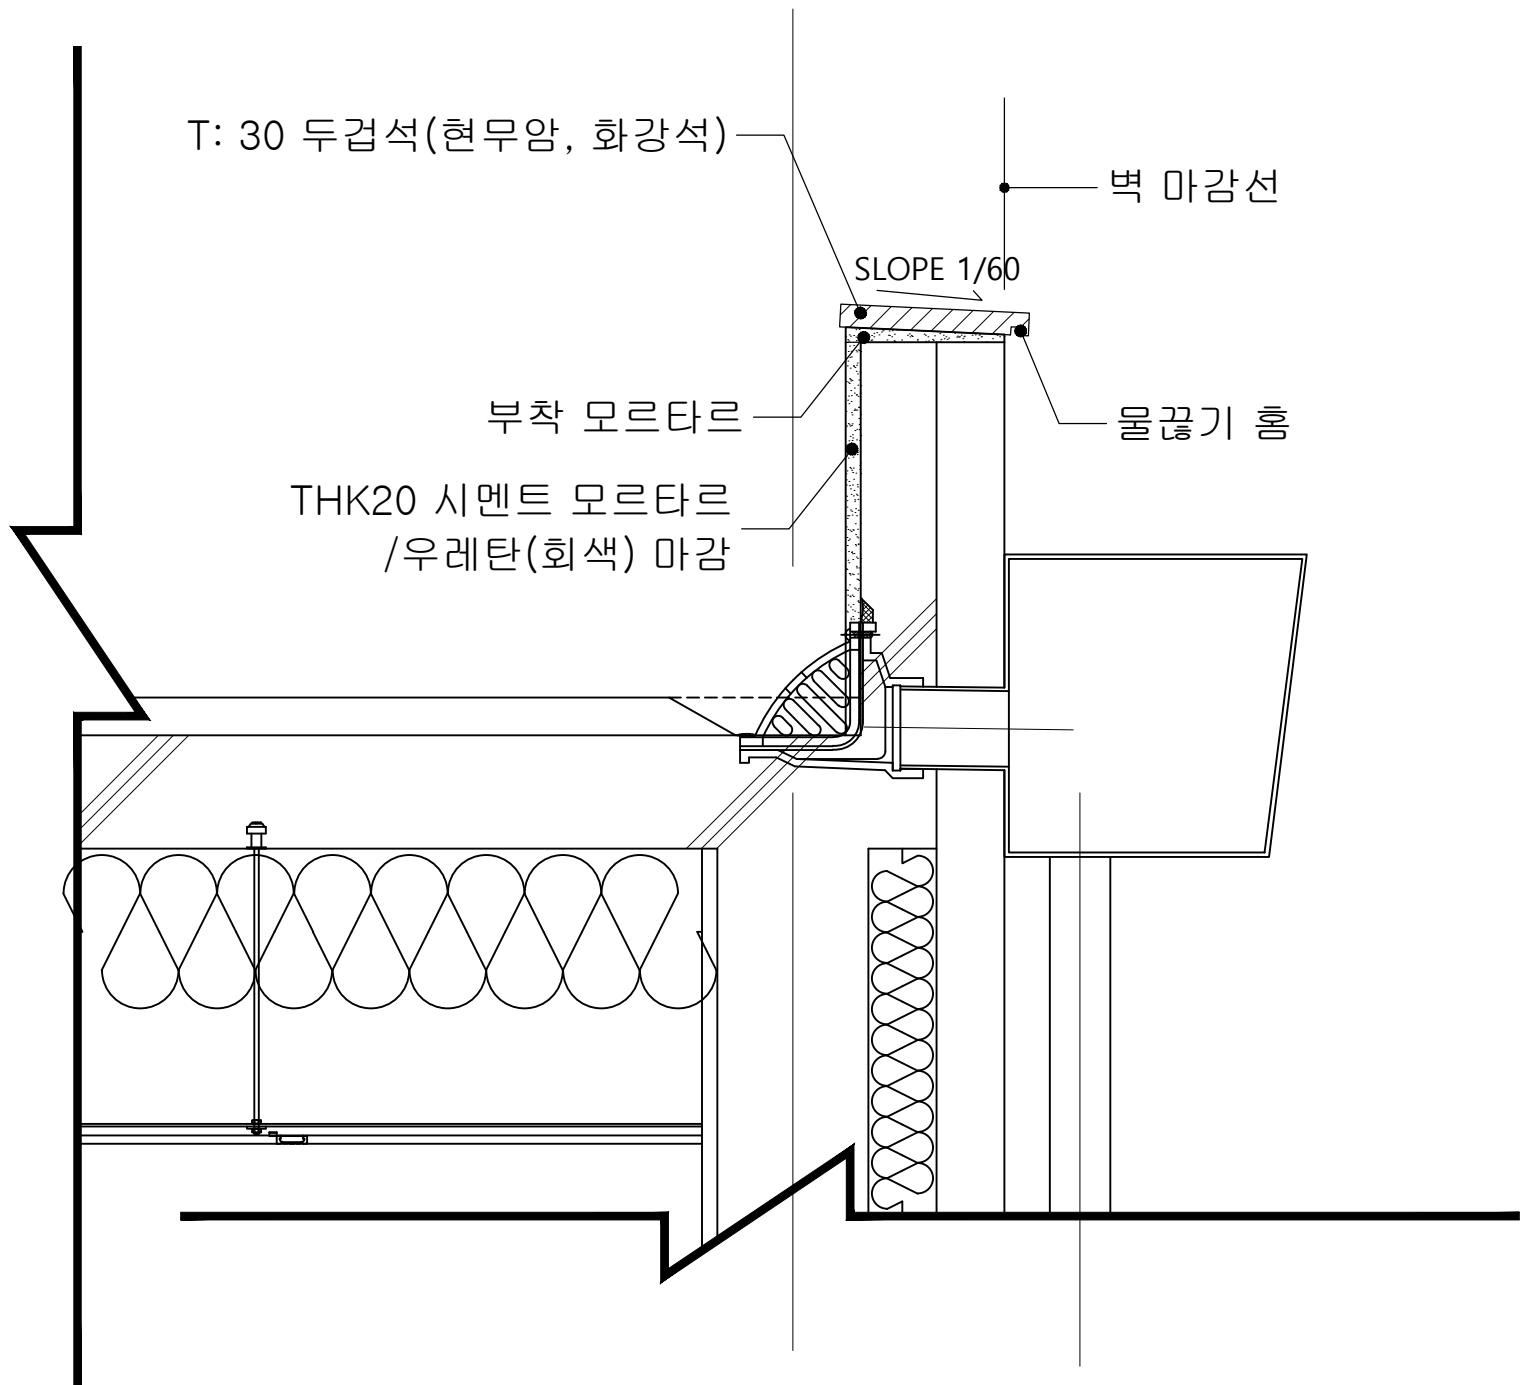

파라펫 상세도

SCALE : 1/10

특기사항
NOTE

수정사항
REVISION

번호 NO	일자 DATE	수정 DESCRIPTION	날인 SIGN
△			
△			
△			
△			
△			
△			
△			
△			
△			
△			

공사명
PROJECT TITLE

축척
SCALE

작성일
DATE

설계
DESIGNED BY

제도
DRAWN BY

검사
CHECKED BY

승인
APPROVED BY

도면명
NAME OF DRAWING

도면번호
DRAWING NO


--	--	--	--	--	--

시공번호
PROJECT NO

TD					
----	--	--	--	--	--

T:12 강화유리
850X760
THK 12


HAND RAIL Ø40X1.6t

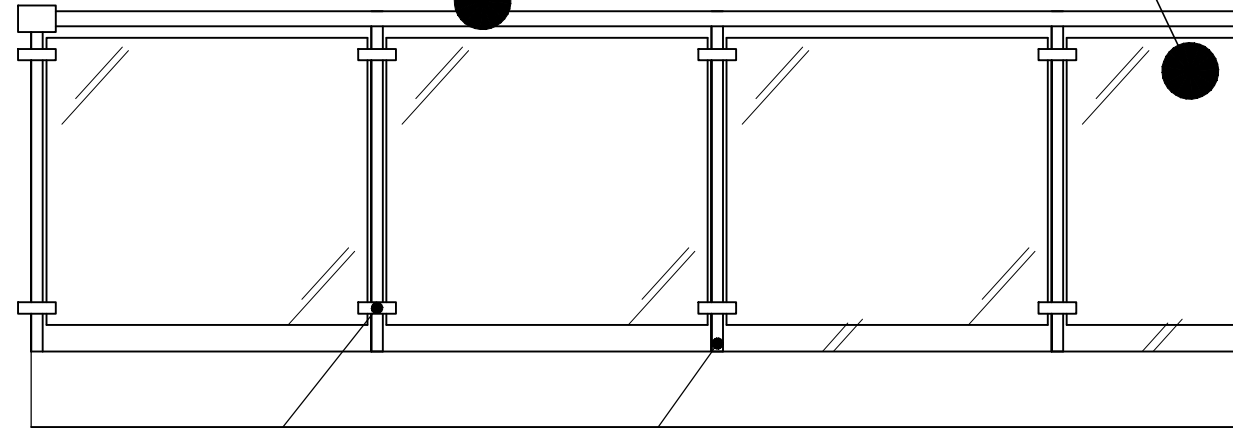

STS ㄷ자 유리클램프

EPDM 고무패킹

STS 고정볼트 Ø8


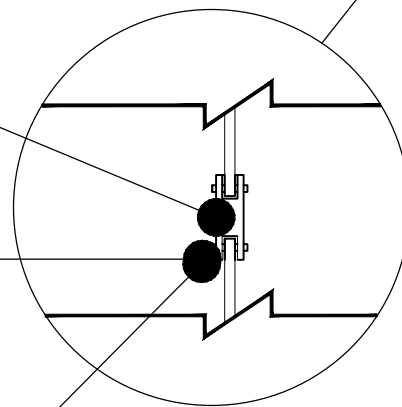


난간 기둥

기초 플레이트 AL 9T

M10~M12 앵커

콘크리트 턱

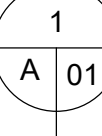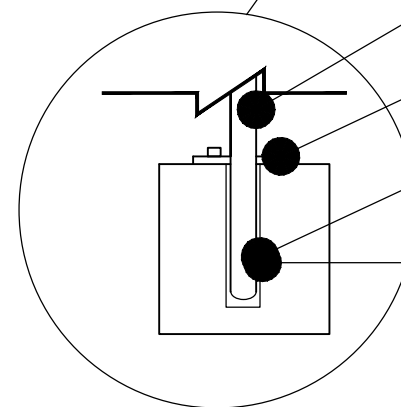

파라펫 상세도

SCALE : 1/20

특기사항
NOTEFck: 240kg/cm²
Fy: 4,000kg/cm²수정사항
REVISION



번호 NO	일 자 DATE	수 정 DESCRIPTION	날 인 SIGN
△			
△			
△			
△			
△			
△			
△			
△			
△			

공사명
PROJECT TITLE축 측
SCALE작성일
DATE설 계
DESIGNED BY제 도
DRAWN BY검 사
CHECKED BY승 인
APPROVED BY도면명
NAME OF DRAWING도면번호
DRAWING NO



--	--	--	--	--	--

사업번호
PROJECT NO

TD					
----	--	--	--	--	--

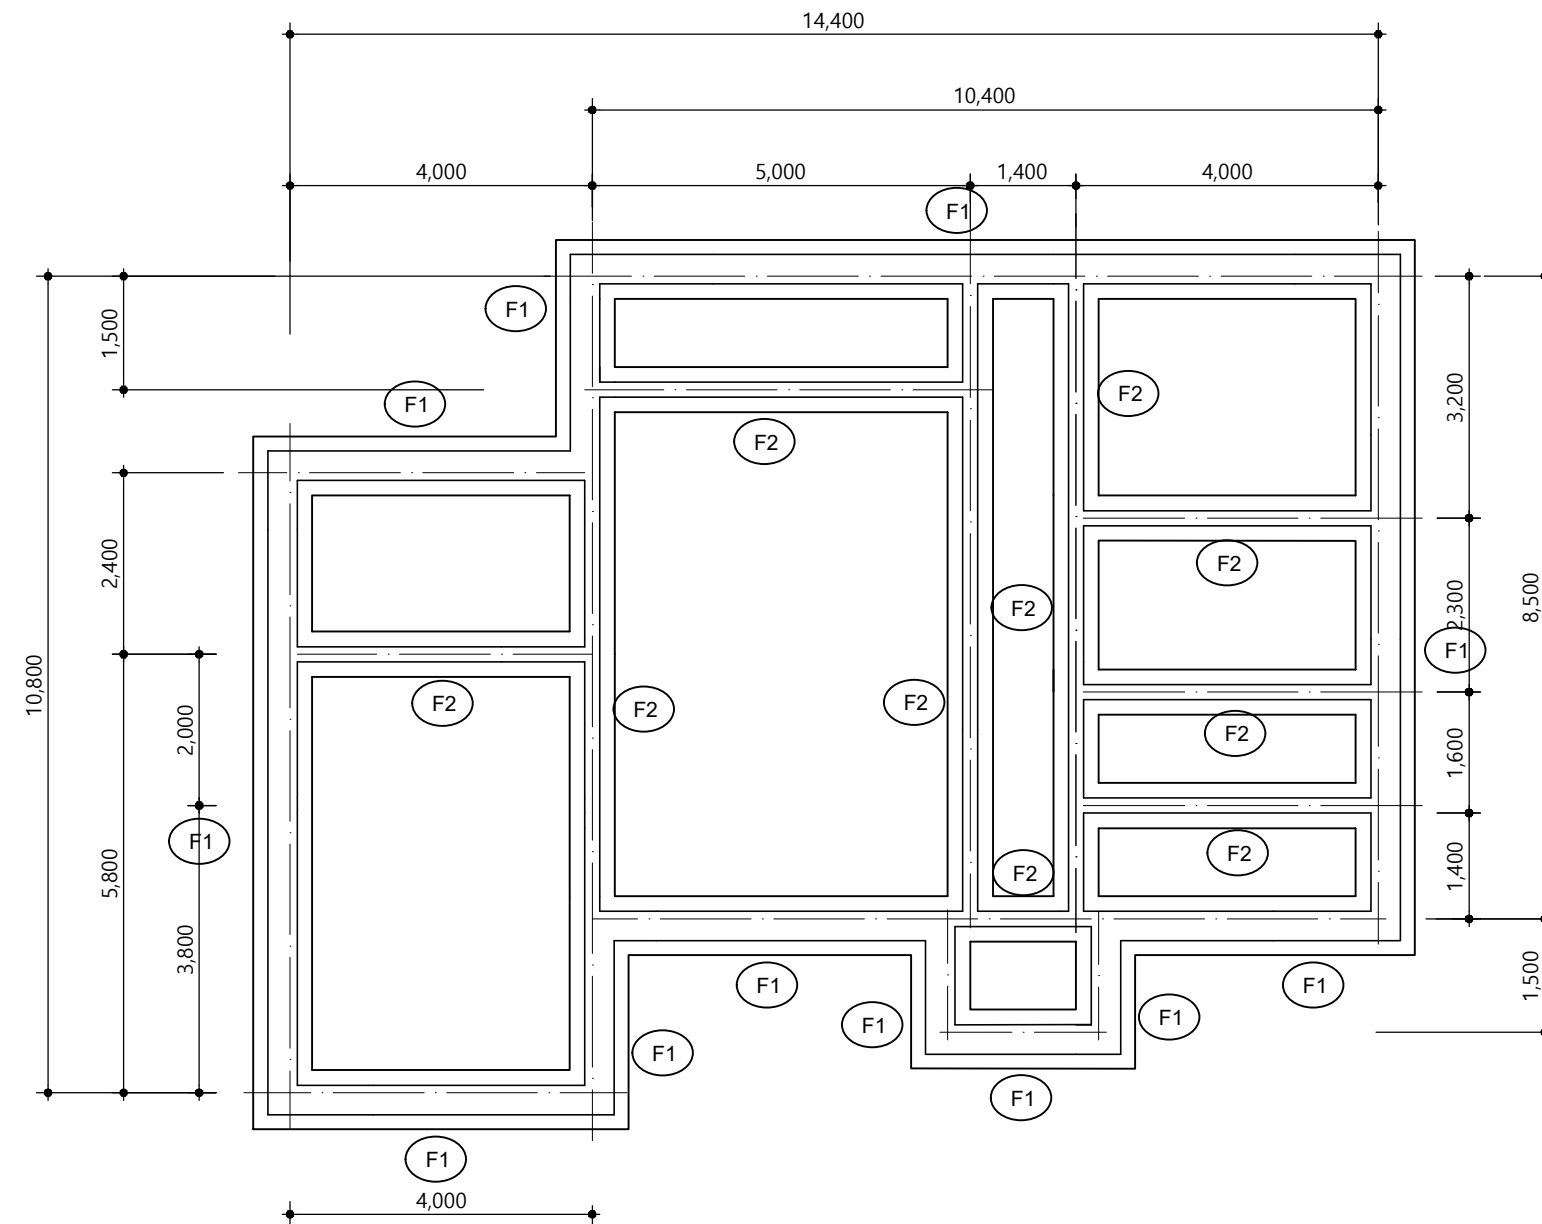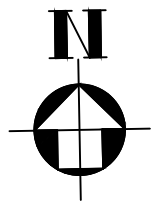

기초 부재리스트

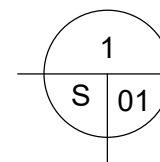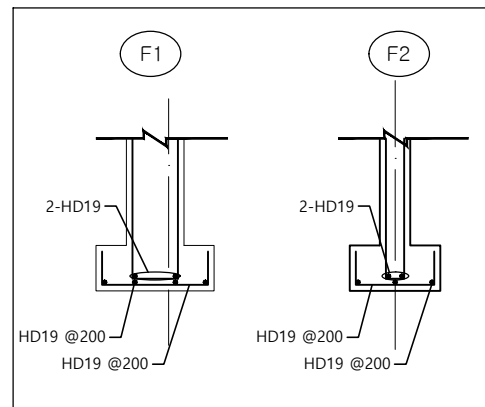

기초 구조평면도

SCALE : 1/100

특기사항
NOTEFck: 240kg/cm²
Fy: 4,000kg/cm²수정사항
REVISION




번호 NO	일 자 DATE	수 정 DESCRIPTION	날 인 SIGN
△			
△			
△			
△			
△			
△			
△			
△			
△			

공사명
PROJECT TITLE축 치
SCALE작성일
DATE설 계
DESIGNED BY제 도
DRAWN BY검 사
CHECKED BY승 인
APPROVED BY도면명
NAME OF DRAWING도면번호
DRAWING NO

--	--	--	--	--	--

사업번호
PROJECT NO

TD					
----	--	--	--	--	--

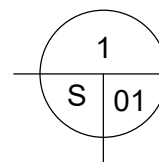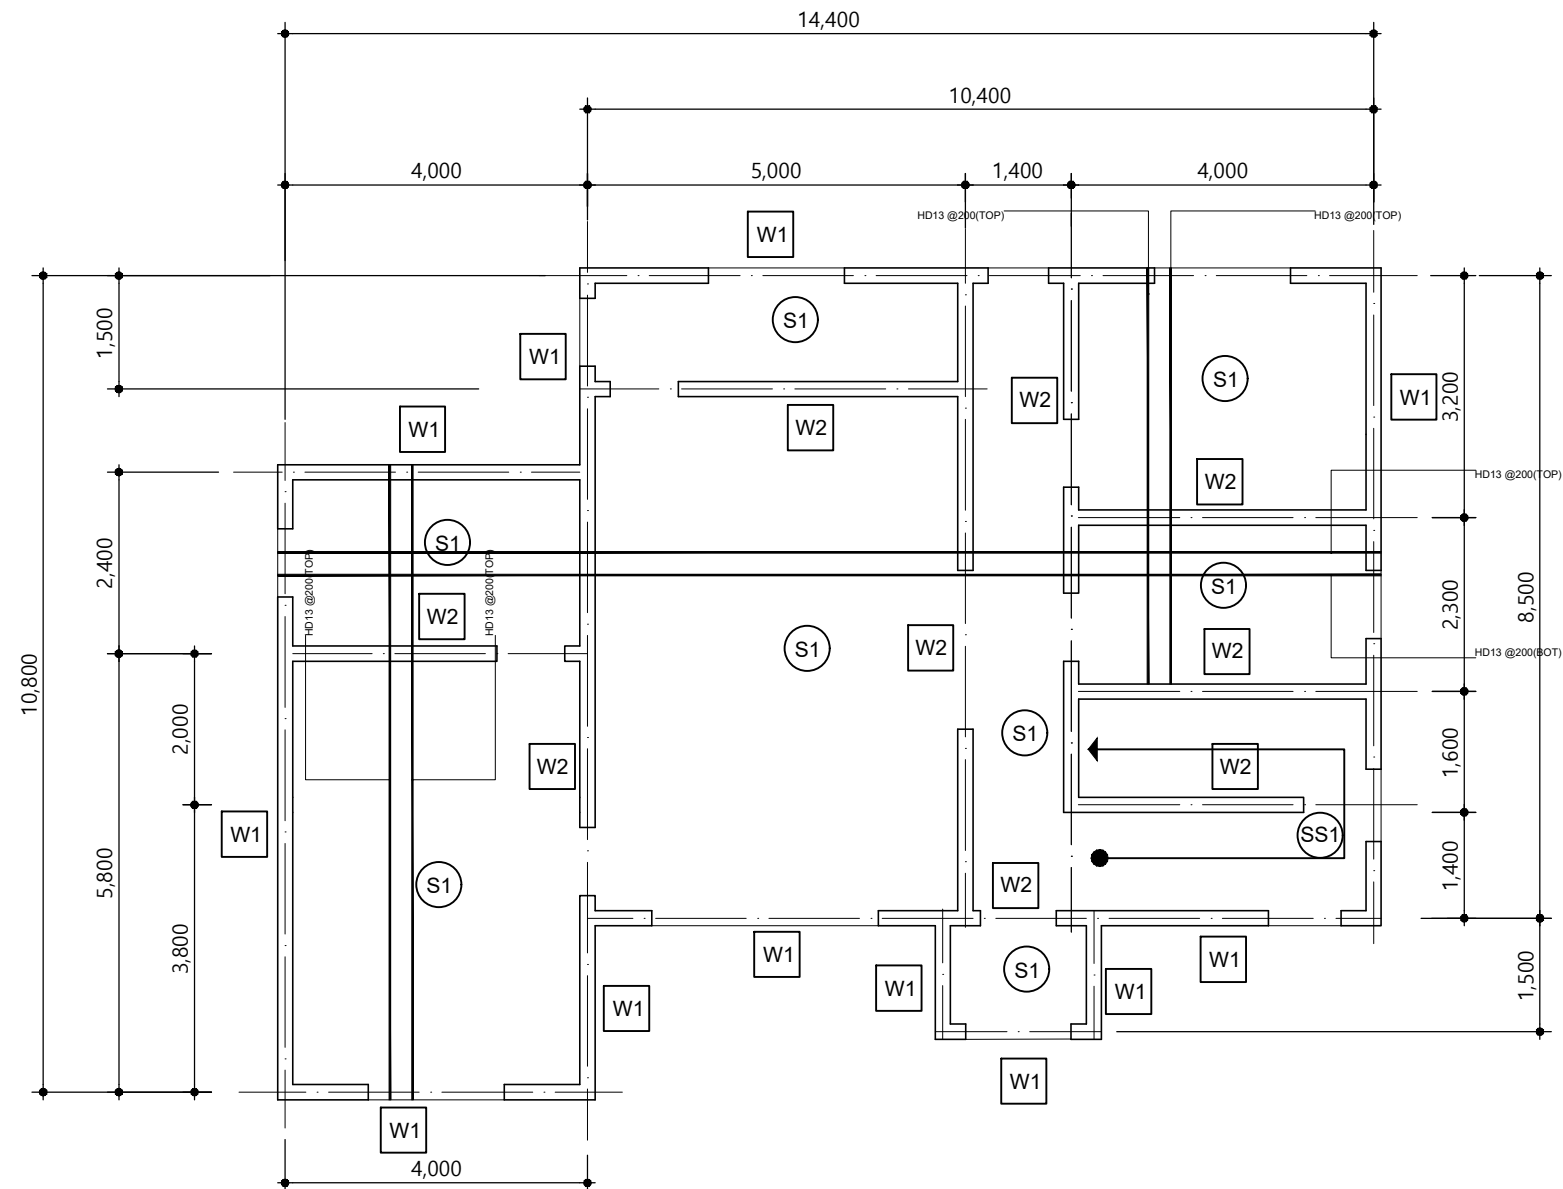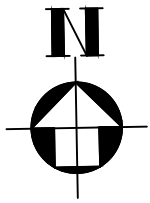

1층 구조평면도

SCALE : 1/100

특기사항
NOTE

Fck: 240kg/cm²
Fy: 4,000kg/cm²

수정사항
REVISION

번호 NO	일 자 DATE	수 정 DESCRIPTION	날 인 SIGN
△			
△			
△			
△			
△			
△			
△			
△			
△			

공사명
PROJECT TITLE

축 척
SCALE

작성일
DATE

설 계
DESIGNED BY

제 도
DRAWN BY

검 사
CHECKED BY

승 인
APPROVED BY




도면명
NAME OF DRAWING

도면번호
DRAWING NO

--	--	--	--	--	--

시공번호
PROJECT NO

TD					
----	--	--	--	--	--

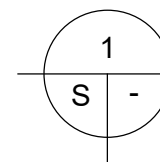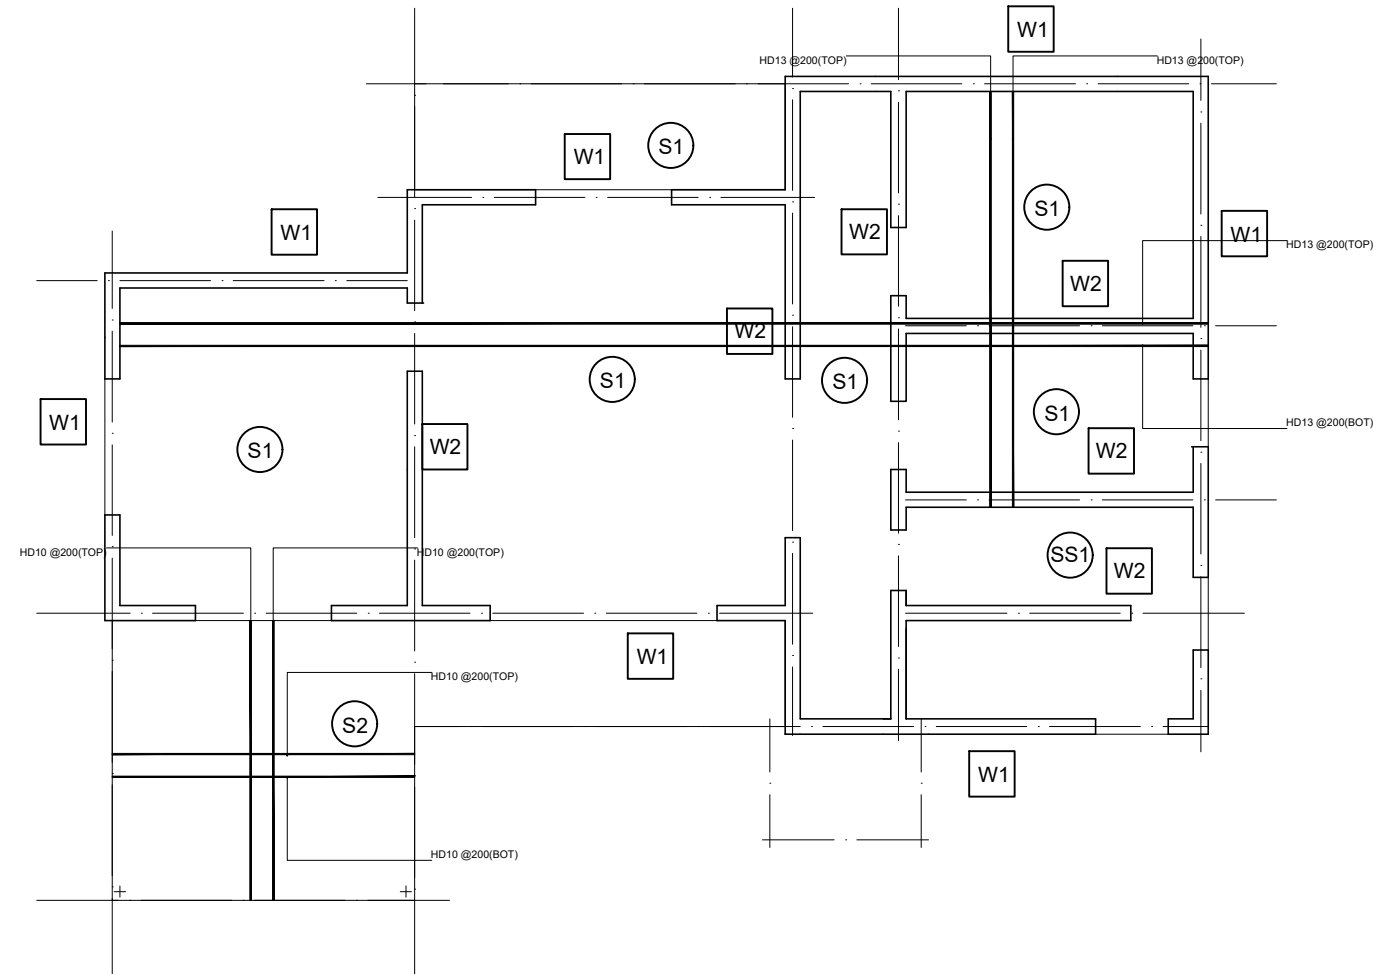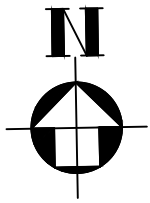

2층 구조평면도

SCALE : 1/100

특기사항
NOTEFck: 240kg/cm²
Fy: 4,000kg/cm²수정사항
REVISION




번호 NO	일 자 DATE	수 정 DESCRIPTION	날 인 SIGN
△			
△			
△			
△			
△			
△			
△			
△			
△			

공사명
PROJECT TITLE축 치
SCALE작성일
DATE설 계
DESIGNED BY제 도
DRAWN BY검 사
CHECKED BY승 인
APPROVED BY도면명
NAME OF DRAWING분류번호
DRAWING NO

--	--	--	--	--	--

시공번호
PROJECT NO

TD					
----	--	--	--	--	--

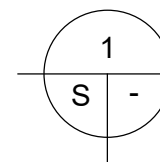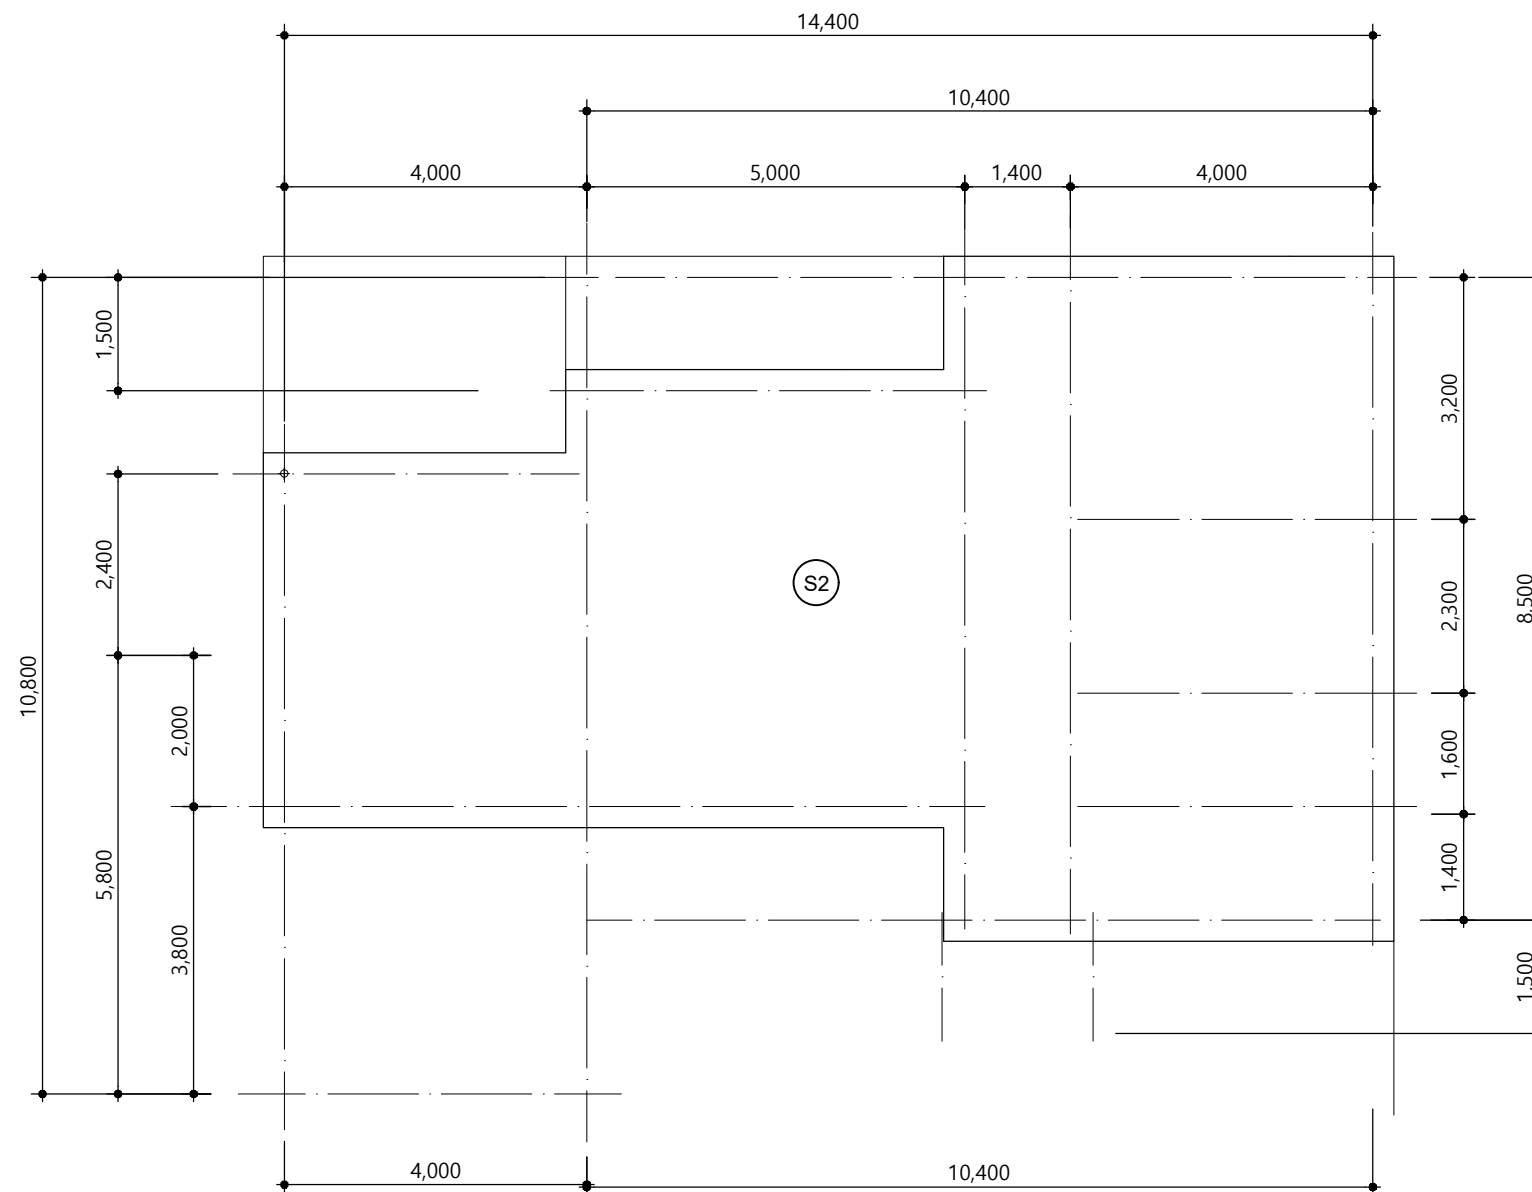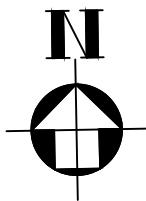

지붕 구조평면도

SCALE : 1/100

특기사항
NOTE

Fck: 240kg/cm²
Fy: 4000kg/cm²

수정사항
REVISION

번호 NO	일자 DATE	수 정 DESCRIPTION	날인 SIGN
△			
△			
△			
△			
△			
△			
△			
△			
△			

공사명
PROJECT TITLE

축
척
SCALE

작성일
DATE

설
계
DESIGNED BY

제
도
DRAWN BY

검
사
CHECKED BY

승
인
APPROVED BY


도면명
NAME OF DRAWING

도면번호
DRAWING NO


--	--	--	--	--	--

시공번호
PROJECT NO


TD					
----	--	--	--	--	--

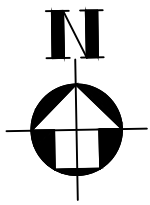


SS1 계단 배근도

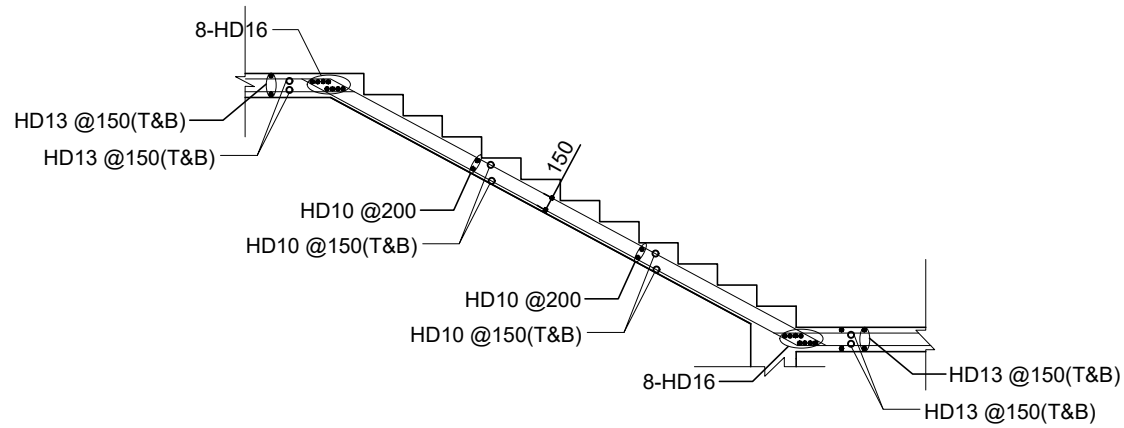

옹벽 배근도 / WALL

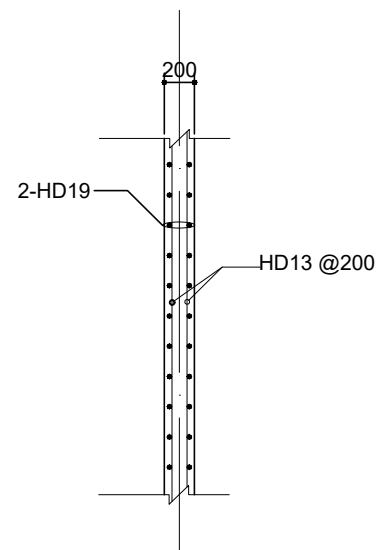

W1

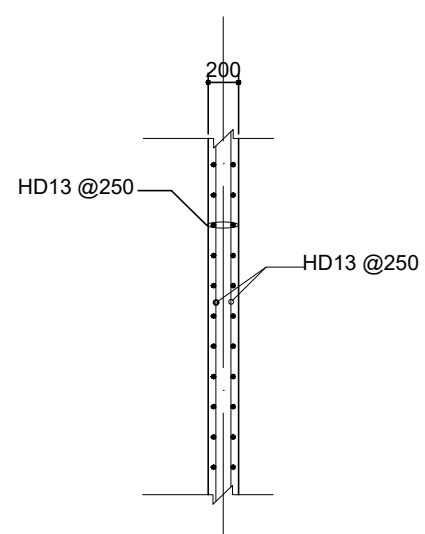

W2

1
S 01

부재 일람표

SCALE : 1/50

구조설계개요

1.1 구조 개요

- 1) 구조 방식 : 철근 콘크리트 벽식 구조
- 2) 기초 형식 : 철근 콘크리트 줄기초

1.2 구조 설계 기준

- 1) 건축물의 구조 기준 등에 관한 규칙(국토교통부)
- 2) 철근 콘크리트 구조계산 및 해설(국토교통부)
- 3) 철근 콘크리트 - 철근 콘크리트 계산규준(국토교통부)
- 콘크리트 구조설계 계산규준(국토교통부)
- 4) 내진설계 지침서 작성에 관한 연구(국토교통부)
참고기준 -ACI 318-83,89

1.3 구조재료의 규격 및 기준 강도

- 1) 콘크리트 : fck = 240 kgf/cm (28 Days)²
- 2) 철 근 : fy = 4,000 kgf/cm (KS D 3504 SD40)

1.4 설계 조건

- 1) 지하 수위 : G.L. -2.0m
- 2) 지내력 기초 : 10.0TON

1.5 특기 사항

- 시공자는 상기사항을 확인하고, 설계자의 승인을 득한후 시공하여야 하며,
상기사항이 현장상황과 불일치 할 경우 설계변경 하여야 한다.
- 기초 공사시 감독관과 협의해서 이질기초의 문제점을 해결 할 것을 요한다.

특기사항

NOTE

수정사항
REVISION

번호 NO	일 자 DATE	수 정 DESCRIPTION	날 인 SIGN
△			
△			
△			
△			
△			
△			
△			
△			
△			

공사명
PROJECT TITLE

축 척
SCALE

작성일
DATE

설 계
DESIGNED BY

제 도
DRAWN BY

검 사
CHECKED BY

승 인
APPROVED BY

도면명
NAME OF DRAWING

도면번호
DRAWING NO

시공번호
PROJECT NO

TD

극한강도 설계법에 의한 철근콘크리트 구조일반사항-1

일 반 사 항



개 요

- 1) 다음의 일반사항 및 표준상세도는 **표준**에 준하였으며 일반구조도에 특별한 사항이 없는 한 모든 도면에 준한다
- 2) 표준 **표**는 표기에 준한다
- 3) 정착길이 및 이음길이는 표기에 준한다
- 4) 기둥 보 용벽 스톱 및 기초배근은 아래표기에 준한다
- 5) 콘크리트 파일길이는 시방타후 결정한다
- 6) 파일 및 지반의 허용내력은 관련도면을 참조한다
단 소정의 내력이 안될 경우 감독의 승인을 얻어 설계변경해야 한다
- 7) 말뚝재하시험은 말뚝 개당 회 또는 지반조건이 현저히 다르거나 다른 형태의 말뚝을 사용할때마다 회이상의 재하시험을 행하여야 한다
- 8) 콘크리트 강도는 관련도면을 참조한다
- 9) 철근의 종류 및 표시방법




SD 40	HD BAR	Fy = 4,000	KG/CM ²
-------	--------	------------	--------------------

철근의 구분

A. HOOK

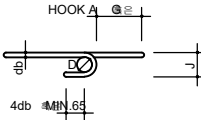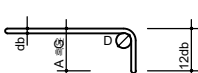
180 HOOK		90 HOOK		
				
D = 6d ~ #8 D = 8d ~ #11				
BAR SIZE	D	180 HOOK		90 HOOK
		A 측은 G	J	A 측은 G
HD 10 (#3)	60	130	75	150
HD 13 (#4)	75	150	100	200
HD 16 (#5)	95	180	130	255
HD 19 (#6)	110	200	150	300
HD 22 (#7)	130	250	180	350
HD 25 (#8)	150	280	200	400
HD 29 (#9)	230	375	285	480
HD 32 (#10)	260	430	320	555

B. STIRRUP AND TIE BAR

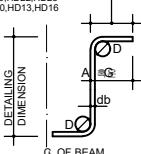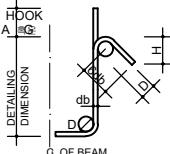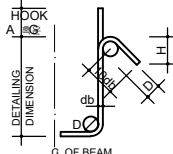GENERAL USE				SEISMIC USE			
90 HOOK		135 HOOK		135 HOOK			
12# FOR HD18,HD22,HD25 6# FOR HD10,HD13,HD15 							
BAR SIZE		D	GENERAL USE		SEISMIC USE		
			90 HOOK	135 HOOK		135 HOOK	
			A 측은 G	A 측은 G	H	A 측은 G	H
HD 10 (#3)		40	100	100	65	130	90
HD 13 (#4)		50	115	115	75	170	110
HD 16 (#5)		65	150	140	95	200	140
HD 19 (#6)		115	305	200	115	280	170
HD 22 (#7)		135	355	230	135	320	200
HD 25 (#8)		150	410	260	150	370	230

철근의 정착 및 이음길이

A) 철근의 정착길이

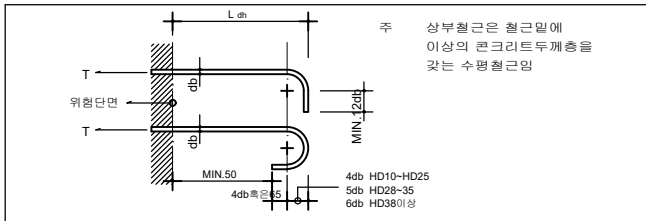

철근호칭	CONC. 설계기준강도 (KG/CM ²)	인 장 철 근				압 축 철 근	
		Ldb	상부철근 L ₁ ≥1.4L _a	Ldh	피도는 나선철근 Ldh	Ldb	나선철근 L ₁ ≥0.75L _a
HD13 HD10	210	300	430	280	220	280	210
	240	300	430	210	260	200	
	240	300	430	240	190	240	200
	300	300	430	240	190	240	200
HD16	210	380	530	350	280	350	260
	240	380	530	330	260	330	250
	240	380	530	300	240	300	230
	300	380	530	300	240	300	230
HD19	210	470	660	420	340	420	320
	240	460	640	390	320	390	300
	240	460	640	370	290	370	240
	300	460	640	350	280	350	260
HD22	210	640	900	490	390	490	370
	240	600	840	460	370	460	340
	240	560	780	420	340	420	320
	300	540	760	410	330	410	310
HD25	210	840	1170	560	450	560	420
	240	780	1100	520	420	520	390
	240	730	1020	490	390	490	360
	300	700	980	460	370	460	350
HD29	210	1060	1490	630	510	630	470
	240	1000	1390	590	470	590	440
	240	920	1290	550	440	550	410
	300	890	1250	540	430	540	410
HD32	210	1320	1840	700	560	700	530
	240	1230	1720	660	530	660	490
	240	1140	1590	610	490	610	460
	300	1100	1540	590	420	590	440

철근호칭	CONC. 설계기준강도 (KG/CM ²)	인 장 철 근				압 축 철 근	
		Ldb	상부철근 L ₁ ≥1.4L _a	Ldh	피도는 나선철근 Ldh	Ldb	나선철근 L ₁ ≥0.75L _a
HD13 HD10	210	300	320	210	170	210	200
	240	300	320	200	160	200	200
	240	300	320	180	150	200	200
	300	300	320	180	150	200	200
HD16	210	300	400	260	210	260	200
	240	300	400	250	200	250	200
	240	300	400	230	180	230	200
	300	300	400	230	190	230	200
HD19	210	360	500	320	250	320	240
	240	340	480	300	240	300	220
	240	340	480	240	220	240	210
	300	340	480	240	220	240	200
HD22	210	480	670	370	290	370	280
	240	450	630	340	280	340	260
	240	420	580	320	250	320	240
	300	400	560	310	250	310	230
HD25	210	630	880	420	340	420	320
	240	590	820	390	310	390	300
	240	550	760	360	290	360	240
	300	530	750	350	280	350	260
HD29	210	800	1120	470	380	470	360
	240	750	1050	440	350	440	330
	240	690	970	410	330	410	310
	300	670	940	280	230	410	310
HD32	210	990	1360	530	420	530	390
	240	920	1290	490	390	490	370
	240	850	1200	460	360	460	340
	300	830	1170	310	250	450	340

기본 정착길이
** 보통골재로서 철근길게 65mm보다 작은 경우 : $L_{dh}=320db/\sqrt{F_c}$ 이며 $F_y=4,000KG/CM^2$
이외의 골재에 대해서는 $F_y/4000$ 를 곱한 값임

B) 철근의 이음길이 (철근간의 순간력 15CM이하)

인장철근의 겹이음길이 (단, B 급이음을 원칙으로 하며 겹이음길이 내에서 전철근량에대한 겹이음된 철근량비가 75% 이상이면 C 급이음을 한다.)

사 소 요	As As	겹이음 길이내에서 전철근량에 대한 겹이음된 철근량의 비(%)		
		50	75	100
2 이상		급 이음	급 이음	급 이음
2 미만		급 이음	급 이음	급 이음

철근의 겹이음길이

인장철근 : $\left[\begin{matrix} \text{급 이음} \\ \text{급 이음} \end{matrix} \right]$ 이상
압축철근 : $\left[\begin{matrix} \text{인장철근의 정착길이가 되어야 하며} \\ \text{2 일때} \end{matrix} \right]$ 이상

철근호칭	CONC. (KG/CM ²) ²	인 장 철 근						압 축 철 근			
		일 부 철 근			상 부 철 근			일반	배 합		
		이 름 의 등 급			이 름 의 등 급				피 환 근	나 선 철 근	
		A13L ³	B13L ³	C13L ³	L ³	A13L ³	B13L ³	C13L ³	L ³	0.831 ³ L ³	0.7 ³ L ³
HD13	210	300	400	520	430	550	730	360	300	300	
	240	300	400	520	430	550	730	360	300	300	
	240	300	400	520	430	550	730	360	300	300	
	300	300	400	520	430	550	730	360	300	300	
HD16	210	380	500	650	530	690	910	450	370	300	
	240	380	500	650	530	690	910	450	370	330	
	240	380	500	650	530	690	910	450	370	330	
	300	380	500	650	530	690	910	450	370	330	
HD19	210	470	620	810	660	860	1130	530	440	400	
	240	460	600	780	640	830	1090	530	440	400	
	240	460	600	780	640	830	1090	530	440	400	
	300	460	600	780	640	830	1090	530	440	400	
HD22	210	640	830	1090	900	1170	1530	620	520	470	
	240	600	780	1020	840	1090	1430	620	520	470	
	240	560	720	940	780	1010	1320	620	520	470	
	300	540	700	920	760	990	1290	620	520	470	
HD25	210	840	1090	1430	1170	1530	2000	710	590	530	
	240	780	1020	1330	1100	1430	1870	710	590	530	
	240	730	950	1240	1020	1320	1730	710	590	530	
	300	700	910	1190	980	1240	1670	710	590	530	
HD29	210	1060	1380	1810	1490	1940	2530	800	660	600	
	240	1000	1290	1690	1390	1810	2370	800	660	600	
	240	920	1200	1570	1290	1680	2190	800	660	600	
	300	890	1160	1510	1250	1630	2130	800	660	600	
HD32	210	1320	1710	2240	1840	2390	3130	890	740	670	
	240	1230	1600	2090	1720	2240	2930	890	740	670	
	240	1140	1480	1940	1590	2070	2710	890	740	670	
	300	1100	1430	1870	1540	2000	2620	890	740	670	

철근호칭	CONC. 설계기준강도 (KG/CM) ²	인 장 철 근						압 축 철 근		
		일반철근			상부철근			일반	배합	
		이음의등급			이음의등급				이철근	나선철근
		AⅡL ⁹ L ⁴	BⅢL ⁷ L ⁴	CⅢL ⁷ L ⁴	AⅡL ⁹ L ⁴	BⅢL ⁷ L ⁴	CⅢL ⁷ L ⁴	L ⁴		
HD13 HD13	210	300	300	390	320	420	540	300	300	300
	240	300	300	390	320	420	540	300	300	300
	240	300	300	390	320	420	540	300	300	300
	300	300	300	390	320	420	540	300	300	300
HD16	210	300	370	490	400	520	680	330	300	300
	240	300	370	490	400	520	680	330	300	300
	240	300	370	490	400	520	680	330	300	300
	300	300	370	490	400	520	680	330	300	300
HD19	210	360	460	600	500	650	850	400	330	300
	240	340	450	580	480	630	820	400	330	300
	240	340	450	580	480	630	820	400	330	300
	300	340	450	580	480	630	820	400	330	300
HD22	210	480	630	820	670	880	1140	470	390	350
	240	450	580	760	630	820	1070	470	390	350
	240	420	540	710	580	760	990	470	390	350
	300	400	520	680	560	730	950	470	390	350
HD25	210	630	820	1070	880	1150	1500	530	440	400
	240	590	770	1000	820	1070	1400	530	440	400
	240	550	710	930	760	990	1300	530	440	400
	300	530	690	900	750	980	1280	530	440	400
HD29	210	800	1040	1360	1120	1450	1900	600	500	450
	240	750	970	1240	1050	1360	1780	600	500	450
	240	690	900	1170	970	1260	1640	600	500	450
	300	670	870	1140	940	1220	1600	600	500	450
HD32	210	990	1280	1680	1380	1800	2350	670	550	500
	240	920	1200	1570	1290	1680	2200	670	550	500
	240	850	1110	1450	1200	1550	2030	670	550	500
	300	830	1080	1410	1170	1520	1990	670	550	500

TD □ □ □ □ □

극한강도 설계법에 의한 철근콘크리트 구조일반사항-3

EZDESIGN
이지디자인컴퓨터학원

(043)272-3550~1

특기사항
NOTE

수정사항
REVISION

번호 NO	일자 DATE	수 정 DESCRIPTION	날인 SIGN
△			
△			
△			
△			
△			
△			
△			
△			
△			
△			
△			
△			
△			

공사명
PROJECT TITLE

축척
SCALE

작성일
DATE

설계
DESIGNED BY

제 도
DRAWN BY

검 사
CHECKED BY

승 인
APPROVED BY

도면명
NAME OF DRAWING

도면번호
DRAWING NO


시공번호
PROJECT NO

TD-□□□□□□


5 슬라브 배근

방향 슬라브 배근

5-1)-1. BEND TYPE

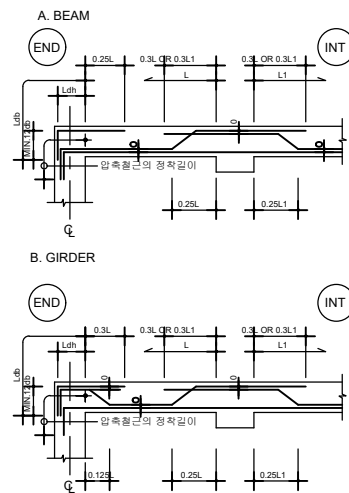


5-1)-2. CUT TYPE

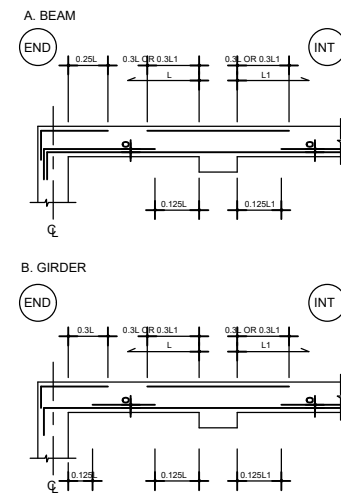


방향 슬라브 배근

ACI METHOD 2 에 의한 슬라브 배근도

의 지간은 지점사이의 중심간거리로 순지간에
슬라브두께의 배를 합한 값중 적은 값으로 한다

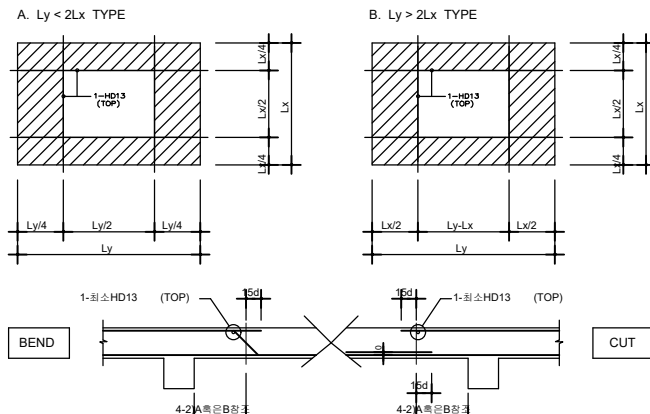


계단의 배근

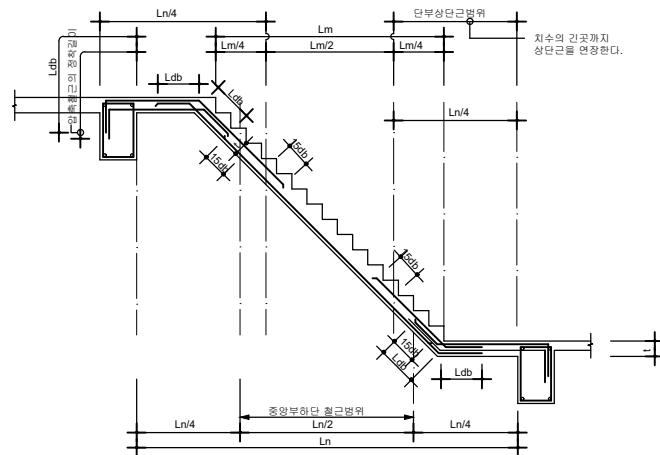


5-4) 슬래브 단차가 있는 경우 수직배근도

(보강근은 HD13이상으로 한다.)

(중앙부)

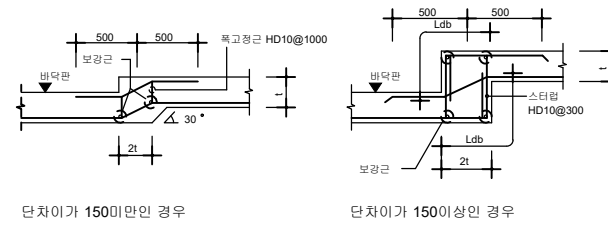


(단 부)

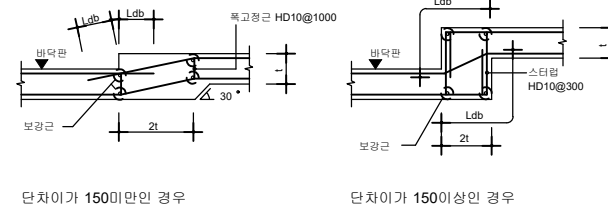


5-5) 보에 만나는 슬래브에 단차가 있는 경우 수직배근도


2t 이상일때

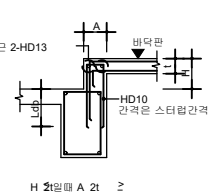

100 < A < 2t일때

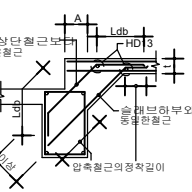


A 2t일때

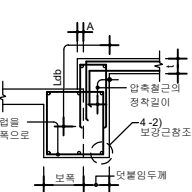

6 벽 배근


6-1) 외부 모서리부분 수평배근도

(보강근은 HD13이상으로 한다.)

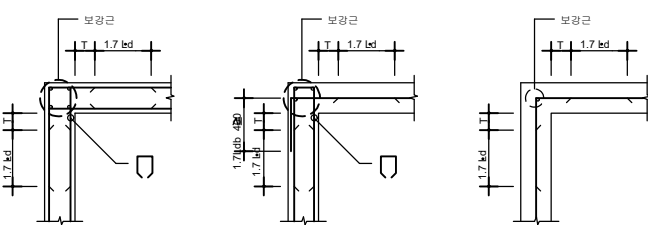

6-2) 교차되는 부분 수평배근도


(보강근은 HD13이상으로 한다.)

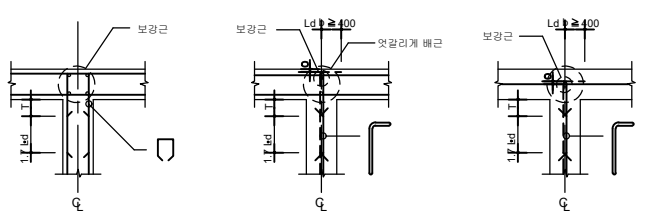


6-3) 내력벽과 슬라브 수직배근도

(보강근은 HD13이상으로 한다.)


(벽배근)

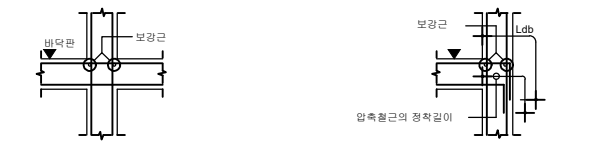


(단배근)

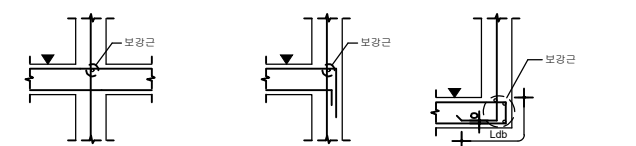


6-4) 내력벽과 최상층 슬라브 (수직배근도)

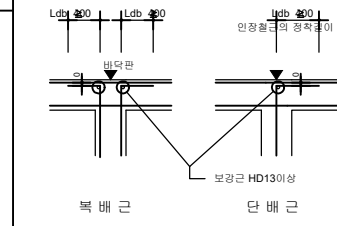

6-5) 내력벽과 캔디레버 슬라브 (수직배근도)

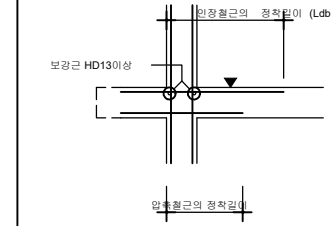


7 기초 배근

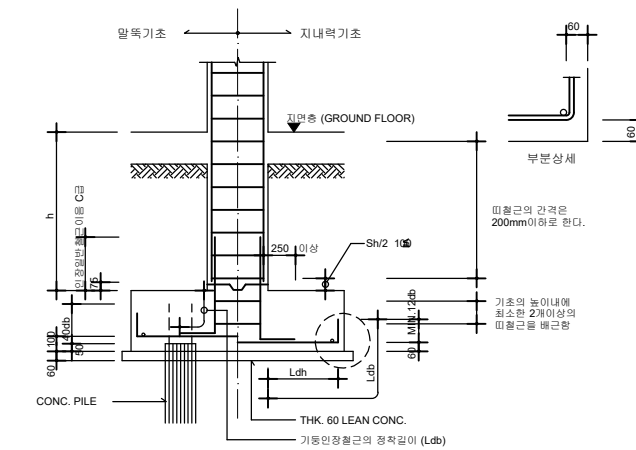

8 옹벽 개구부 배근

(단, 최소보강근임)

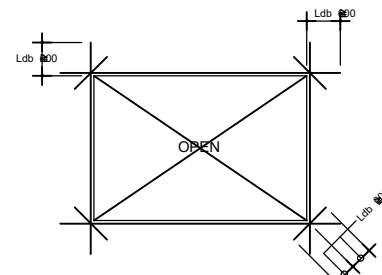

옹벽 두께	가로근	세로근	경사근
150	1-HD16	1-HD16	1-HD16
180	2-HD16	2-HD16	2-HD16
200	2-HD16	2-HD16	2-HD16
220	2-HD16	2-HD16	2-HD16
250	2-HD19	2-HD19	2-HD19
280	2-HD19	2-HD19	2-HD19
300	2-HD19	2-HD19	2-HD19
350	2-HD22	2-HD22	2-HD22
400	2-HD22	2-HD22	2-HD22

극한강도 설계법에 의한 철근콘크리트 구조일반사항-4

EZDESIGN
이지디자인컴퓨터학원

(043)272-3550~1

특기사항

NOTE

수정사항

REVISION

번호 NO	일 자 DATE	수 정 DESCRIPTION	날 인 SIGN
△			
△			
△			
△			
△			
△			
△			
△			
△			

공사명

PROJECT TITLE

축척

SCALE

작성일

DATE

설계

DESIGNED BY

제도

DRAWN BY

검사

CHECKED BY

승인

APPROVED BY

도면명

NAME OF DRAWING

도면번호

DRAWING NO

--	--	--	--	--	--

시공번호

PROJECT NO

TD					
----	--	--	--	--	--

A	옹벽 배근 일반사항	B 기본 수직 보강근 수평배근도 (주 배근방법은 철근콘크리트 구조일반 참조)			
두께가 이상인 외부벽은 복배근으로 한다 최상층 전 후면 측면 옥탑층 외벽의 수직근은 이하로 복배근하고 수평근은 이하로 복배근한다 간격이 이상이면 로 배근한다		B-1	B-2	B-3	B-4
C	기본 옹벽 배근도 수평배근도	D	옹벽 층별연결부 상세 수직배근도		
E	옹벽 층간 배근요령 수직배근도 단배근 및 복배근 동일				
F	보스트럽 배근도				
I	연속교 슬라브 콘크리트 타설순서				